

«ООО Творческая мастерская
архитектора Иняева А.А.»

Храм Рождества Пресвятой Богородицы по адресу ул. Березовская рядом с
профилакторием в Московском р-не г. Нижний Новгород

0143.03.2023-АР



ГАП

Иняев В.А.

г. Нижний Новгород 2024 г.

Инв. № подл.	Подп. и дата	Взам. инв. №	Согласовано		

Ведомость чертежей	
№ П.П.	Наименование
1.	Ведомость чертежей.
2.	Визуализация 1.
3.	Визуализация 2.
4.	Аксонометрия 1.
5.	Аксонометрия 2.
6.	Фасад М-А. Фасад 1-8. М 1:100. Цветовое решение. М 1:100.
7.	Фасад А-М. Фасад 8-1. М 1:100. Цветовое решение. М 1:100.
8.	План подклета на отм.-3,200. М 1:50.
9.	План 1-го этажа на отм.±0,000. М 1:50.
10.	План колокольни на отм.+5,900. М 1:50.
11.	План колокольни и план главного восьмерика на отм.+9,300. М1:50.
12.	План кровли. М 1:50.
13.	Разрез 1-1. М 1:100.
14.	Разрез 2-2. Разрез 3-3. М 1:100.
15.	Разрез 4-4. Разрез 5-5. М 1:100.
16.	Фасад М-А. Фасад 1-8. М 1:100.
17.	Фасад А-М. Фасад 8-1. М 1:100.
18.	Фрагмент главного шатра.
19.	Фрагмент колокольни.
20.	Фрагмент - наличники 1, М 1:20.
21.	Фрагмент - наличник 3. Фрагмент - наличники 2. М 1:20.
22.	Фрагмент - портал главного входа. Узел 1. Узел 2. М 1:20.
23.	Спецификация заполнения дверных проемов. Спецификация заполнения оконных проемов. Ведомость отделки помещений. Экспликация полов.

Принятые в комплекте АР технические решения соответствуют требованиям экологических, санитарно-гигиенических, противопожарных и других норм, действующих на территории Российской Федерации, и обеспечивают безопасную для жизни и здоровья людей эксплуатацию объекта при соблюдении предусмотренных рабочими чертежами мероприятий.

ГИП

 Иняев А. А.

Общие данные

1. Документация на Храм Рождества Пресвятой Богородицы по адресу ул. Березовская рядом с профилакторием в Московском р-не г. Нижний Новгород разработана на основании следующих исходных данных:
 - градостроительный план земельного участка №RU52303000-0000000000001424 Арх.№702-НО
 - задание на проектирование;
 - градостроительный план земельного участка;
 - технического отчета по результатам инженерно-геодезических и инженерно-геологических изысканий для разработки проектной и рабочей документации;
2. За относительную отметку 0,000 принята отметка уровня чистого пола 1-го этажа, что соответствует абсолютной отметке БСК +79,970.
3. При проектировании несущих и ограждающих конструкций нагрузки и воздействия приняты исходя из условий района строительства и с учетом:
 - расчетной зимней температуры - -32°C
 - расчетной снеговой нагрузки для IV района - 240кг/м^2 ;
 - скоростного напора для I ветрового района 23кг/м^2 ;
 - временной нагрузки на перекрытии в соотв. с СП 20.13330.2016;
 - временной нагрузки на фундаментные плиты СП 20.13330.2016, СП 43.13330.2012;

Технико - экономические показатели :

- | | | |
|--------------------------------|---|------------|
| 1. Площадь земельного участка | - | 0,235 Га |
| 2. Общая площадь храма | - | 324,90 м2 |
| в т.ч. план на отм -3,200 | - | 132,40 м2 |
| 3. Полезная площадь храма | - | 60,00 м2 |
| 4. Площадь застройки храма | - | 299,00 м2 |
| 5. Вместимость храма | - | 50 мест |
| 6. Количество этажей | - | 2 этажа |
| 7. Строительный объем храма | - | 2284,32 м3 |
| в т.ч. подвала | - | 690,50 м3 |
| 8. Количество парковочных мест | - | 10м/м |

						0143.03.2023-АР				
						Храм Рождества Пресвятой Богородицы по адресу ул. Березовская рядом с профилакторием в Московском р-не г. Нижний Новгород				
Изм.	Кол.Уч	Лист	№док	Подпись	Дата					
Разработал		Иняев В.А.						Стадия	Лист	Листов
ГАП		Иняев А.А.						П	1	
						Ведомость чертежей. Общие данные.		«ООО Творческая мастерская архитектора Иняева А.А.»		
Н.контр.		Иняев А.А.								

Согласовано				
Инов. № подл.	Подп. и дата	Взам. инв. №		




						0143.03.2023-AP			
						Храм Рождества Пресвятой Богородицы по адресу ул. Березовская рядом с профилакторием в Московском р-не г. Нижний Новгород			
Изм.	Кол.Уч	Лист	№док	Подпись	Дата				
Разработал		Иняев В.А.				Стадия		Лист	Листов
ГАП		Иняев А.А.				П		2	
Н.контр.		Иняев А.А.				Визуализация 1.		«ООО Творческая мастерская архитектора Иняева А.А.»	

Согласовано				
Инов. № подл.	Подп. и дата	Взам. инв. №		



						0143.03.2023-AP						
						Храм Рождества Пресвятой Богородицы по адресу ул. Березовская рядом с профилакторием в Московском р-не г. Нижний Новгород						
Изм.	Кол.Уч	Лист	№док	Подпись	Дата		Стадия	Лист	Листов			
Разработал		Иняев В.А.						П	3			
ГАП		Иняев А.А.				Визуализация 2.		«ООО Творческая мастерская архитектора Иняева А.А.»				
Н.контр.		Иняев А.А.										


Согласовано

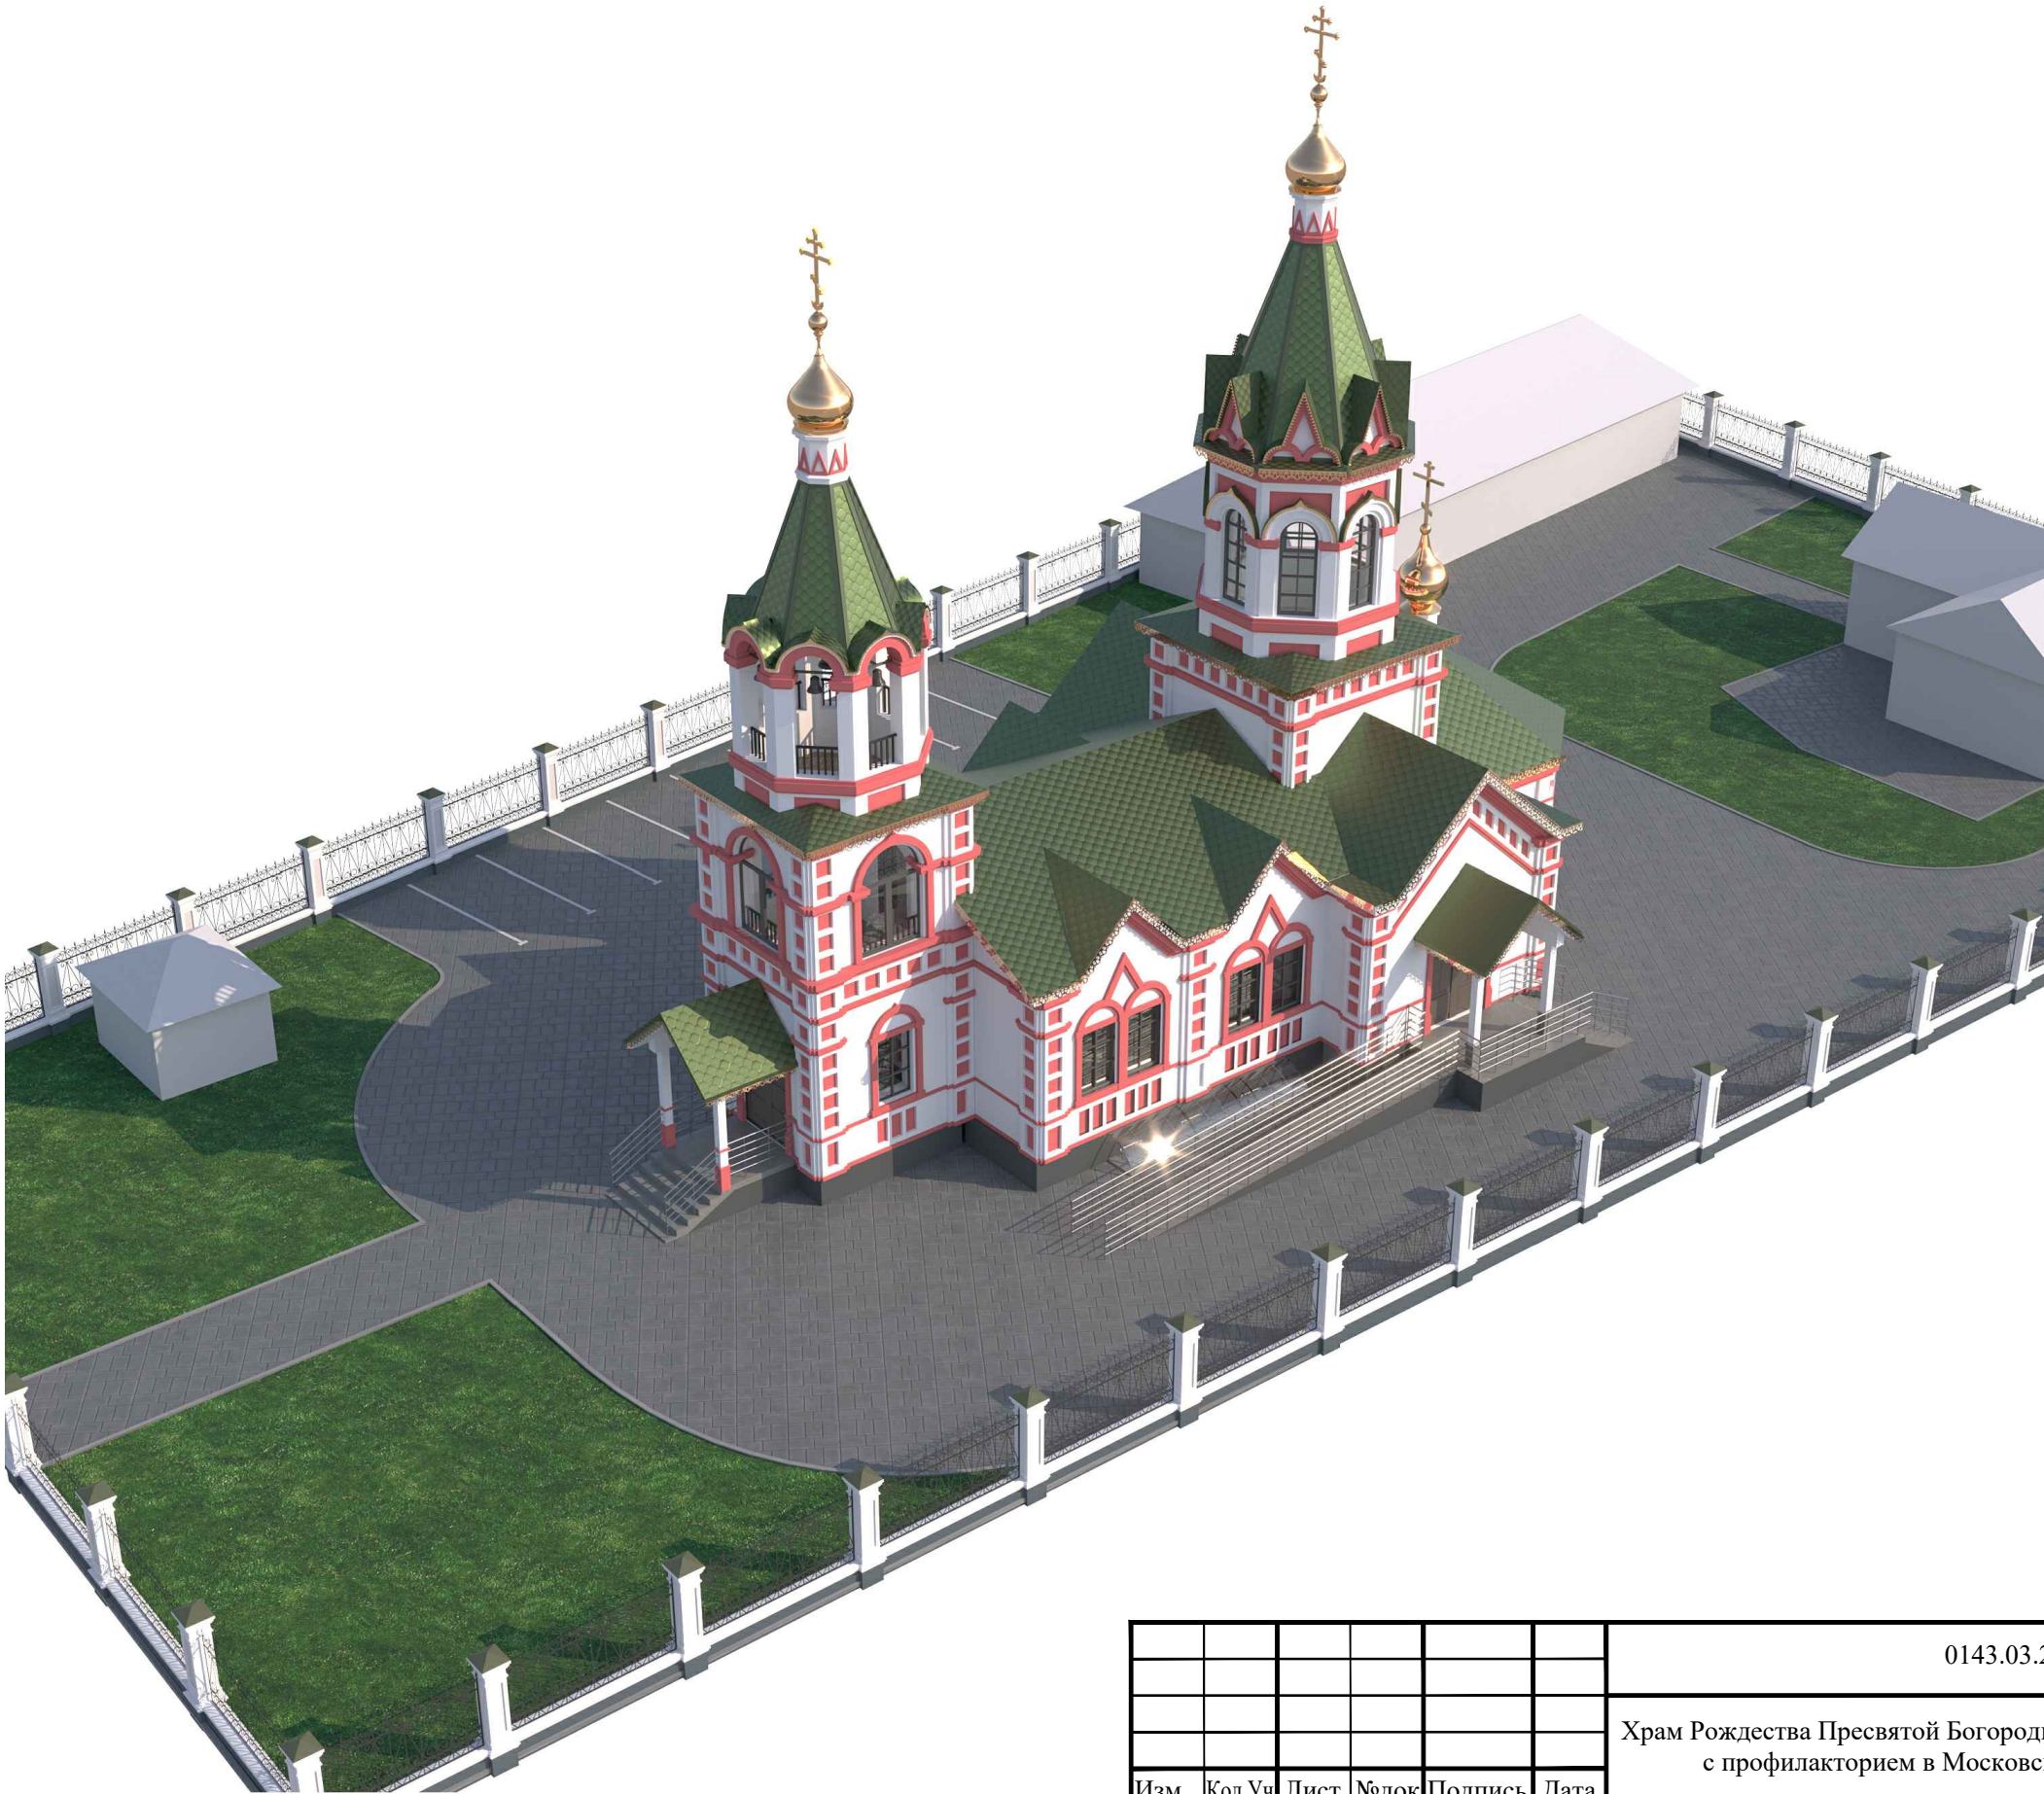

Согласовано					
Инв. № подл.	Подп. и дата	Взам. инв. №			

						0143.03.2023-AP				
						Храм Рождества Пресвятой Богородицы по адресу ул. Березовская рядом с профилакторием в Московском р-не г. Нижний Новгород				
Изм.	Кол.Уч	Лист	№док	Подпись	Дата					
Разработал		Иняев В.А.						Стадия	Лист	Листов
ГАП		Иняев А.А.						П	4	
								«ООО Творческая мастерская архитектора Иняева А.А.»		
Н.контр.		Иняев А.А.				Аксонометрия 1.				

Инв. № подл.	Подп. и дата	Взам. инв. №	Согласовано			

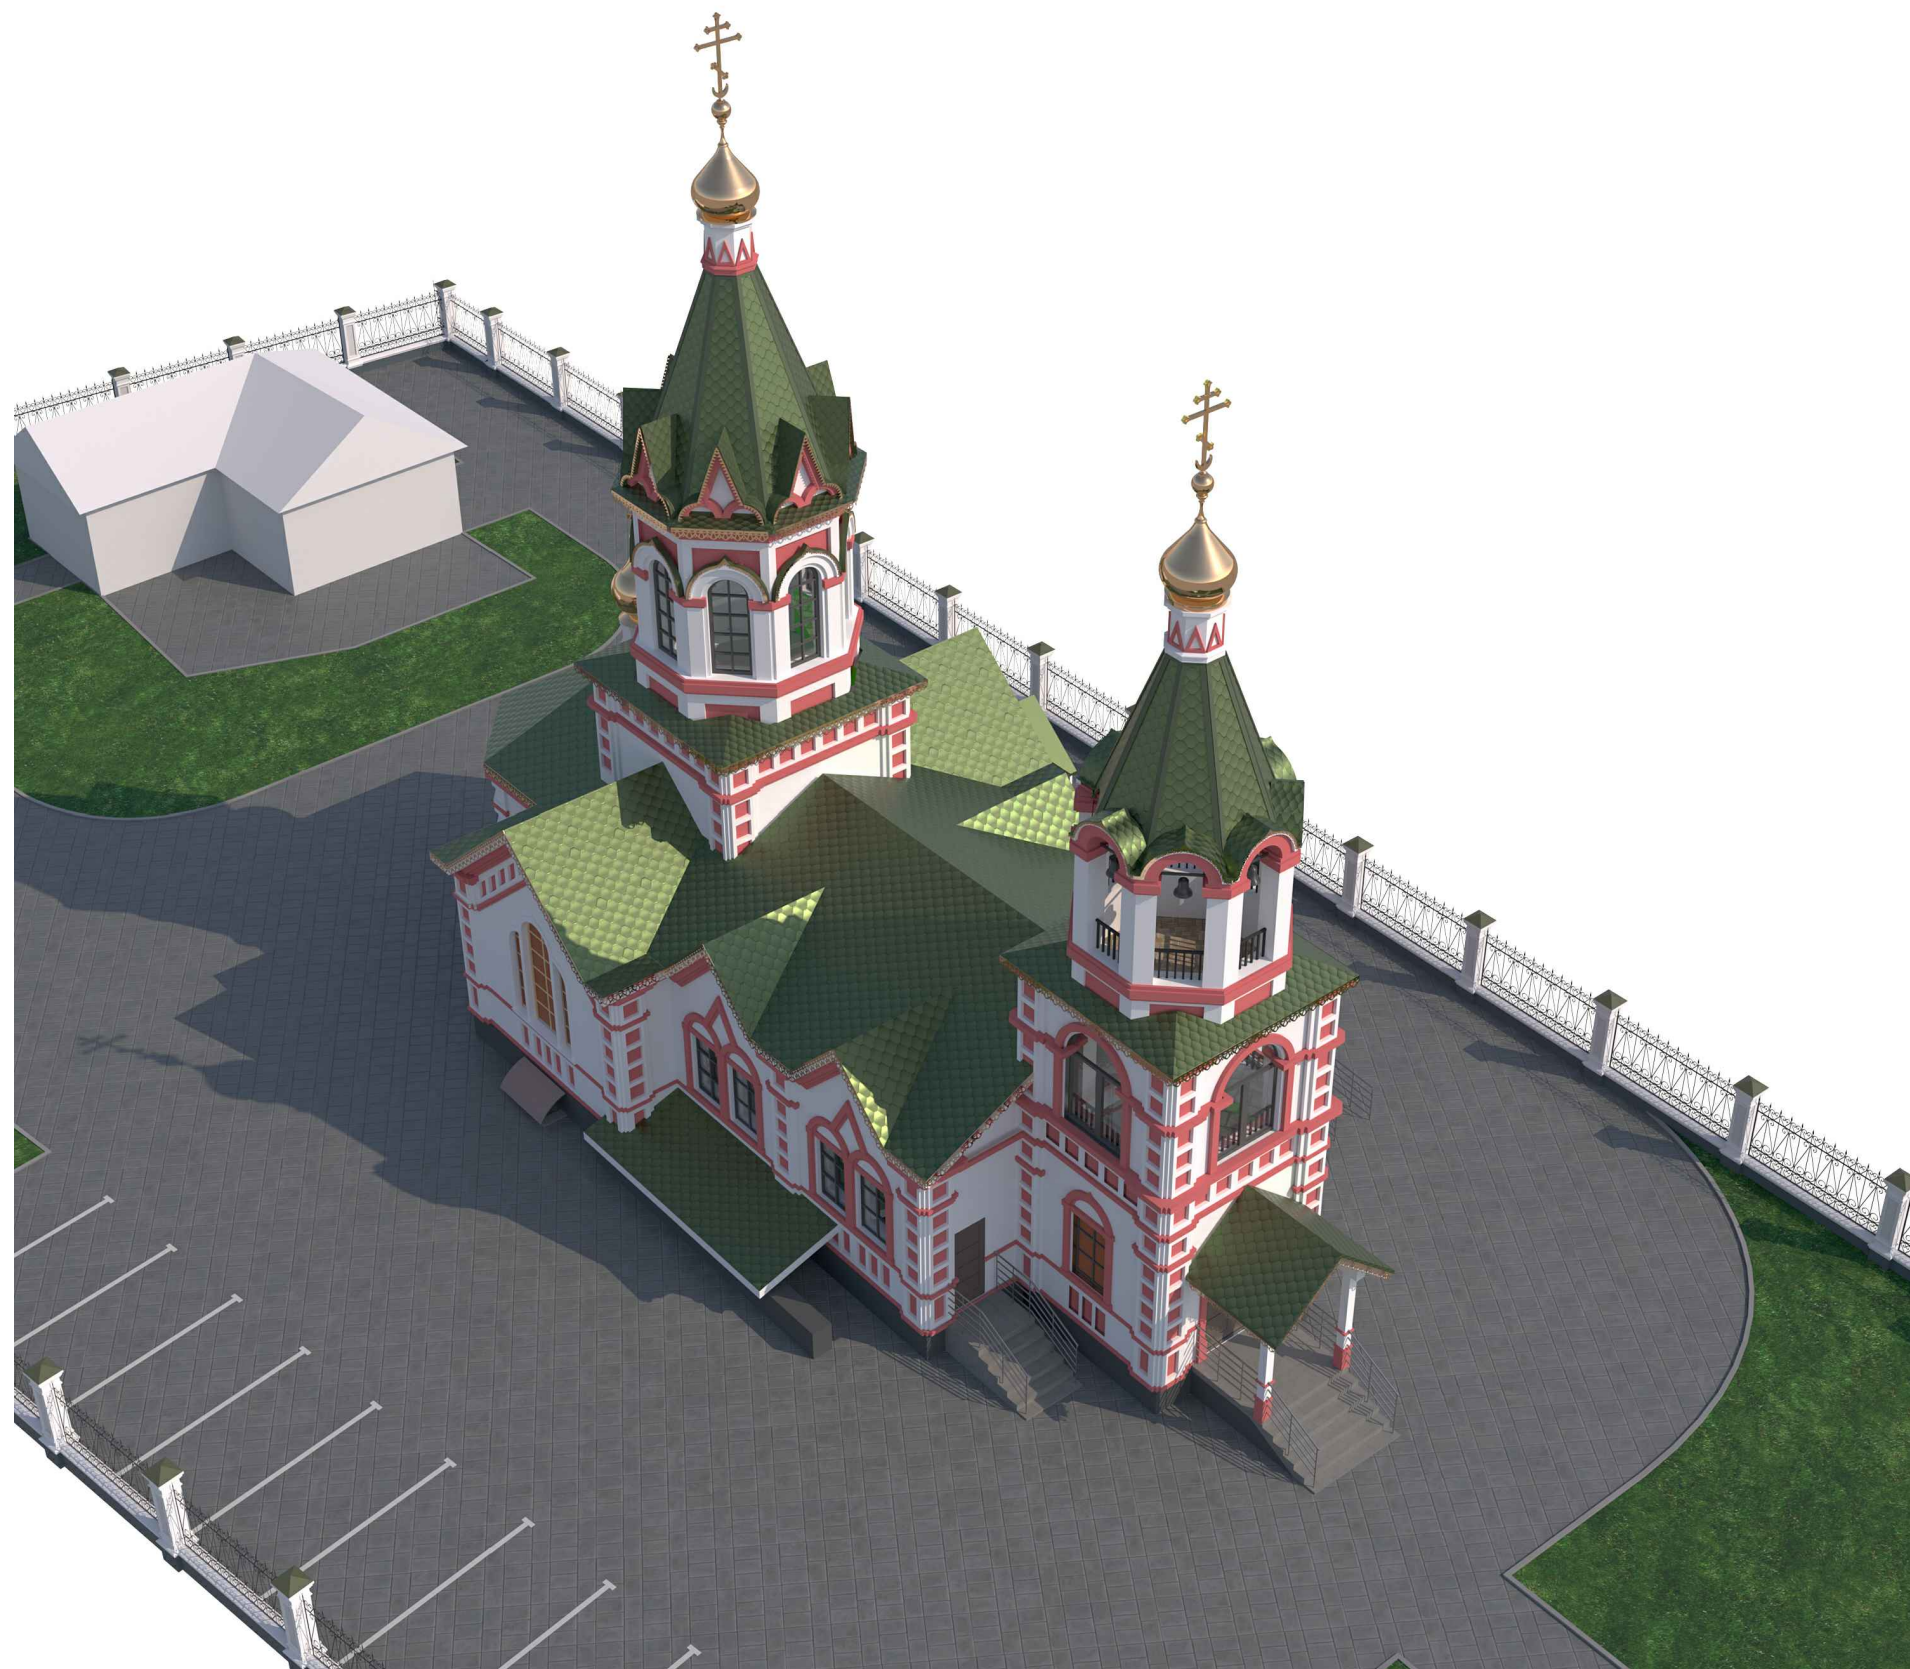


						0143.03.2023-АР			
						Храм Рождества Пресвятой Богородицы по адресу ул. Березовская рядом с профилакторием в Московском р-не г. Нижний Новгород			
Изм.	Кол.Уч	Лист	№док	Подпись	Дата				
Разработал		Иняев В.А.				Стадия		Лист	Листов
ГАП		Иняев А.А.				П		5	
Н.контр.		Иняев А.А.				Аксонометрия 2.		«ООО Творческая мастерская архитектора Иняева А.А.»	

Согласовано				
Иив. № подл.	Подп. и дата	Взам. инв. №		



Фасад М-А. М 1:100.

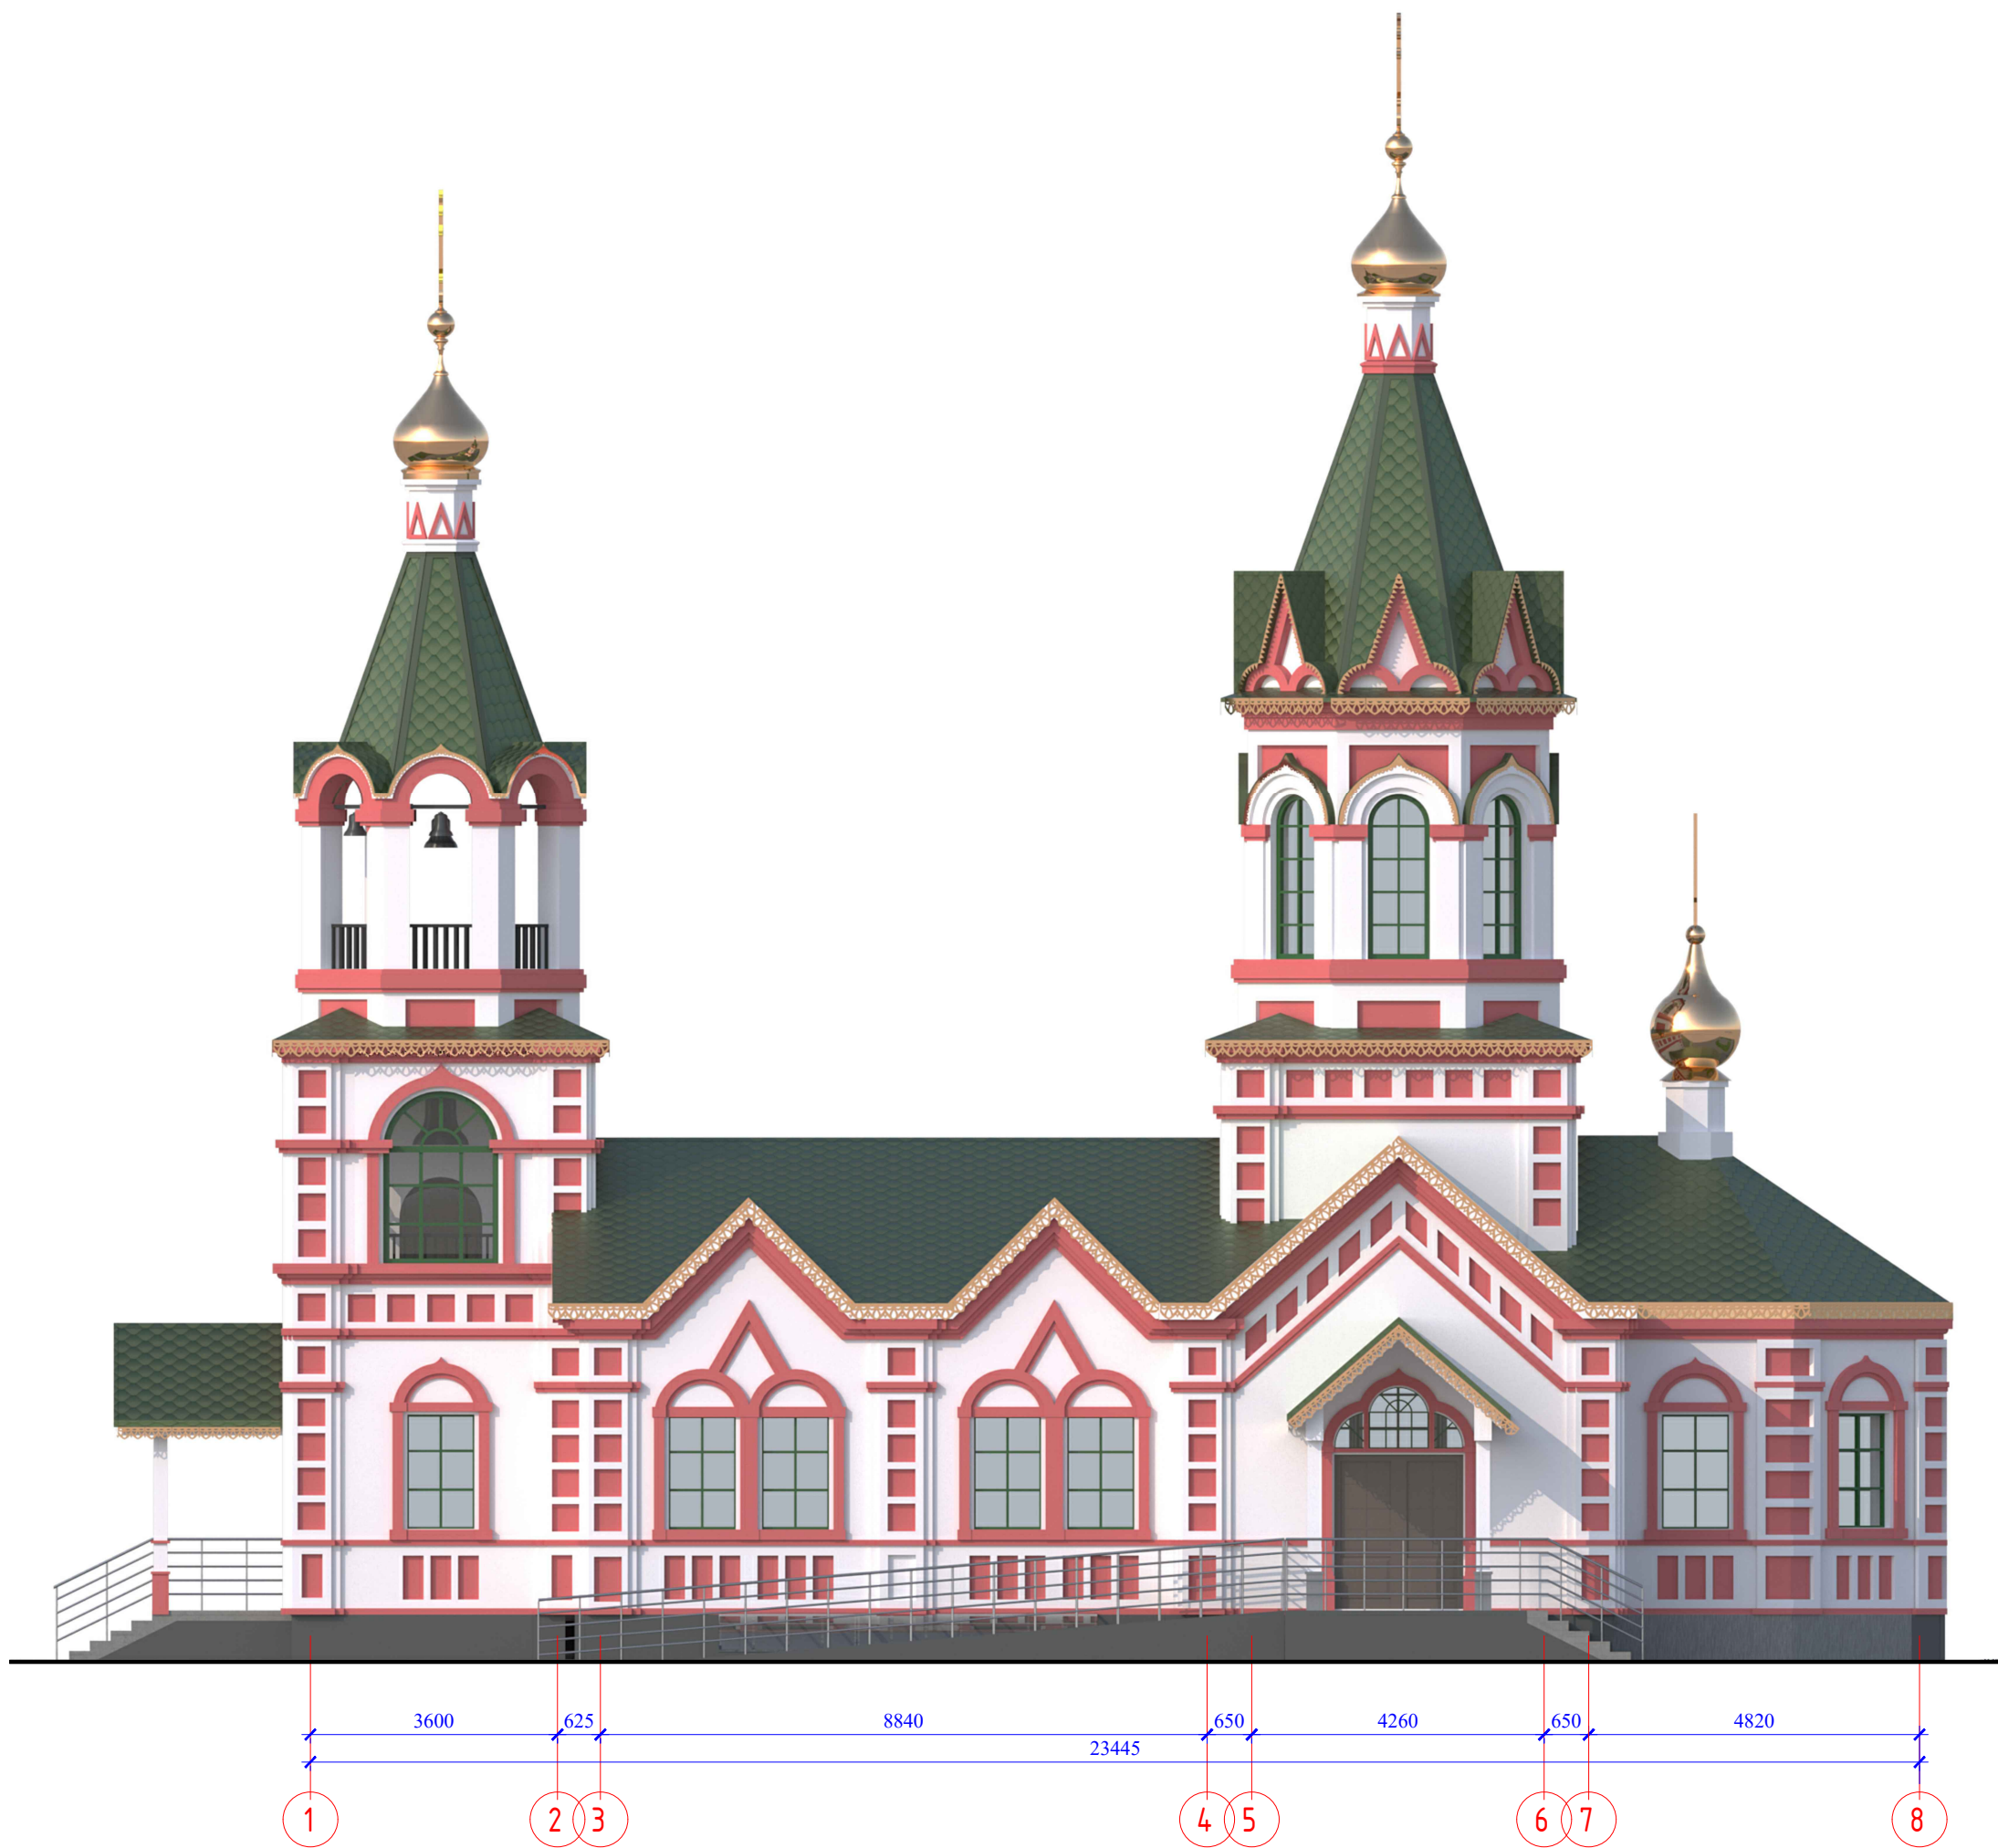

Фасад 1-8. М 1:100.

Отделка фасада :


- RAL - 3031
- RAL - 9010

						0143.03.2023-AP		
						Храм Рождества Пресвятой Богородицы по адресу ул. Березовская рядом с профилакторием в Московском р-не г. Нижний Новгород		
Изм.	Кол.Уч	Лист	№ док	Подпись	Дата		Стадия	Лист
Разработал	Иняев В.А.						П	6
ГАП	Иняев А.А.					Фасад М-А. Фасад 1-8. М 1:100. Цветовое решение. М 1:100.	«ООО Творческая мастерская архитектора Иняева А.А.»	
Н.контр.	Иняев А.А.							

Согласовано				
Иив. № подл.	Подп. и дата	Взам. инв. №		



Фасад А-М. М 1:100.

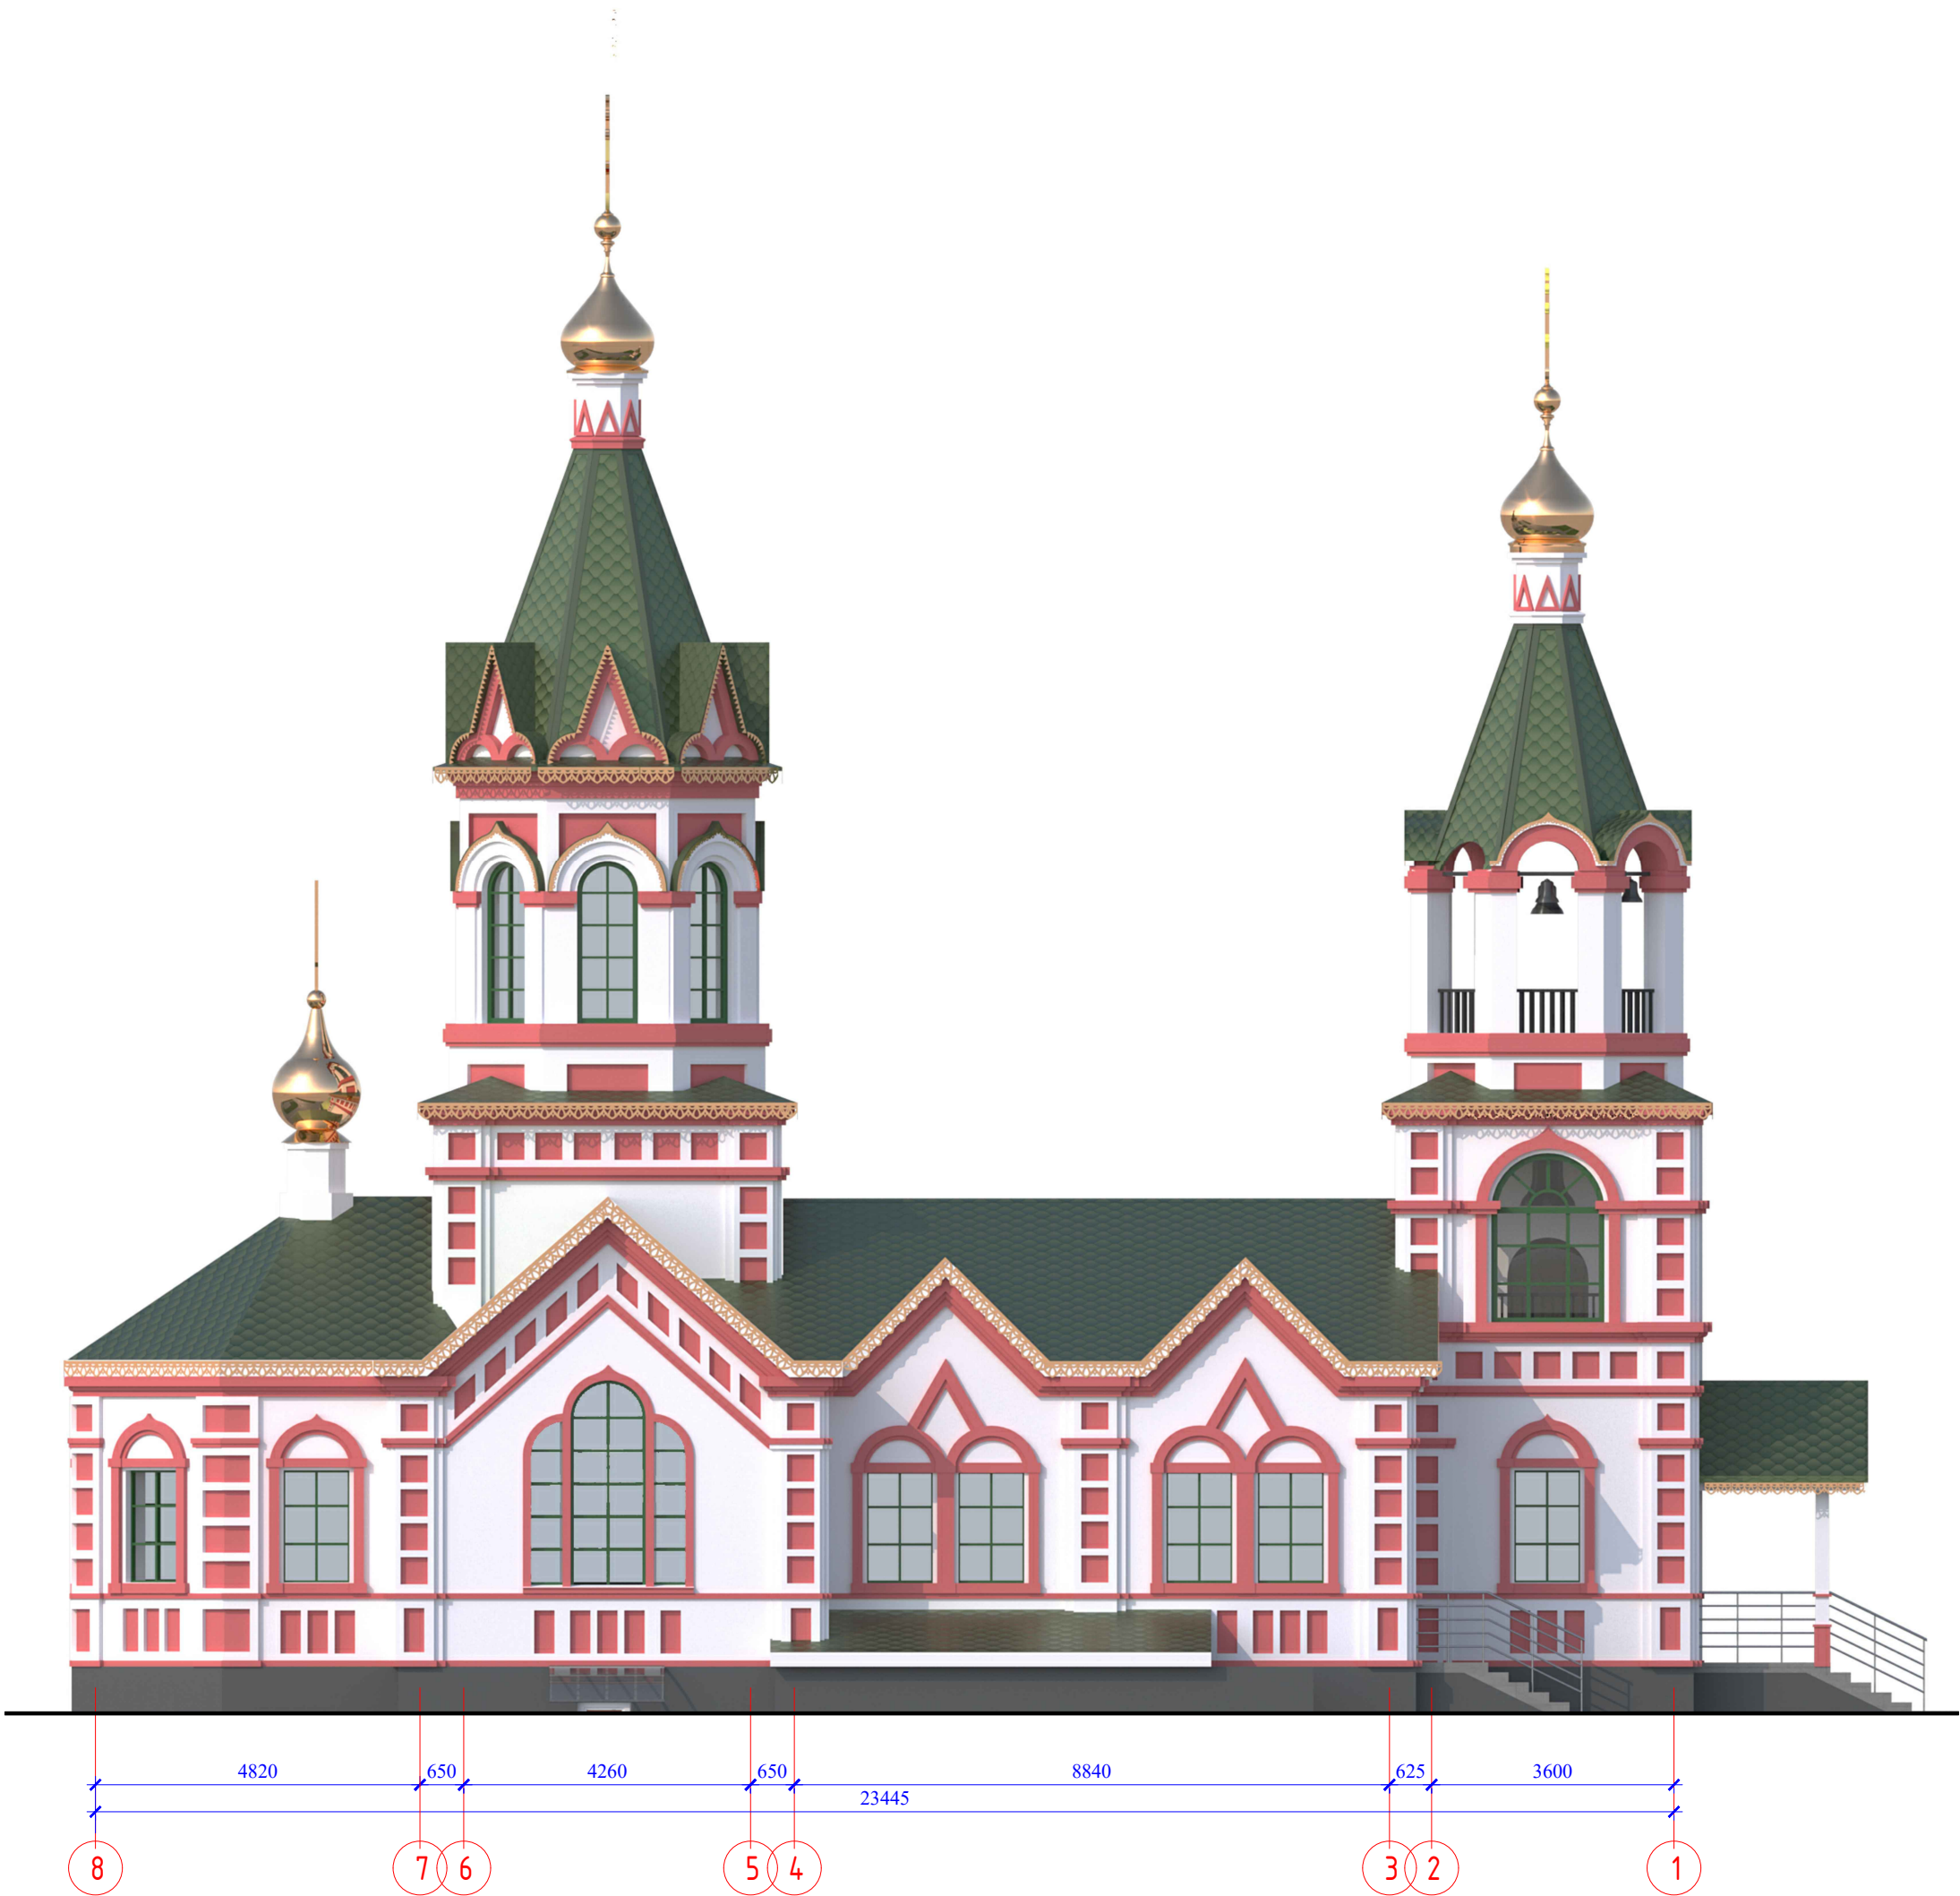


Фасад 8-1. М 1:100.

Отделка фасада :

- RAL - 3031
- RAL - 9010

						0143.03.2023-АР			
						Храм Рождества Пресвятой Богородицы по адресу ул. Березовская рядом с профилакторием в Московском р-не г. Нижний Новгород			
Изм.	Кол.Уч	Лист	№ док	Подпись	Дата		Стадия	Лист	Листов
Разработал	Иняев В.А.						П	7	
ГАП	Иняев А.А.						«ООО Творческая мастерская архитектора Иняева А.А.»		
						Фасад А-М. Фасад 8-1. М 1:100. Цветовое решение. М 1:100.			
Н.контр.	Иняев А.А.								

Экспликация помещений		
№ помещения	Наименование помещения	Площадь м2
1	Трапезная	69,25
2	Крестильня	15,40
3	Ризница	8,70
4	Провирия	11,20
5	Кухня	11,20
6	Санузел	9,90
7	Кабинет	7,34
8	Кабинет	6,90
9	Кабинет	7,30
10	Гардероб	4,63
Общая площадь помещений:		151,80

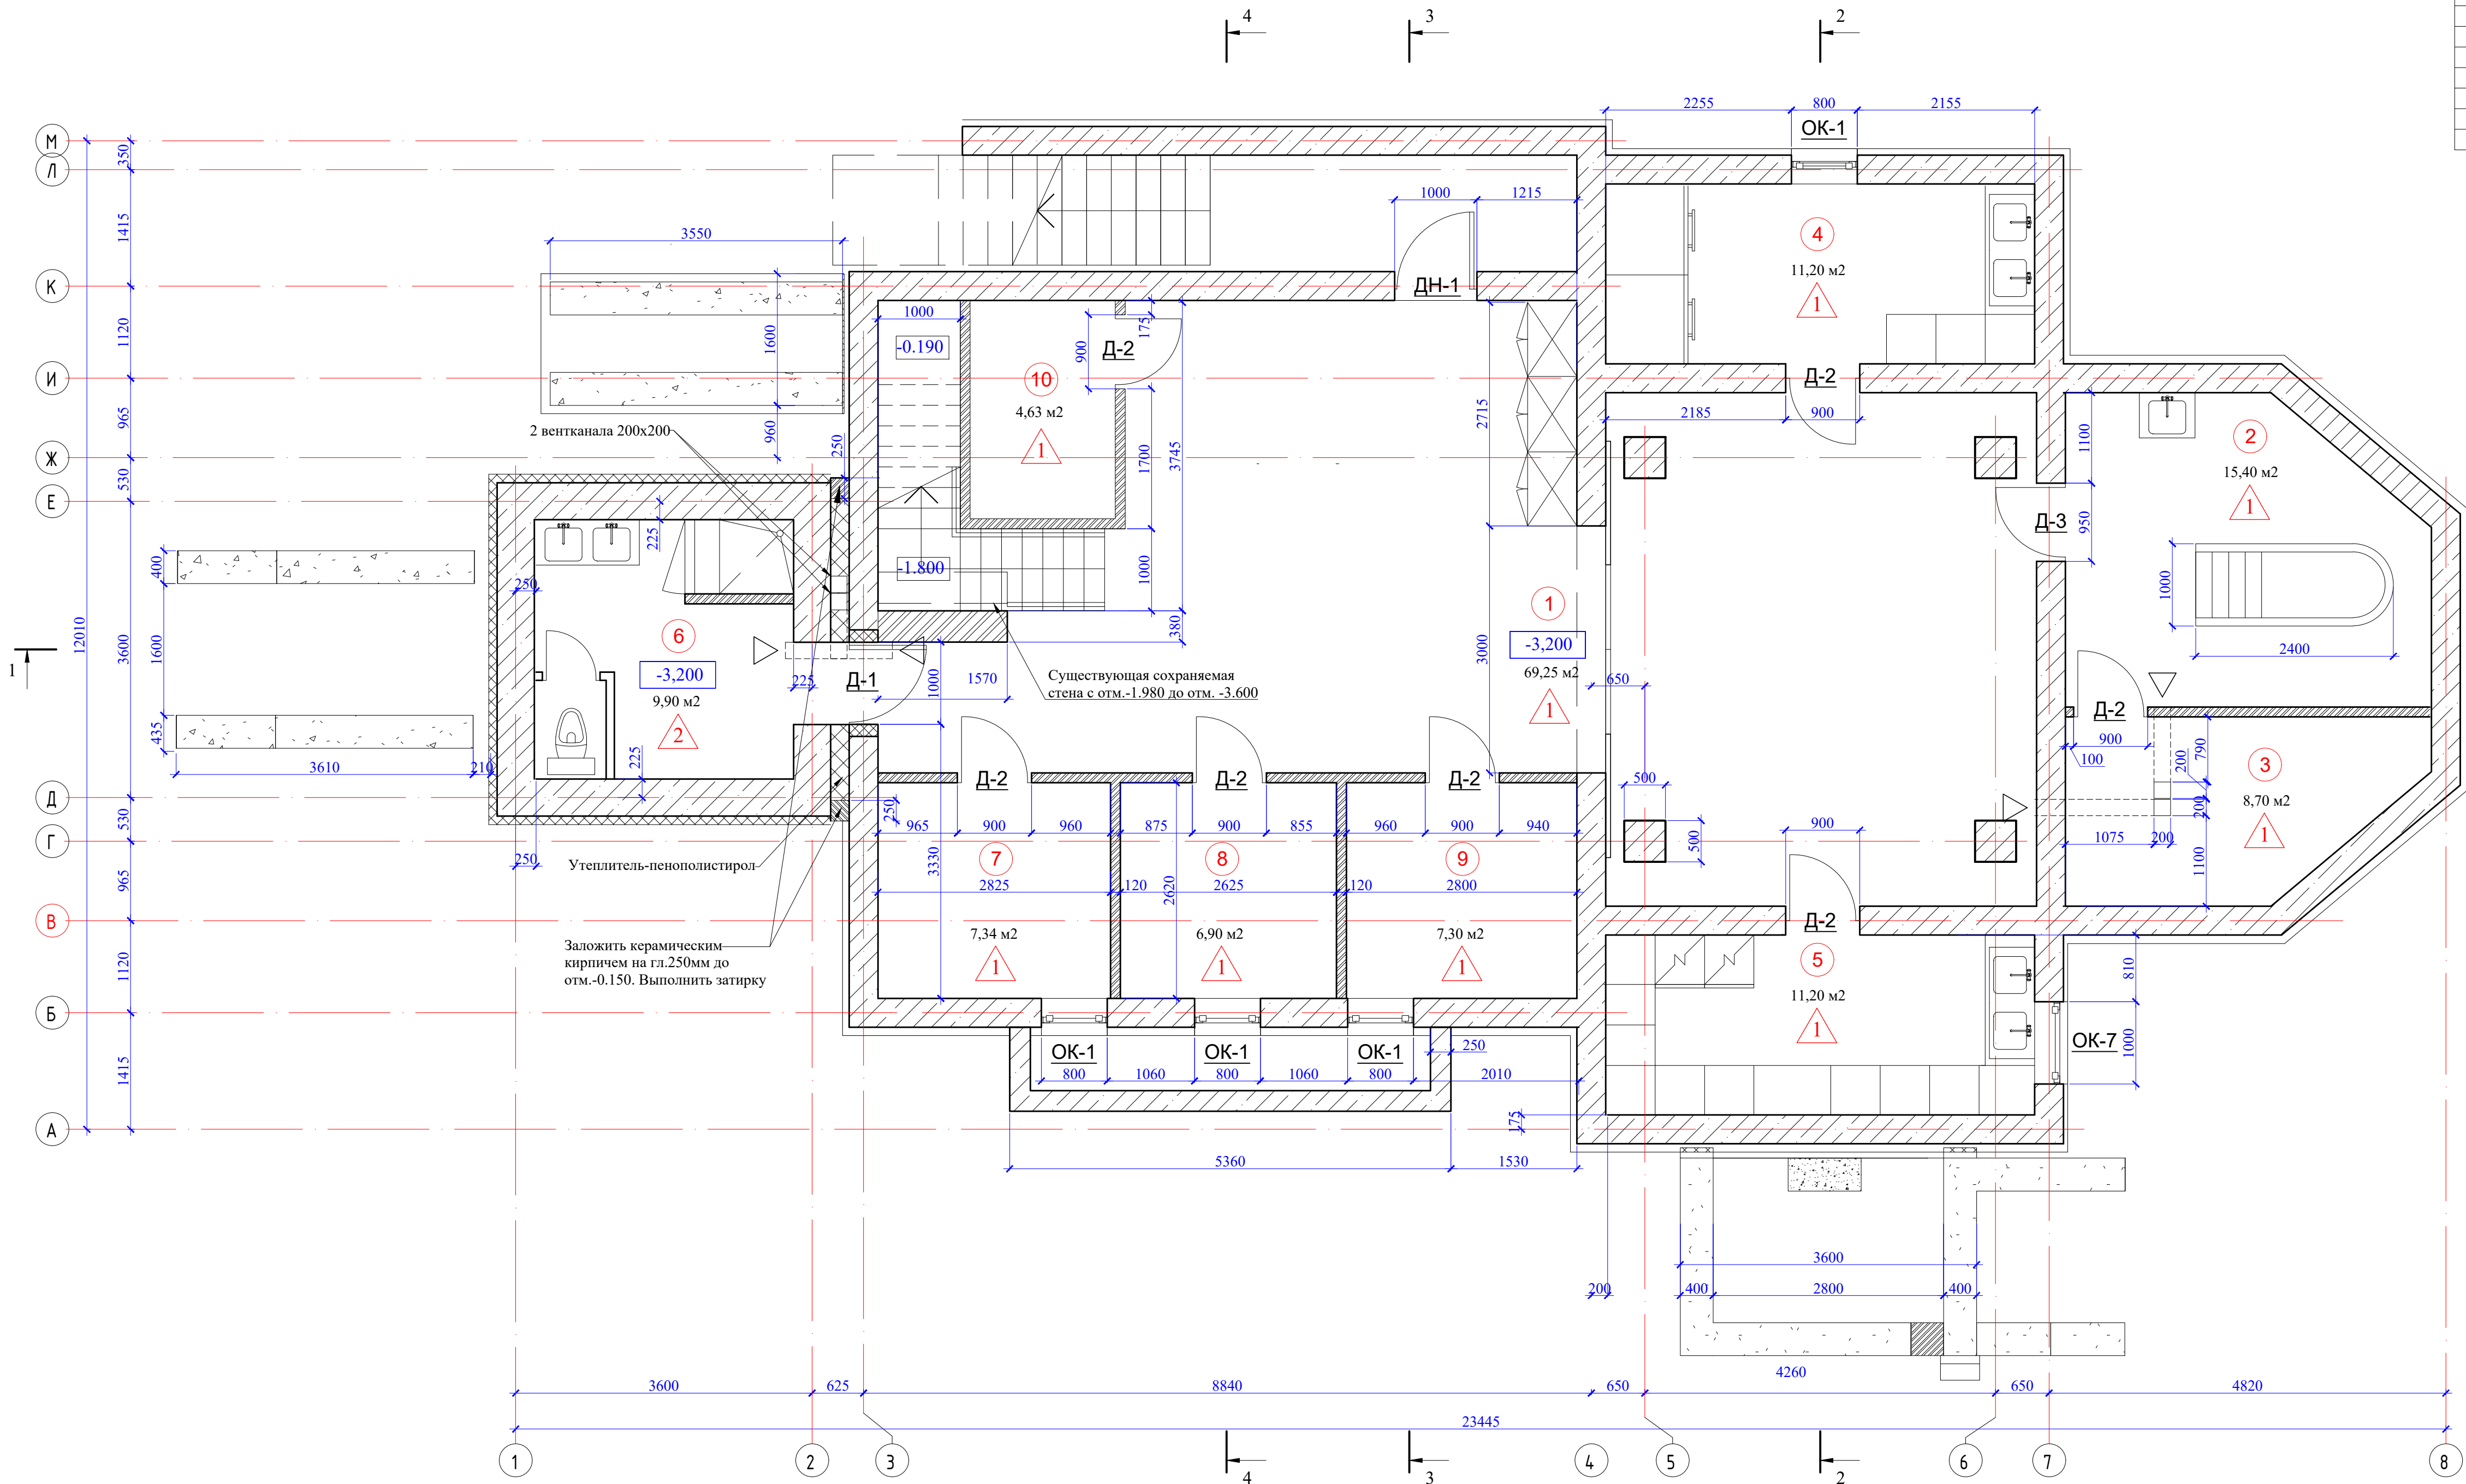

Условные обозначения :

- Ж/б стены и колонны

- Тип пола

96,80 м2 - Площадь помещения

- Отметка

- Марка двери

- Марка окна


Общие указания :

- относительная отметка 0,000 соответствует абсолютной отметке +79,970
- данный лист смотреть с разделом АР, инженерной и конструктивной частью проекта
- экспликацию полов и ведомость отделки помещений см. листы
- отделка стен - толстая штукатурка 2 см обетка известковым раствором под покраску
- спецификацию элементов заполнения проемов внутренних и наружных стен см. листы

						0143.03.2023-АР		
						Храм Рождества Пресвятой Богородицы по адресу ул. Березовская рядом с профилактрием в Московском р-не г. Нижний Новгород		
Изм.	Кол.	Лист	№ док.	Подпись	Дата	Стадия	Лист	Листов
Разработал	Иняев В.А.					П	8	
ГАП	Иняев А.А.							
						План подклета на отм.-3,200. М 1:50.		
Н.контр.	Иняев А.А.					«ООО Творческая мастерская архитектора Иняева А.А.»		


Формат А1

Экспликация помещений		
№ помещения	Наименование помещения	Площадь м2
1	Пригвор	7,70
2	Храм	96,80
3	Солея	23,30
4	Алтарь	31,00
Общая площадь помещений:		158,80

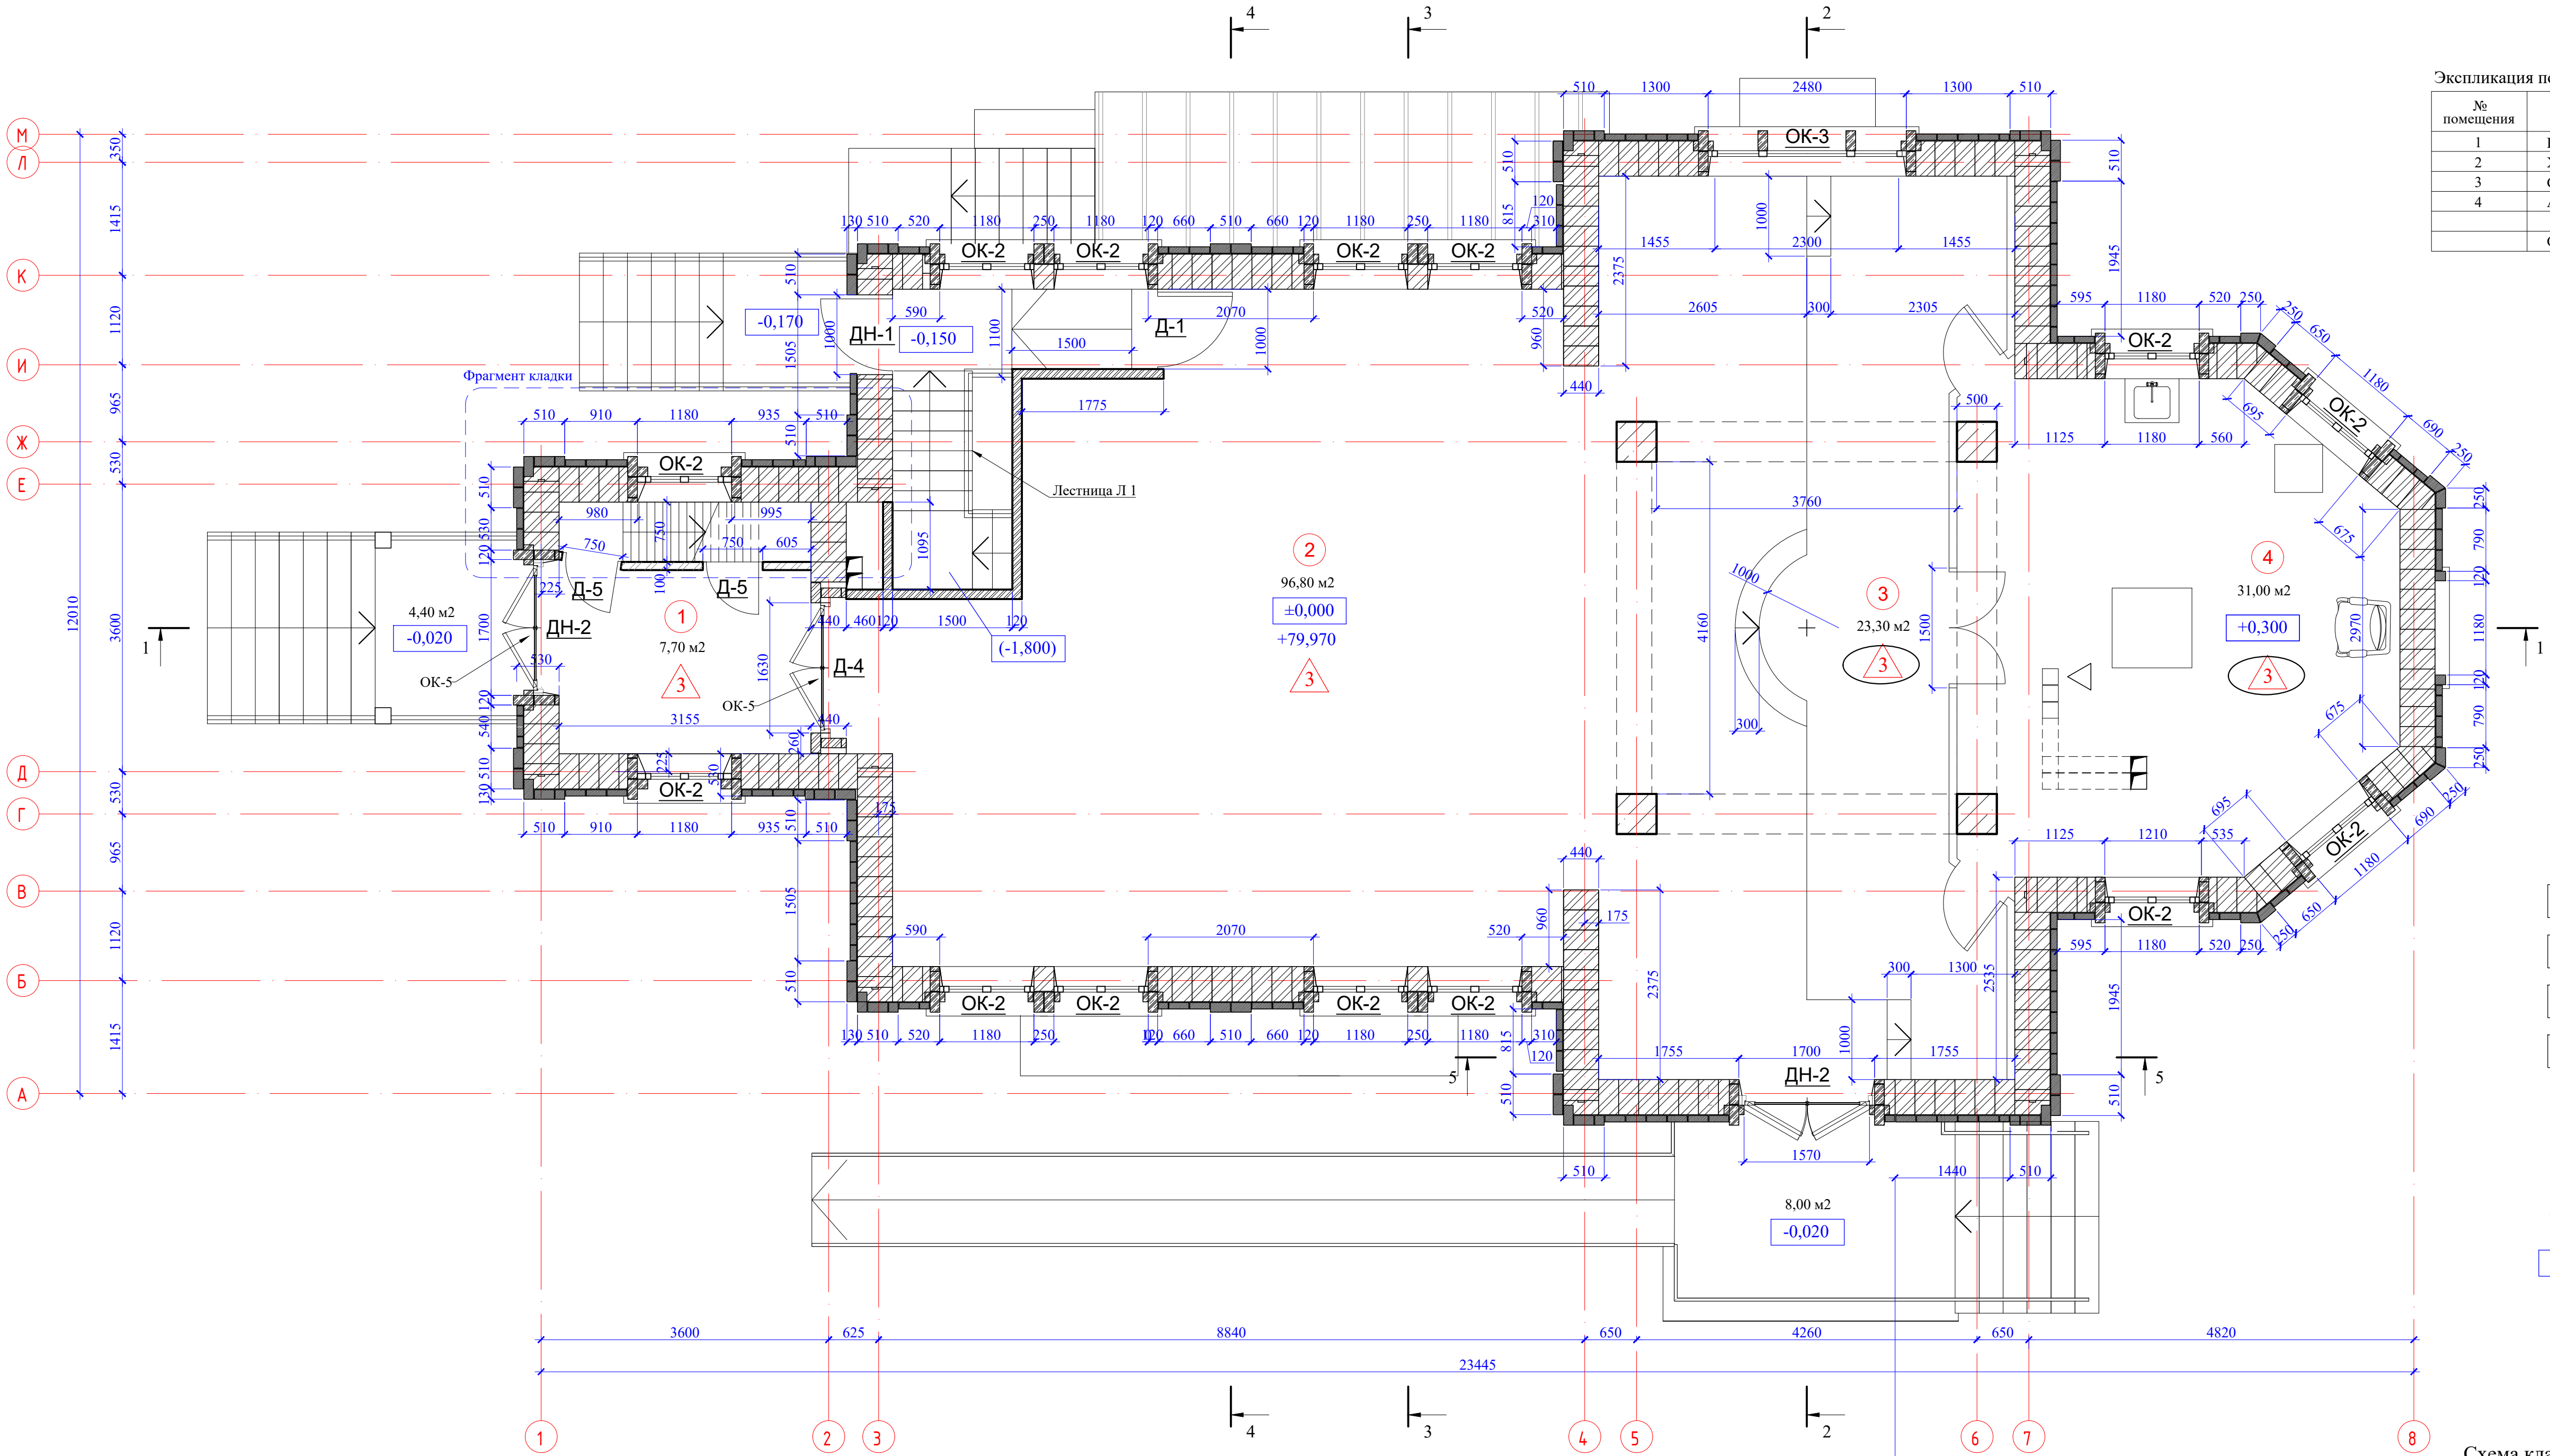

- Условные обозначения :
- Ж/б стены и колонны
 - Стены из керамических блоков "Porotherm" - 440мм
 - Ядринский кирпич полнотелый - 250x120x65 мм
 - Облицовка - кирпич керамическийлицевой «ЕВРО» - 250x85x65 мм
 - Керамический пустотелый кирпич КОолПу — 250x120x65 мм
 - Тип пола
 - Площадь помещения
 - Отметка
 - Марка двери
 - Марка окна

Схема кладки Parotherm 44

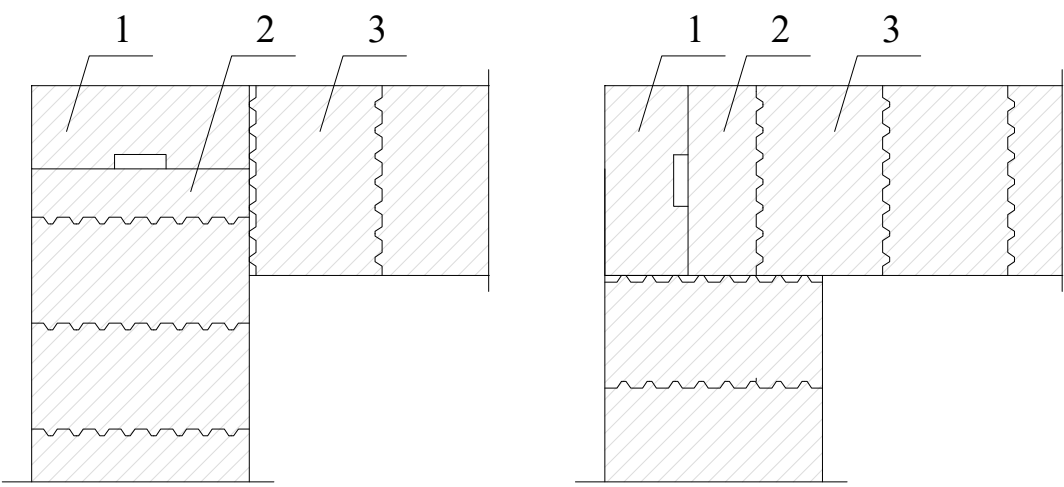



- 1 - Parotherm 44R (180x440x219 мм)
2 - Parotherm 44 1/2 (125x440x219 мм)
3 - Parotherm 44 (250x440x219 мм)

- Общие указания :
- относительная отметка 0,000 соответствует абсолютной отметке +79,970
 - данный лист смотреть с разделом АР, инженерной и конструктивной частью проекта
 - экспликацию полов и ведомость отделки помещений см. листы
 - отделка стен - толстая штукатурка 2 см обетка известковым раствором под покраску
 - спецификацию элементов заполнения проемов внутренних и наружных стен см. листы

0143.03.2023-АР				
Храм Рождества Пресвятой Богородицы по адресу ул. Березовская рядом с профилактрием в Московском р-не г. Нижний Новгород				
Изм.	Кол.Уч.	Лист	Модок	Подпись
Разработал	Иняев В.А.			
ГАП	Иняев А.А.			
П			Лист	Листов
			9	
План 1-го этажа на отм.±0,000. М 1:50.			«ООО Творческая мастерская архитектора Иняева А.А.»	
Н.контр.	Иняев А.А.			


Фрагмент кладки. 1-й ряд.

Фрагмент кладки. 2-й ряд.

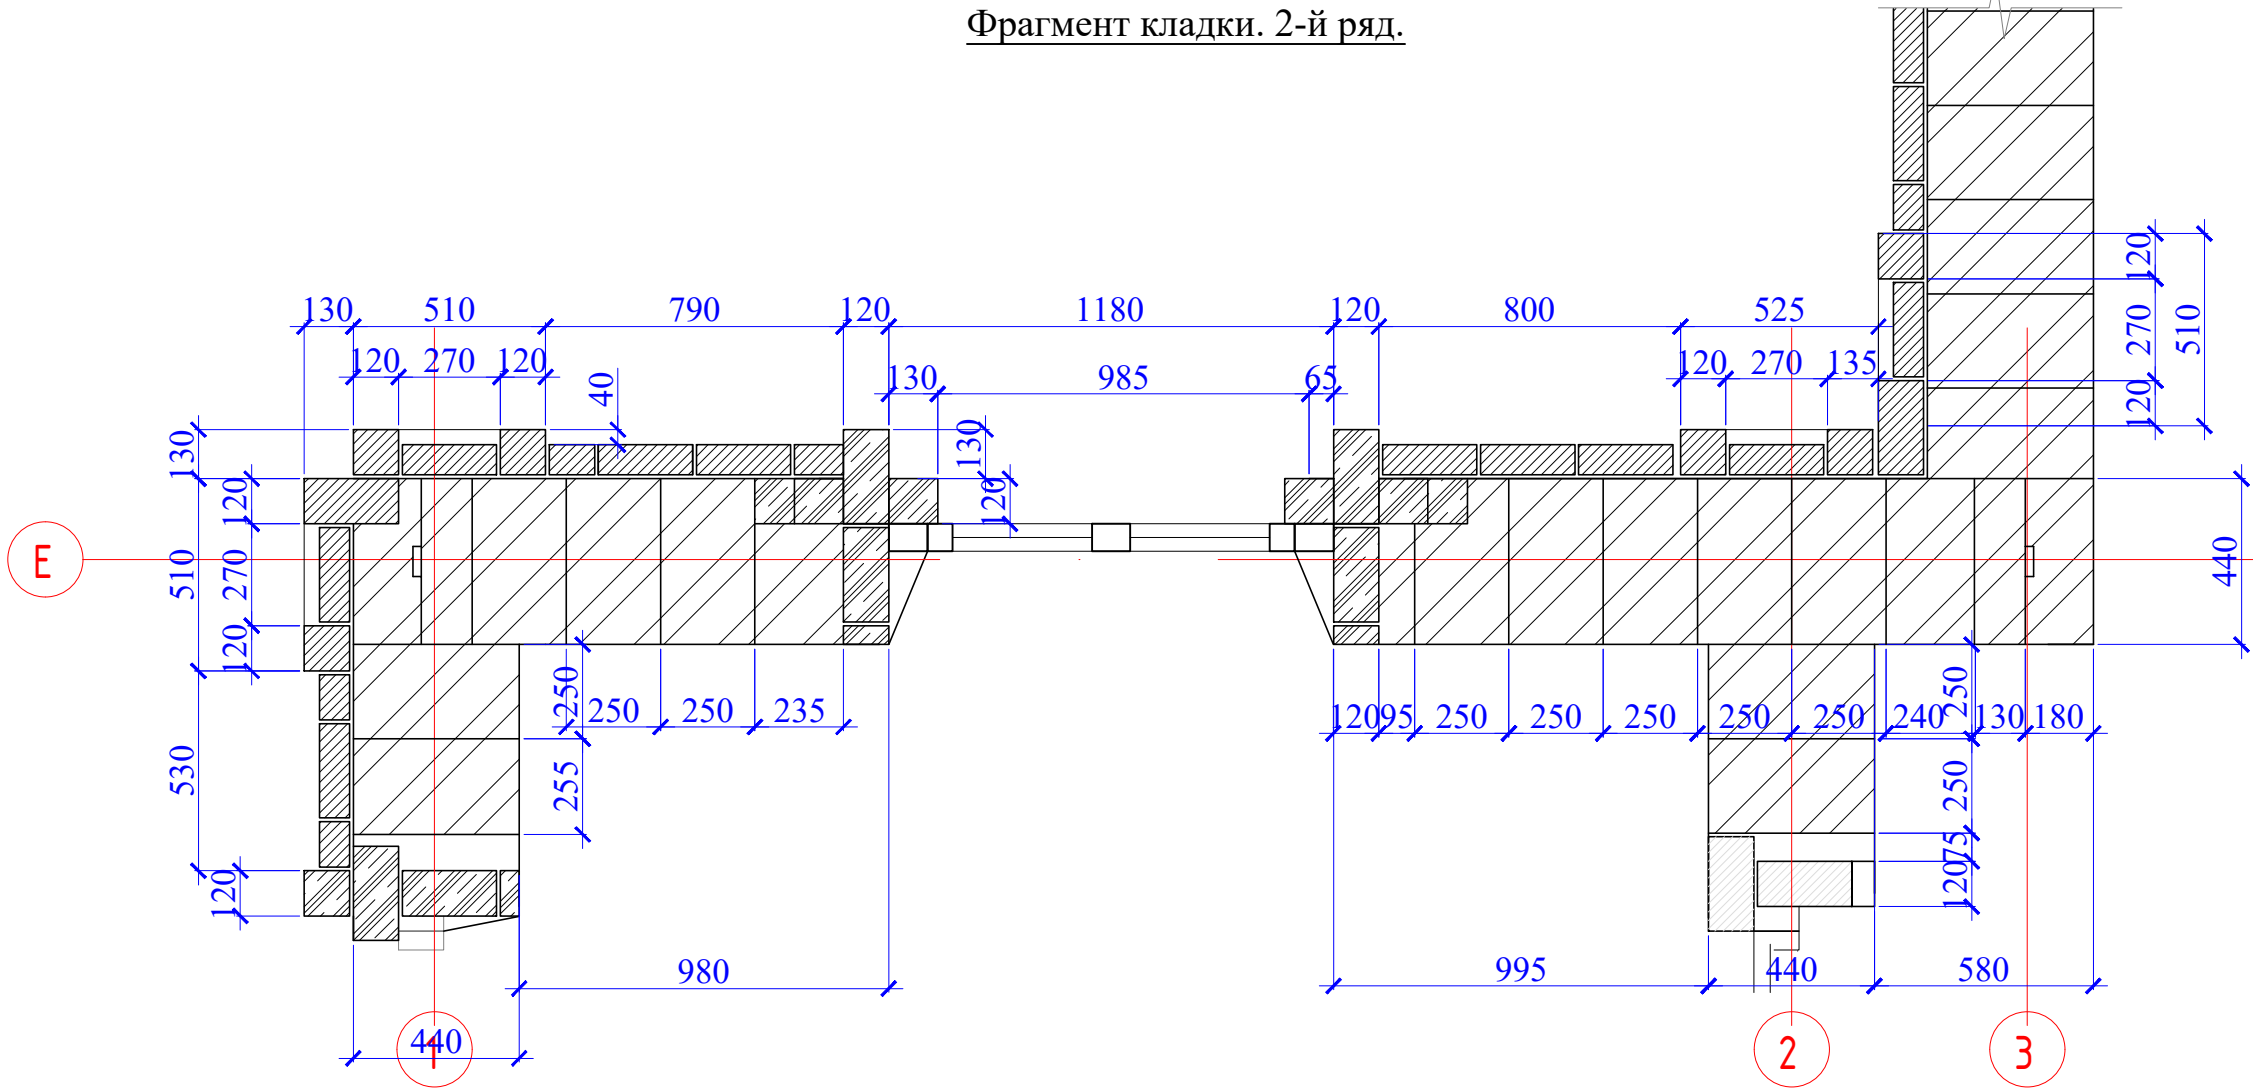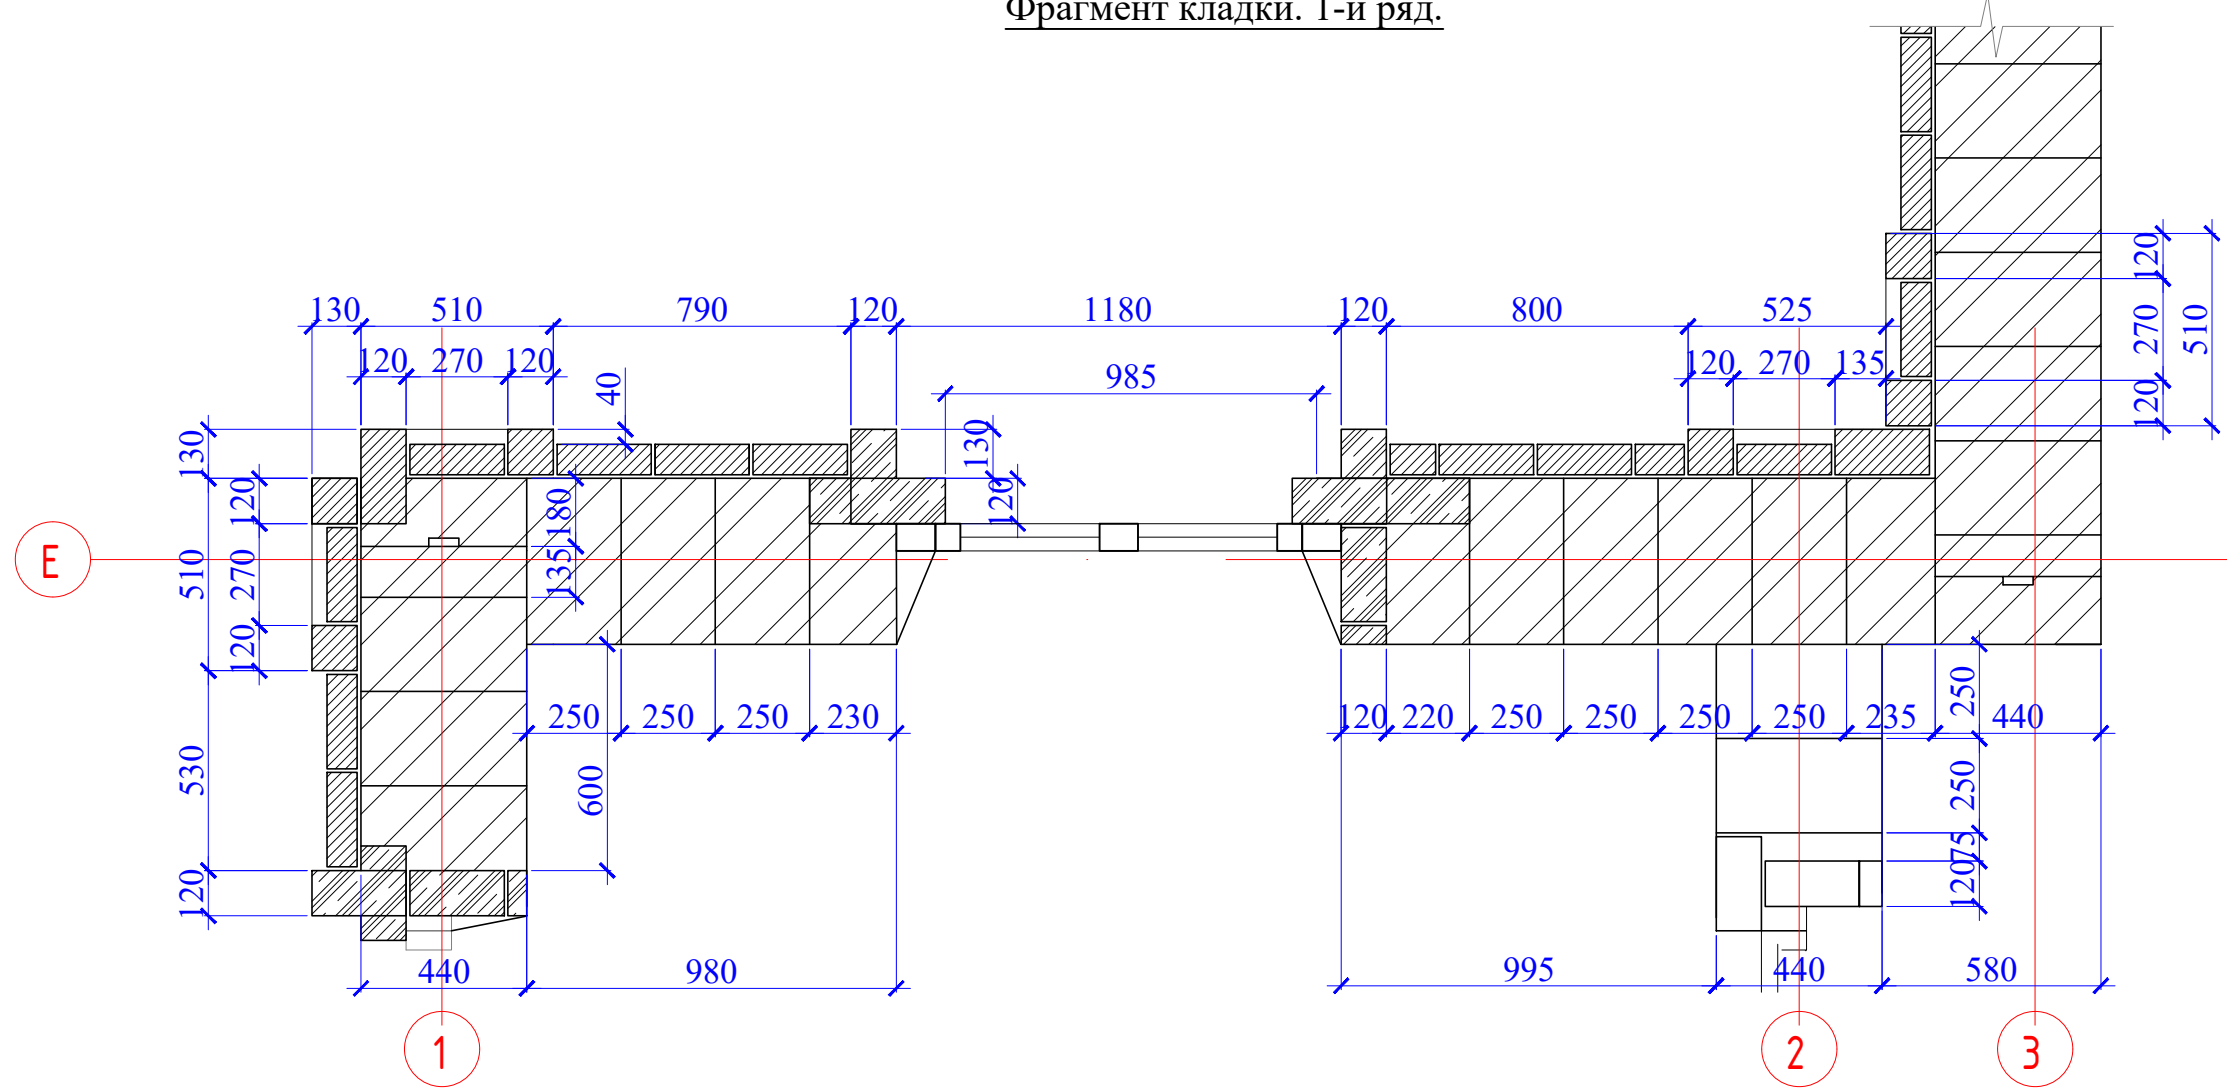

Согласовано					
Имя № подл.	Подп. и дата	Взам. инв. №			

Экспликация помещений		
№ помещения	Наименование помещения	Площадь м2
1	Помещение для газопользующего оборудования	10,00
2	Чердачное помещение	15,60
Общая площадь помещений:		25,60

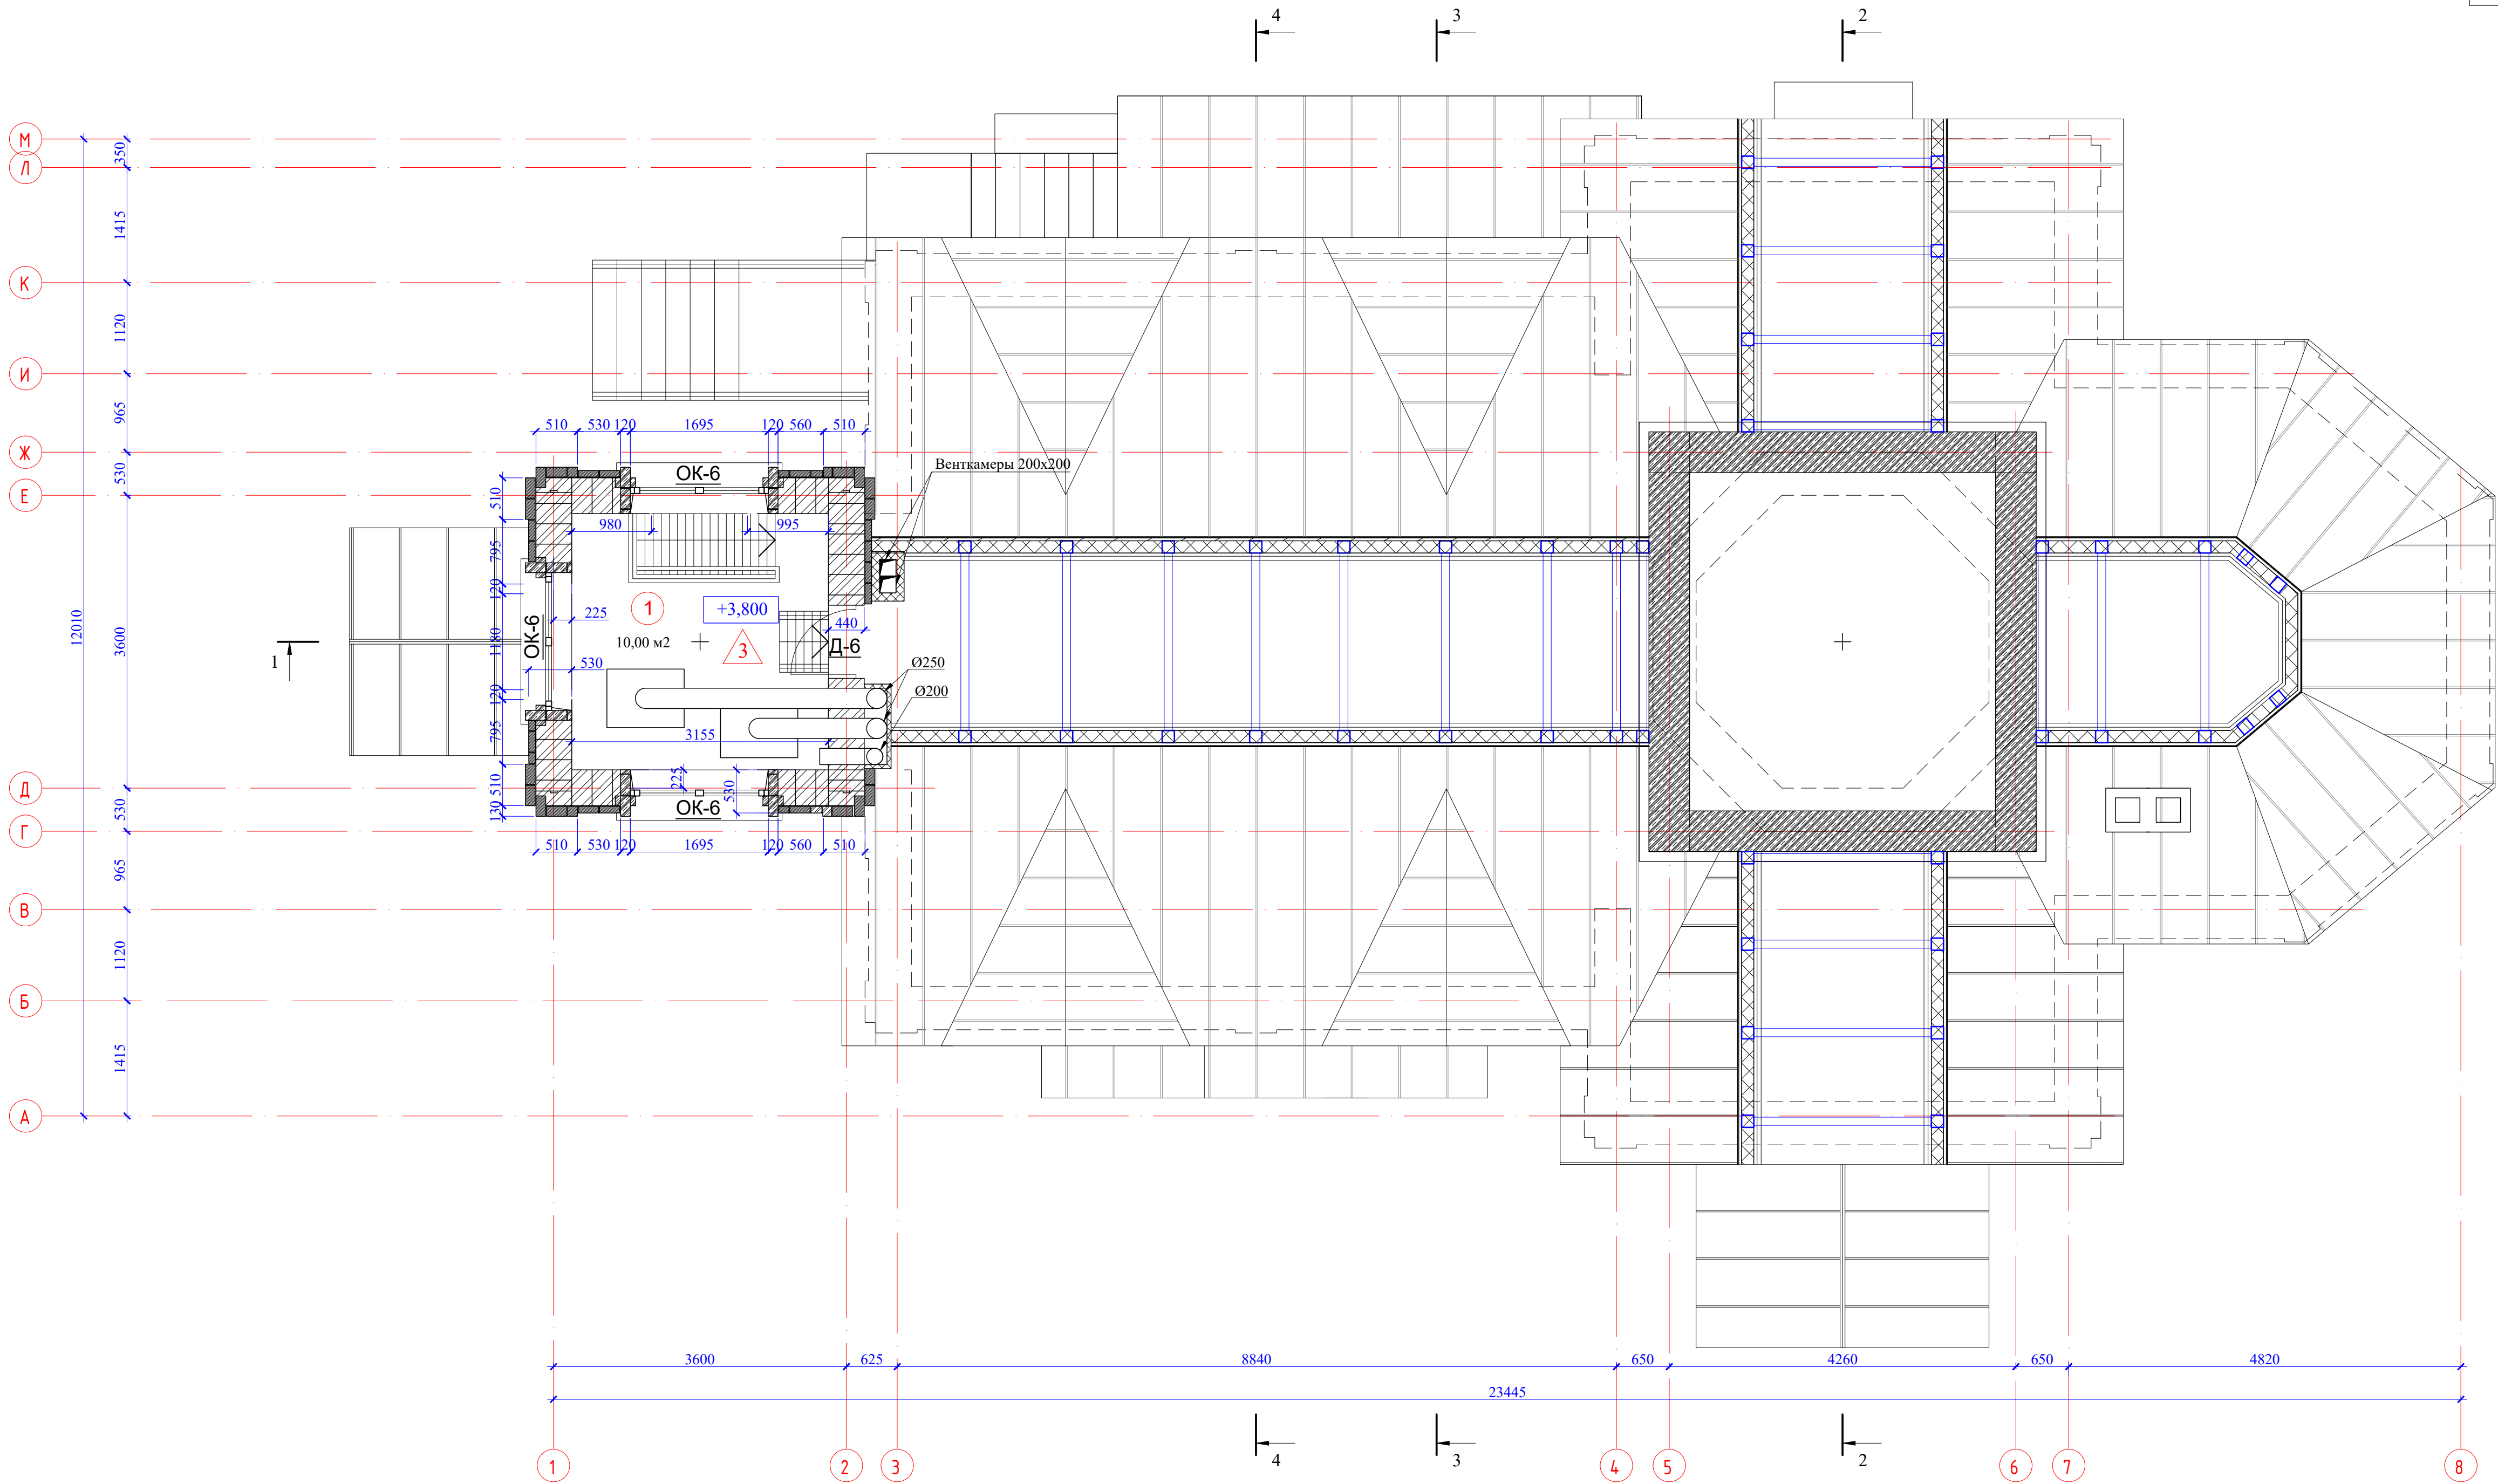


Условные обозначения :

- Ж/б стены и колонны
- Стены из керамических блоков "Porotherm" - 440мм
- Ядринский кирпич полнотелый - 250x120x65 мм
- Облицовка - кирпич керамическийлицевой «ЕВРО» - 250x85x65 мм
- Керамический пустотелый кирпич КОЛПу — 250x120x65 мм
- Тип пола
- Площадь помещения
- Отметка
- Марка двери
- Марка окна

Общие указания :

- относительная отметка 0,000 соответствует абсолютной отметке +79,970
- данный лист смотреть с разделом АР, инженерной и конструктивной частью проекта
- экспликацию полов и ведомость отделки помещений см. листы
- отделка стен - толстая штукатурка 2 см обетка известковым раствором под покраску
- спецификацию элементов заполнения проемов внутренних и наружных стен см. листы

						0143.03.2023-АР			
						Храм Рождества Пресвятой Богородицы по адресу ул. Березовская рядом с профилакторием в Московском р-не г. Нижний Новгород			
Изм.	Кол.Уч.	Лист	№док.	Подпись	Дата		Стадия	Лист	Листов
Разработал	Иняев В.А.						п	10	
ГАП	Иняев А.А.								
Н.контр.	Иняев А.А.					План колокольной на отм.+5,900. М 1:50.	«ООО Творческая мастерская архитектора Иняева А.А.»		

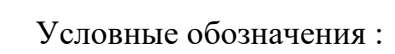


- | | | | | | | | | |
|------------|----------|------------|--------|---|------|---|---|--------|
| | | | | | | 0143.03.2023-АР | | |
| | | | | | | Храм Рождества Пресвятой Богородицы по адресу ул. Березовская рядом с профилакторием в Московском р-не г. Нижний Новгород | | |
| Изм. | Кол. Ул. | Лист | № док. | Подпись | Дата | | | |
| Разработал | | Иняев В.А. | |  | | Стадия | Лист | Листов |
| ГАП | | Иняев А.А. | |  | | П | 11 | |
| | | | | | | План колокольни и план главного восьмерика на отм. +9,300. М1:50. | «ООО Творческая мастерская архитектора Иняева А.А.» | |
| Н.контр. | | Иняев А.А. | |  | | | | |


Согласовано					
Имя, № подл.	Подп. и дата	Взам. инв. №			

							0143.03.2023-АР
							Храм Рождества Пресвятой Богородицы по адресу ул. Березовская рядом с профилакторием в Московском р-не г. Нижний Новгород
Изм.	Кол.Уч	Лист	Ведом.	Подпись	Дата		Стация
Разработал	Иняев В.А.						Лист
ГАП	Иняев А.А.						Листов
							П
							12
Н.контр.	Иняев А.А.						«ООО Творческая мастерская архитектора Иняева А.А.»


Формат А

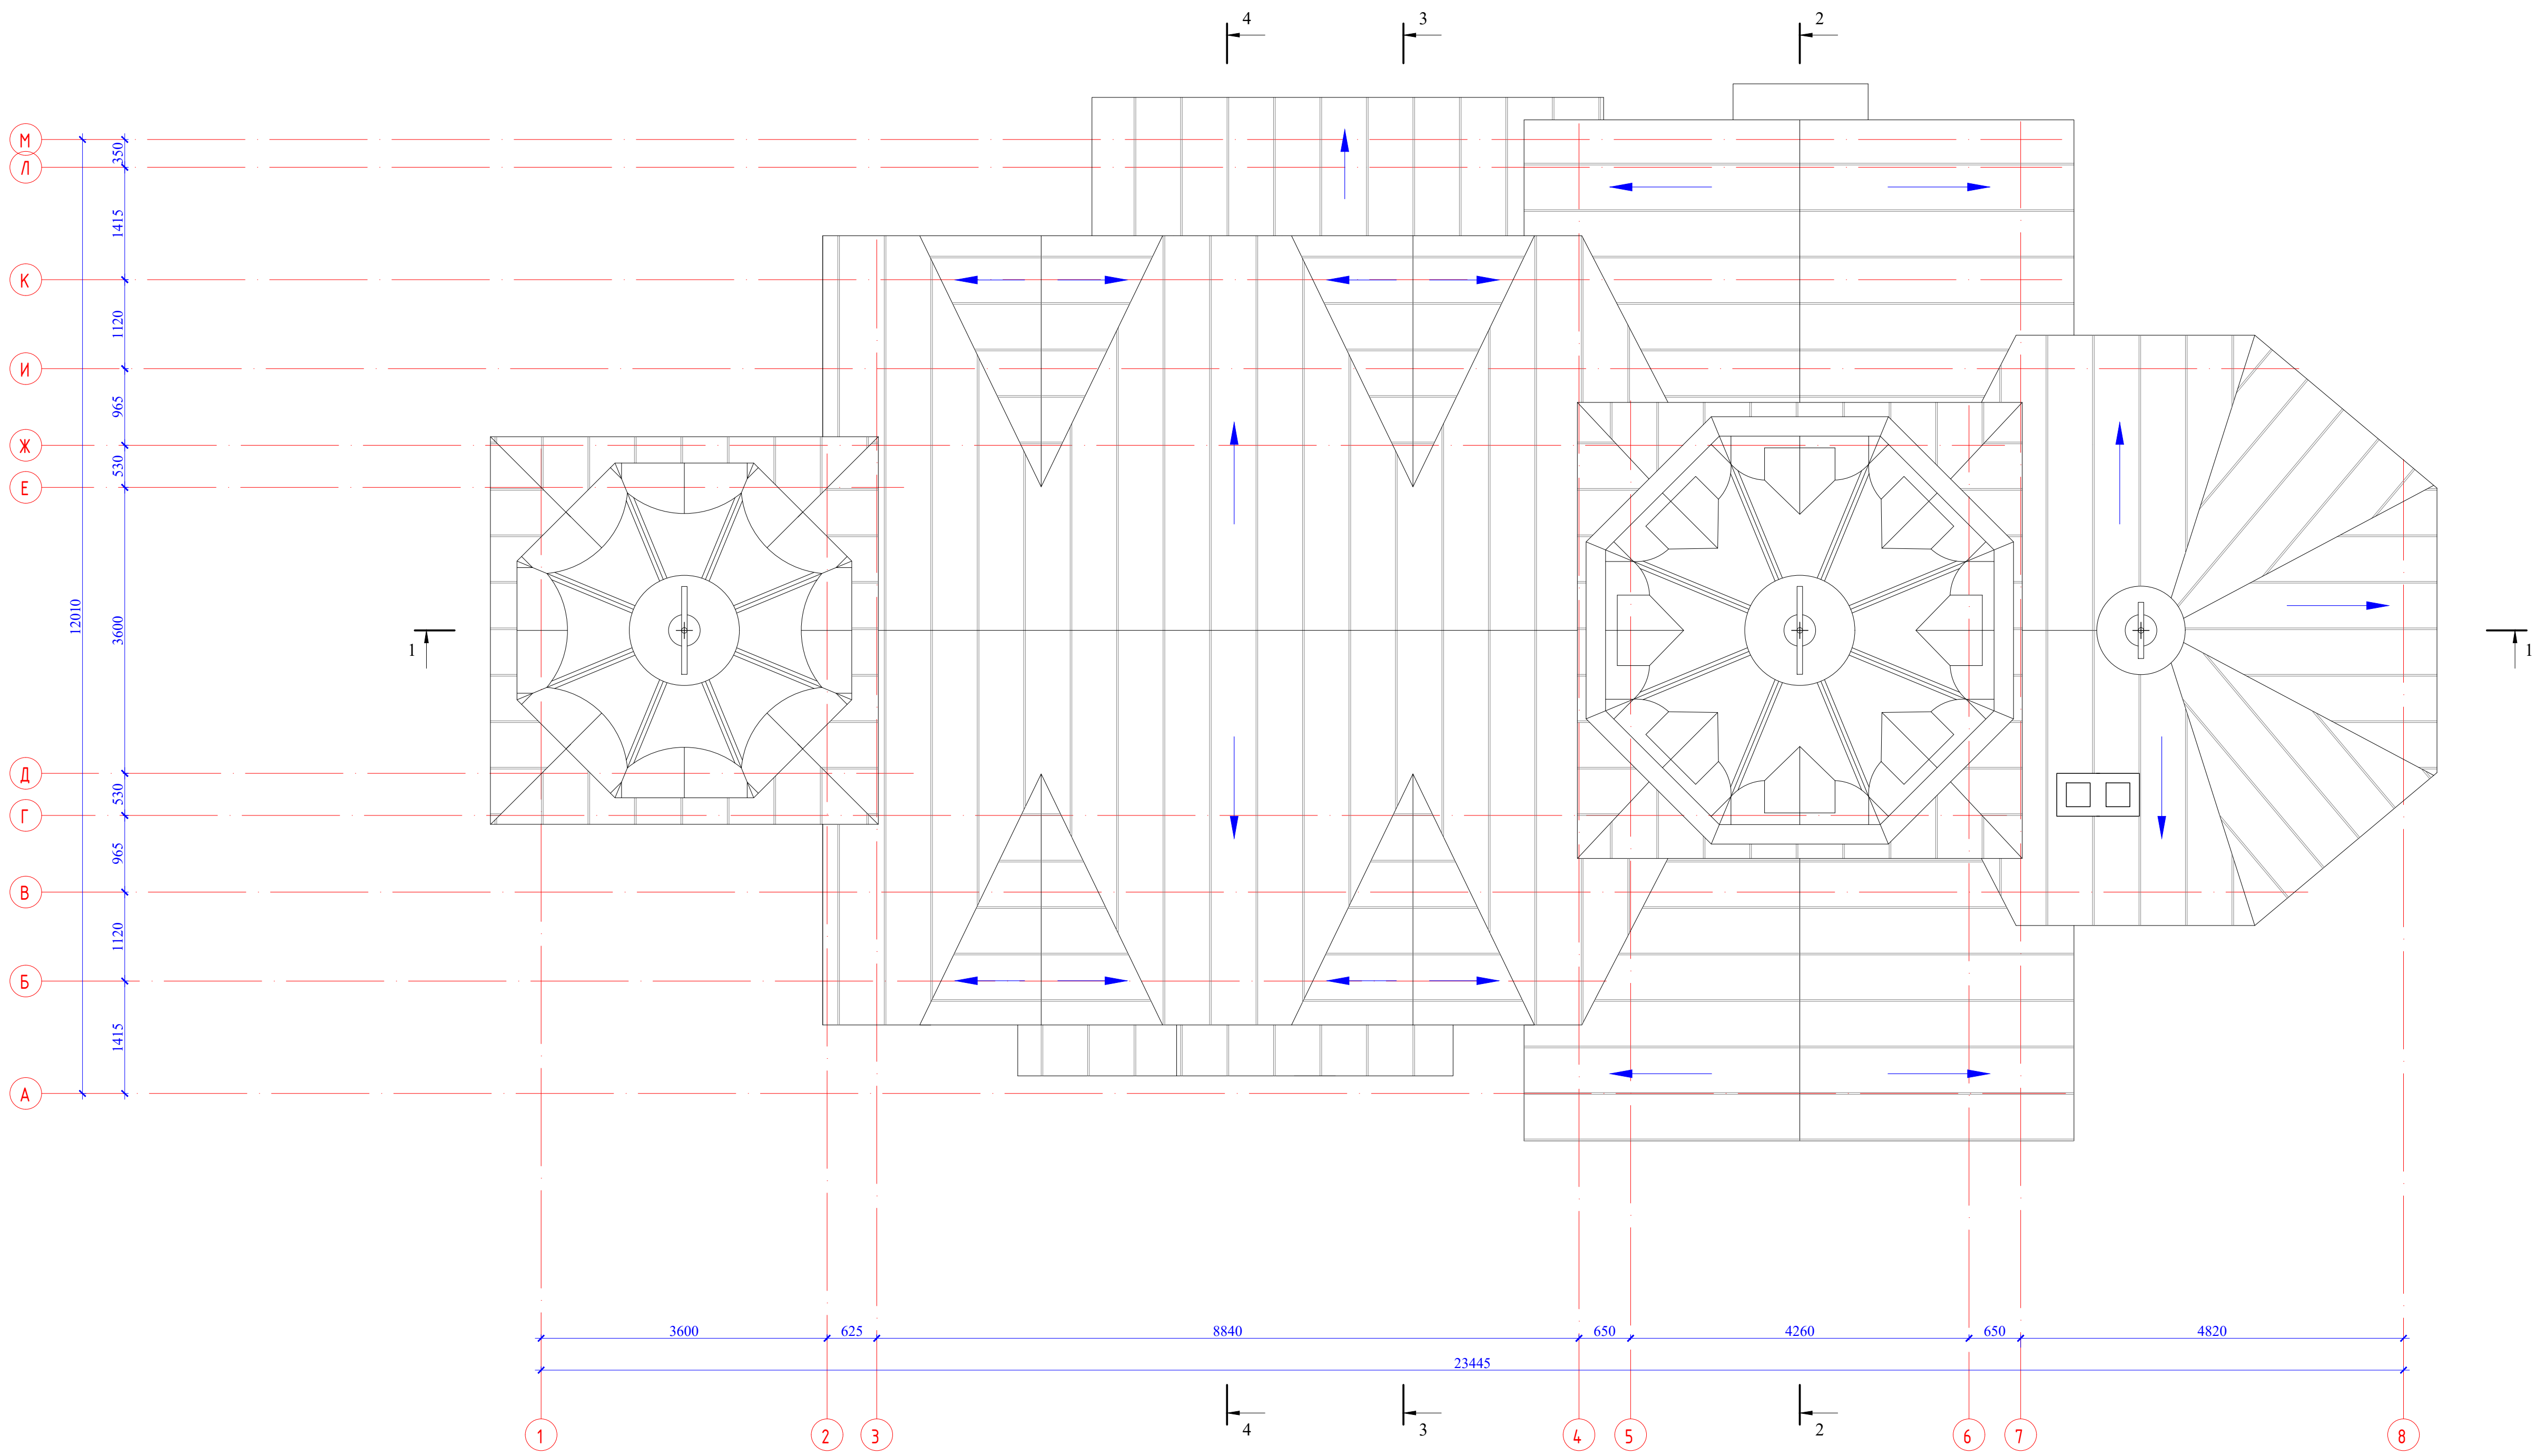

Разрез 1-1.

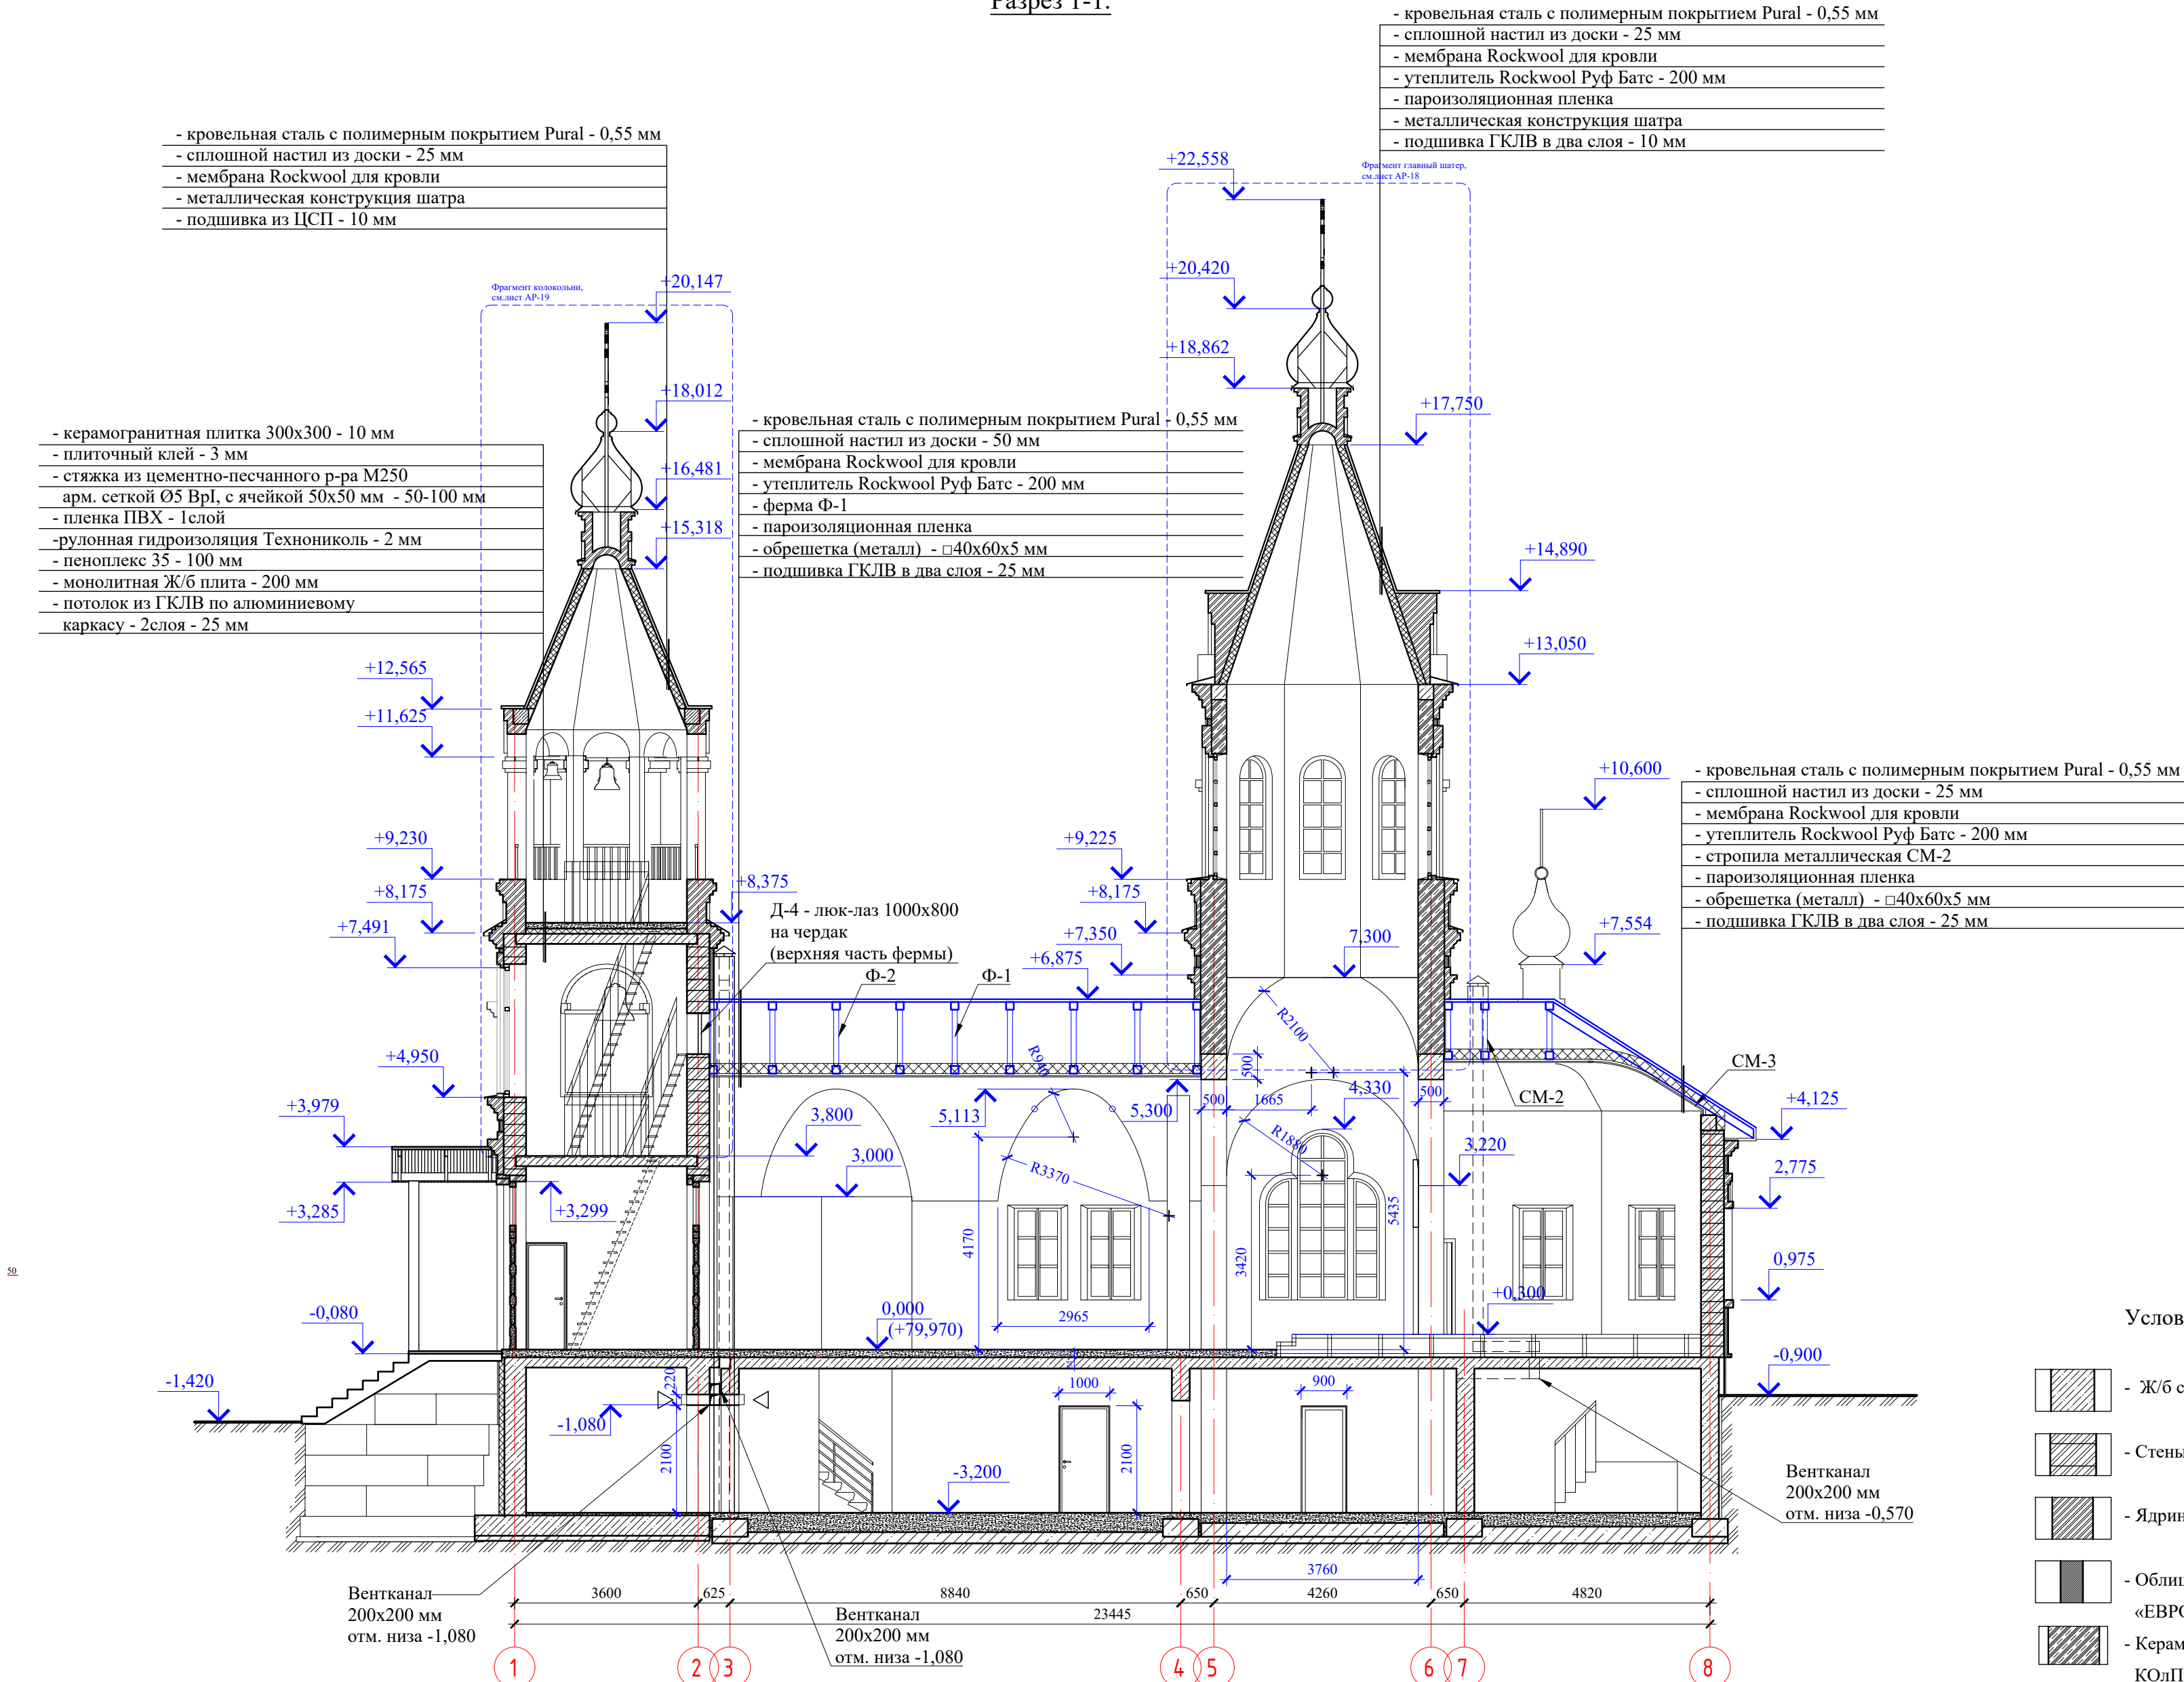


Условные обозначения :

 
-  - Ж/б стены и колонны
-  - Стены из керамических блоков "Porotherm" - 440мм
-  - Ядринский кирпич полнотелый - 250х120х65 мм
-  - Облицовка - кирпич керамическийлицевой
«ЕВРО» - 250х85х65 мм
-  - Керамический пустотелый кирпич
КОдПв — 250х120х65 мм

						0143.03.2023-АР			
						Храм Рождества Пресвятой Богородицы по адресу ул. Березовская рядом с профилакторием в Московском р-не г. Нижний Новгород			
Изм.	Кол.Уч	Лист	№док	Подпись	Дата				
Разработал						Иняев В.А.	Стадия	Лист	Листов
ГАП						Иняев А.А.	П	13	
Н.контр.						Иняев А.А.	Разрез 1-1. М 1:100.		
						«ООО Творческая мастерская архитектора Иняева А.А.»			


Разрез 2-2.

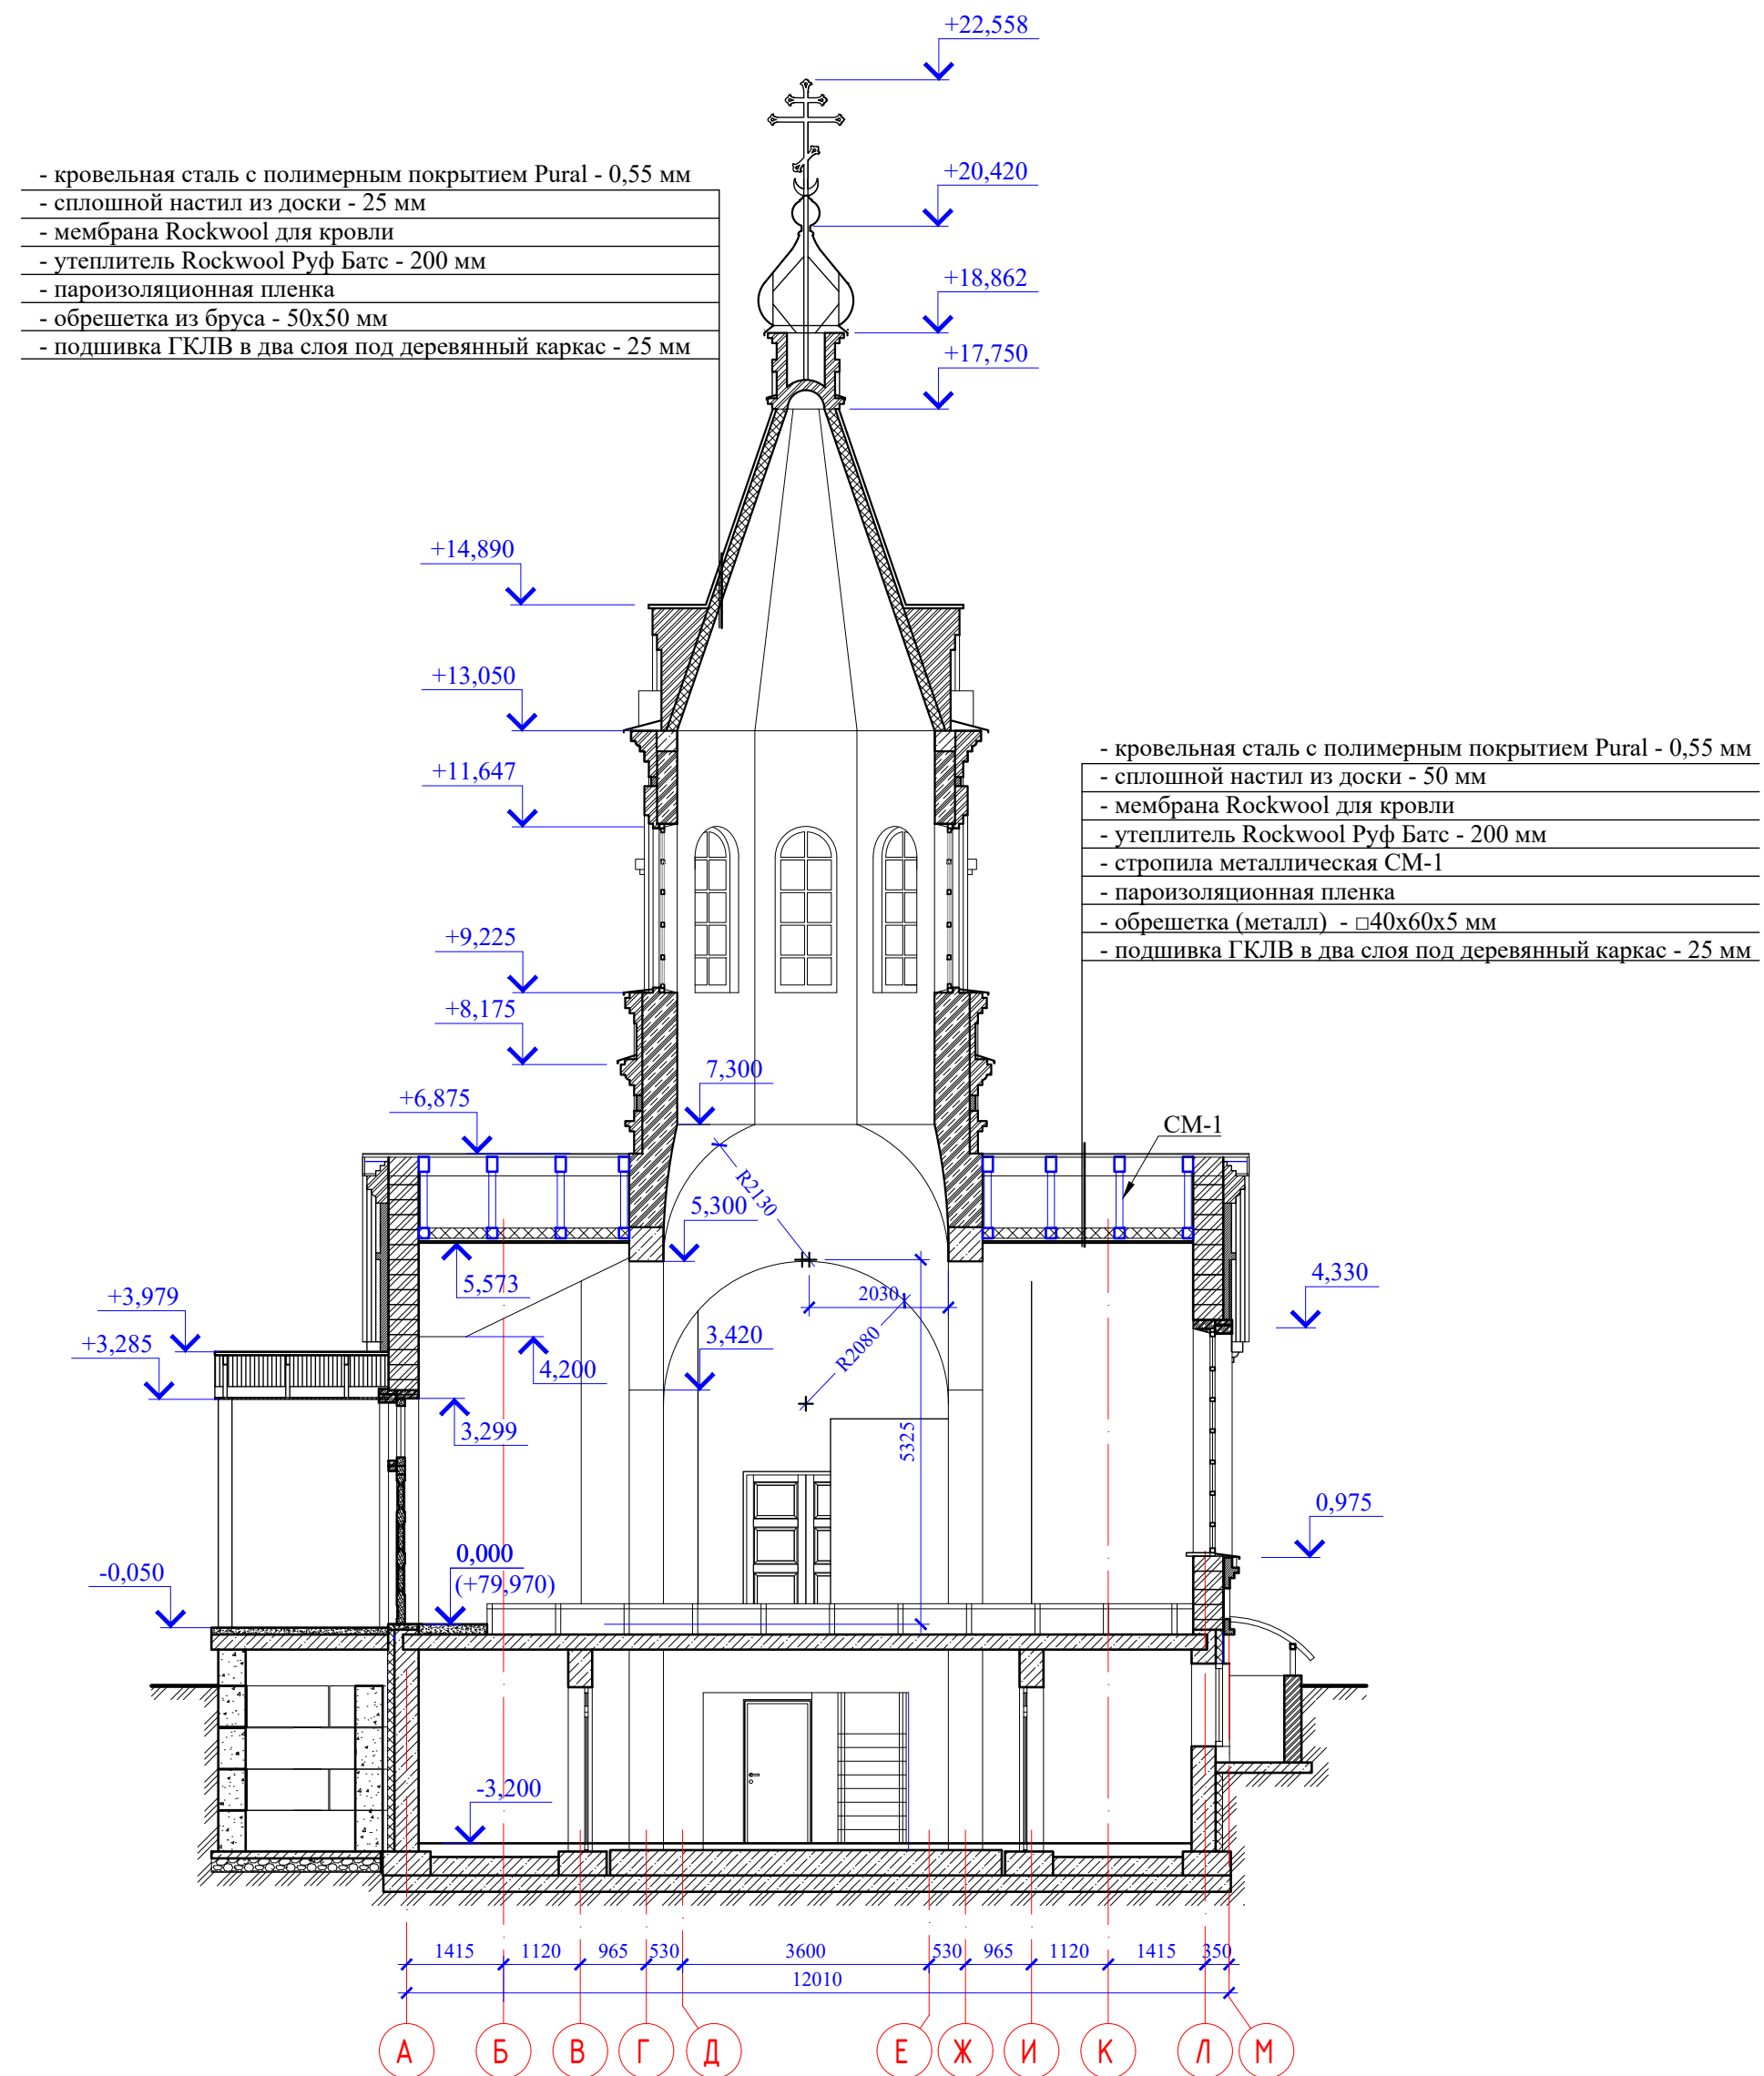

Условные обозначения :

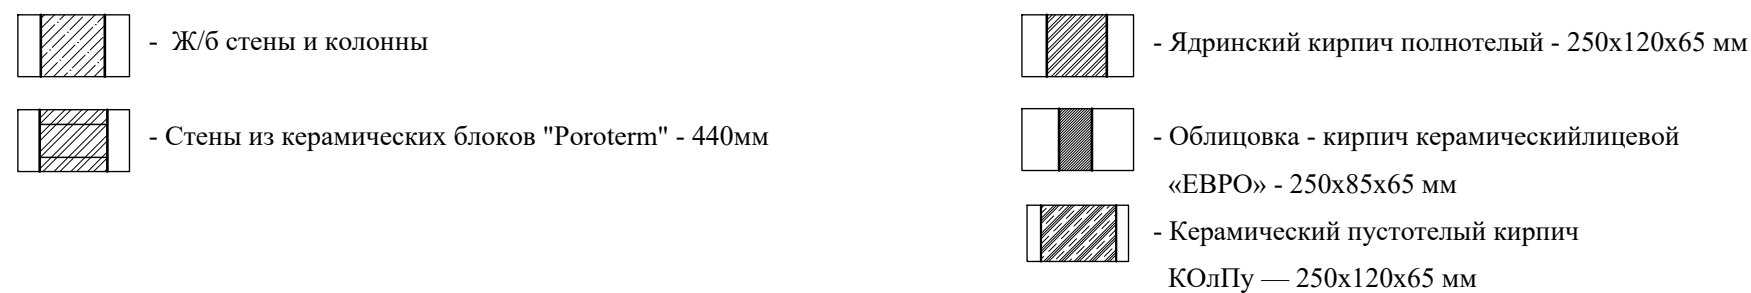


Разрез 3-3.

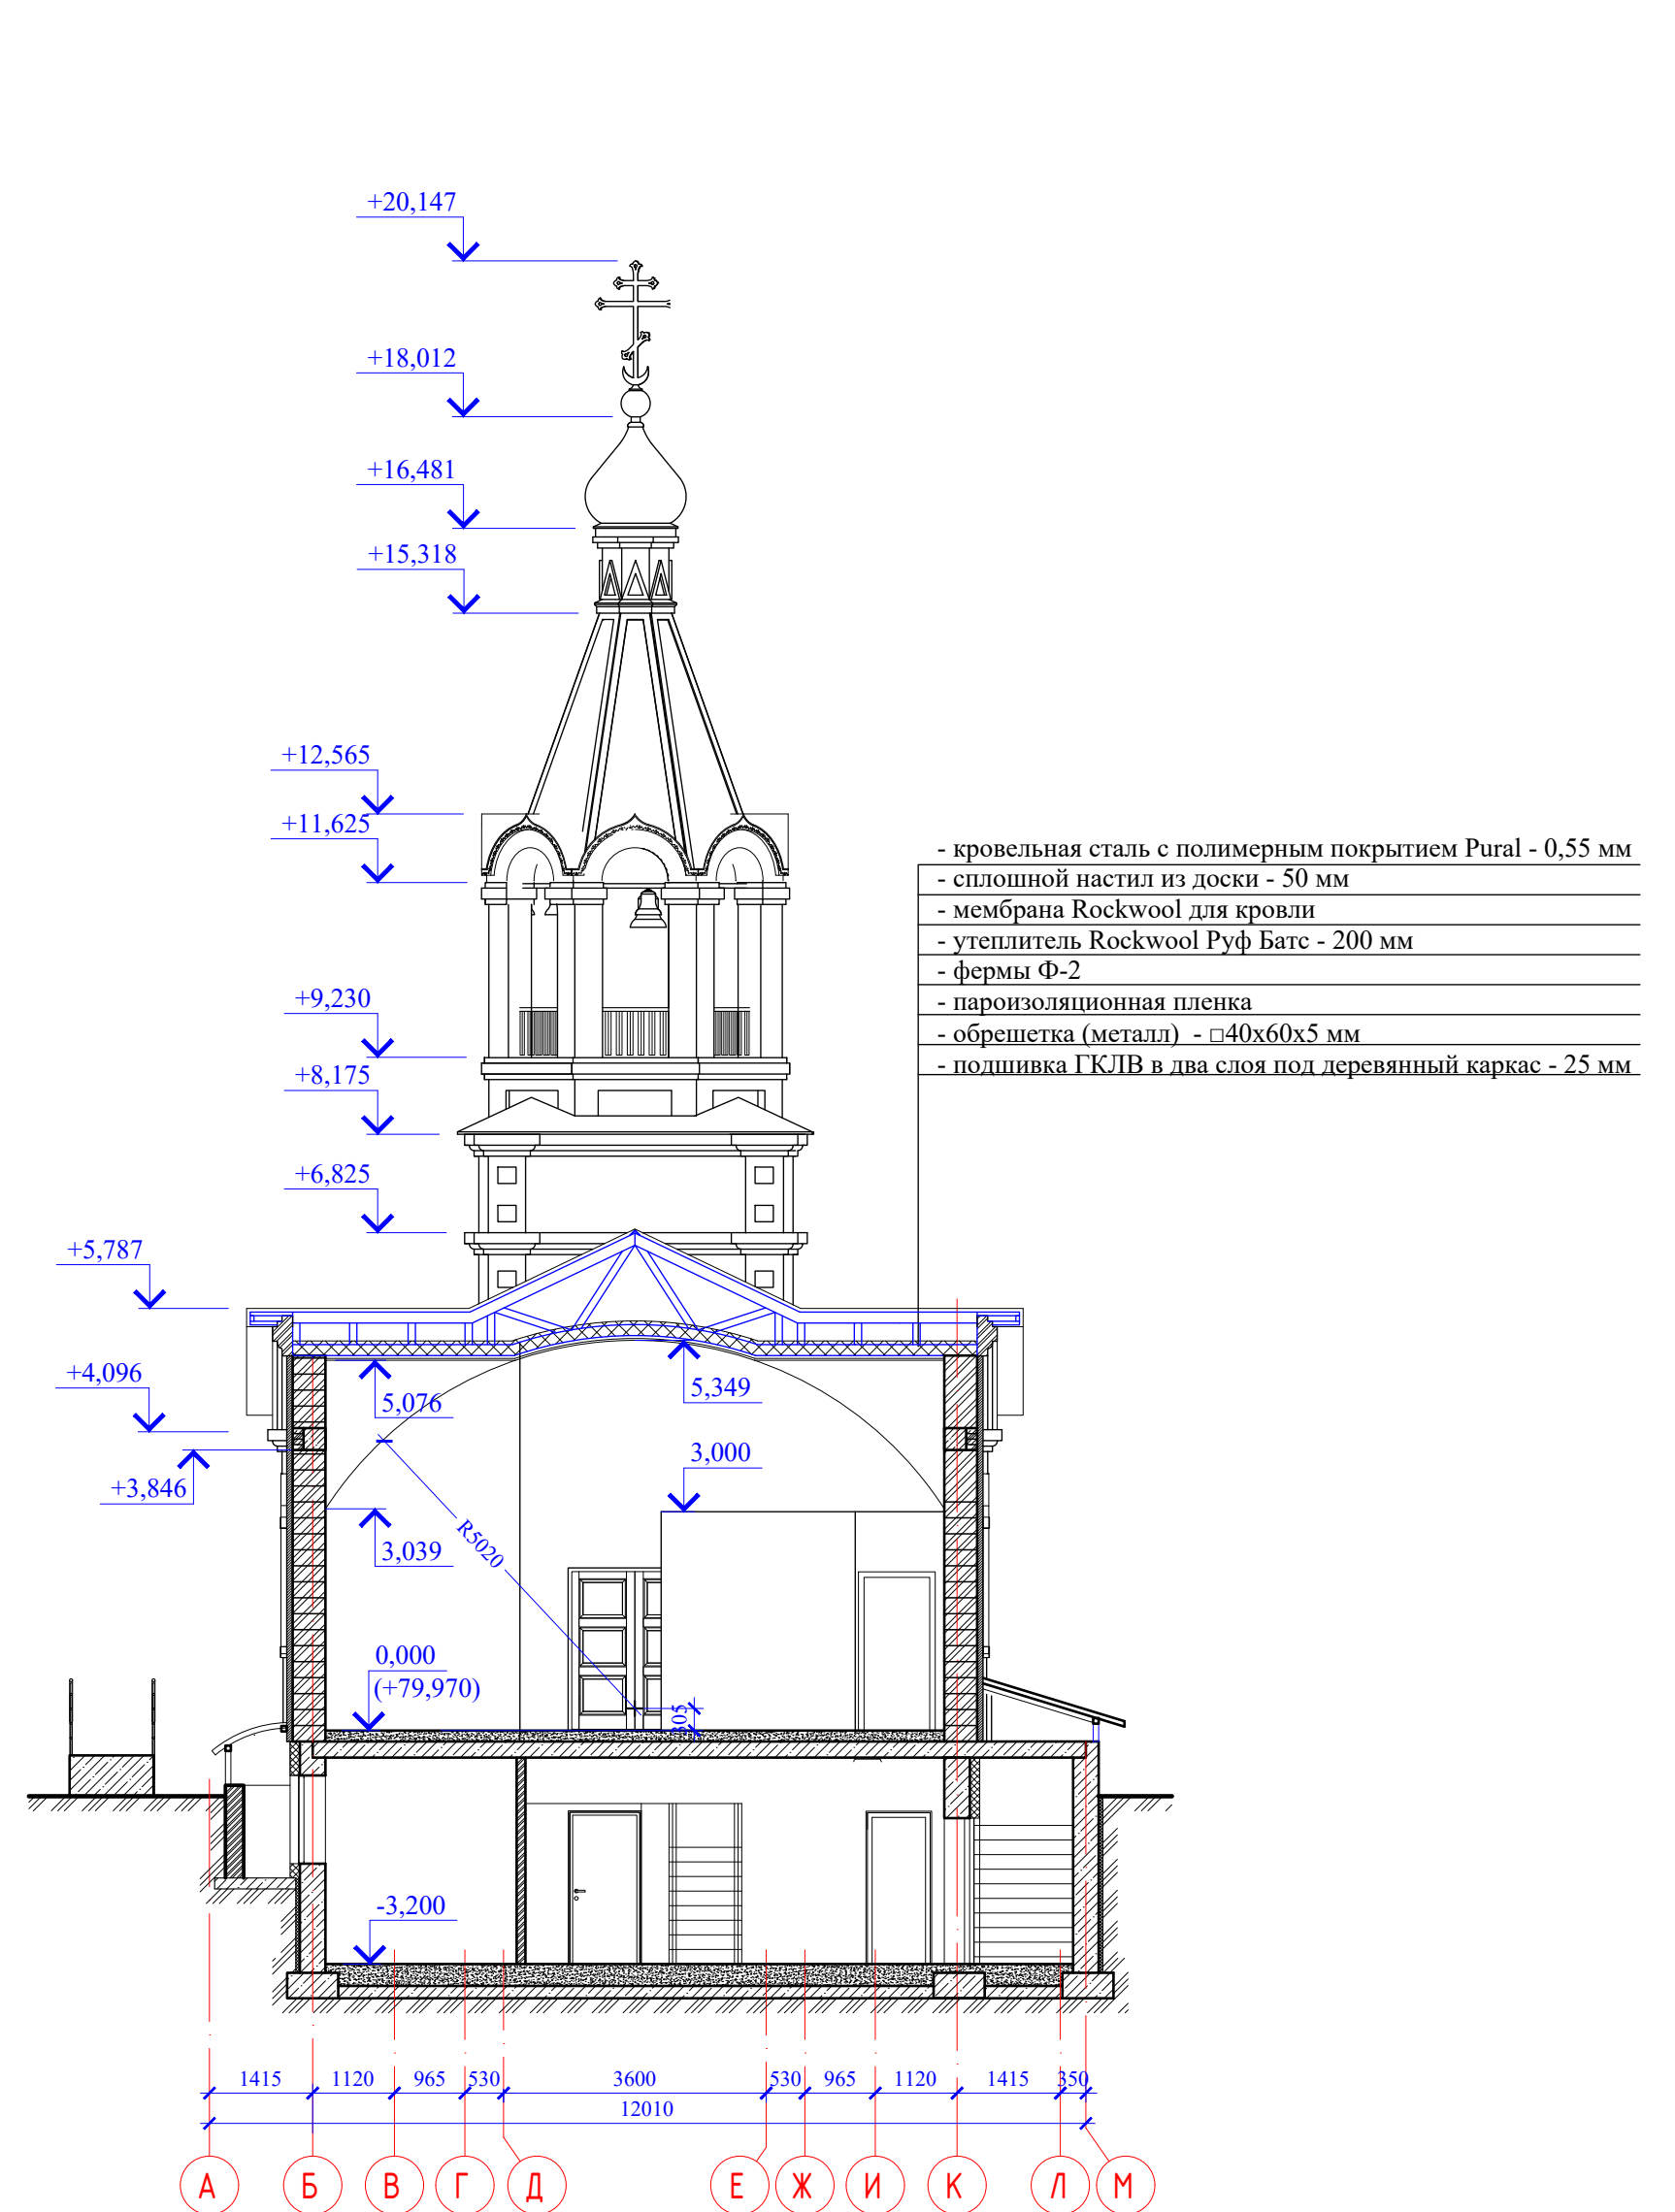


						0143.03.2023-АР			
						Храм Рождества Пресвятой Богородицы по адресу ул. Березовская рядом с профилакторием в Московском р-не г. Нижний Новгород			
Изм.	Код.Уч.	Лист	№ док.	Подпись	Дата				
Разработал	Иняев В.А.					Стадия	Лист	Листов	
ГАП	Иняев А.А.					П	14		
Н.контр.	Иняев А.А.					Разрез 2-2. Разрез 3-3. М 1:100.		«ООО Творческая мастерская архитектора Иняева А.А.»	

Разрез 4-4.

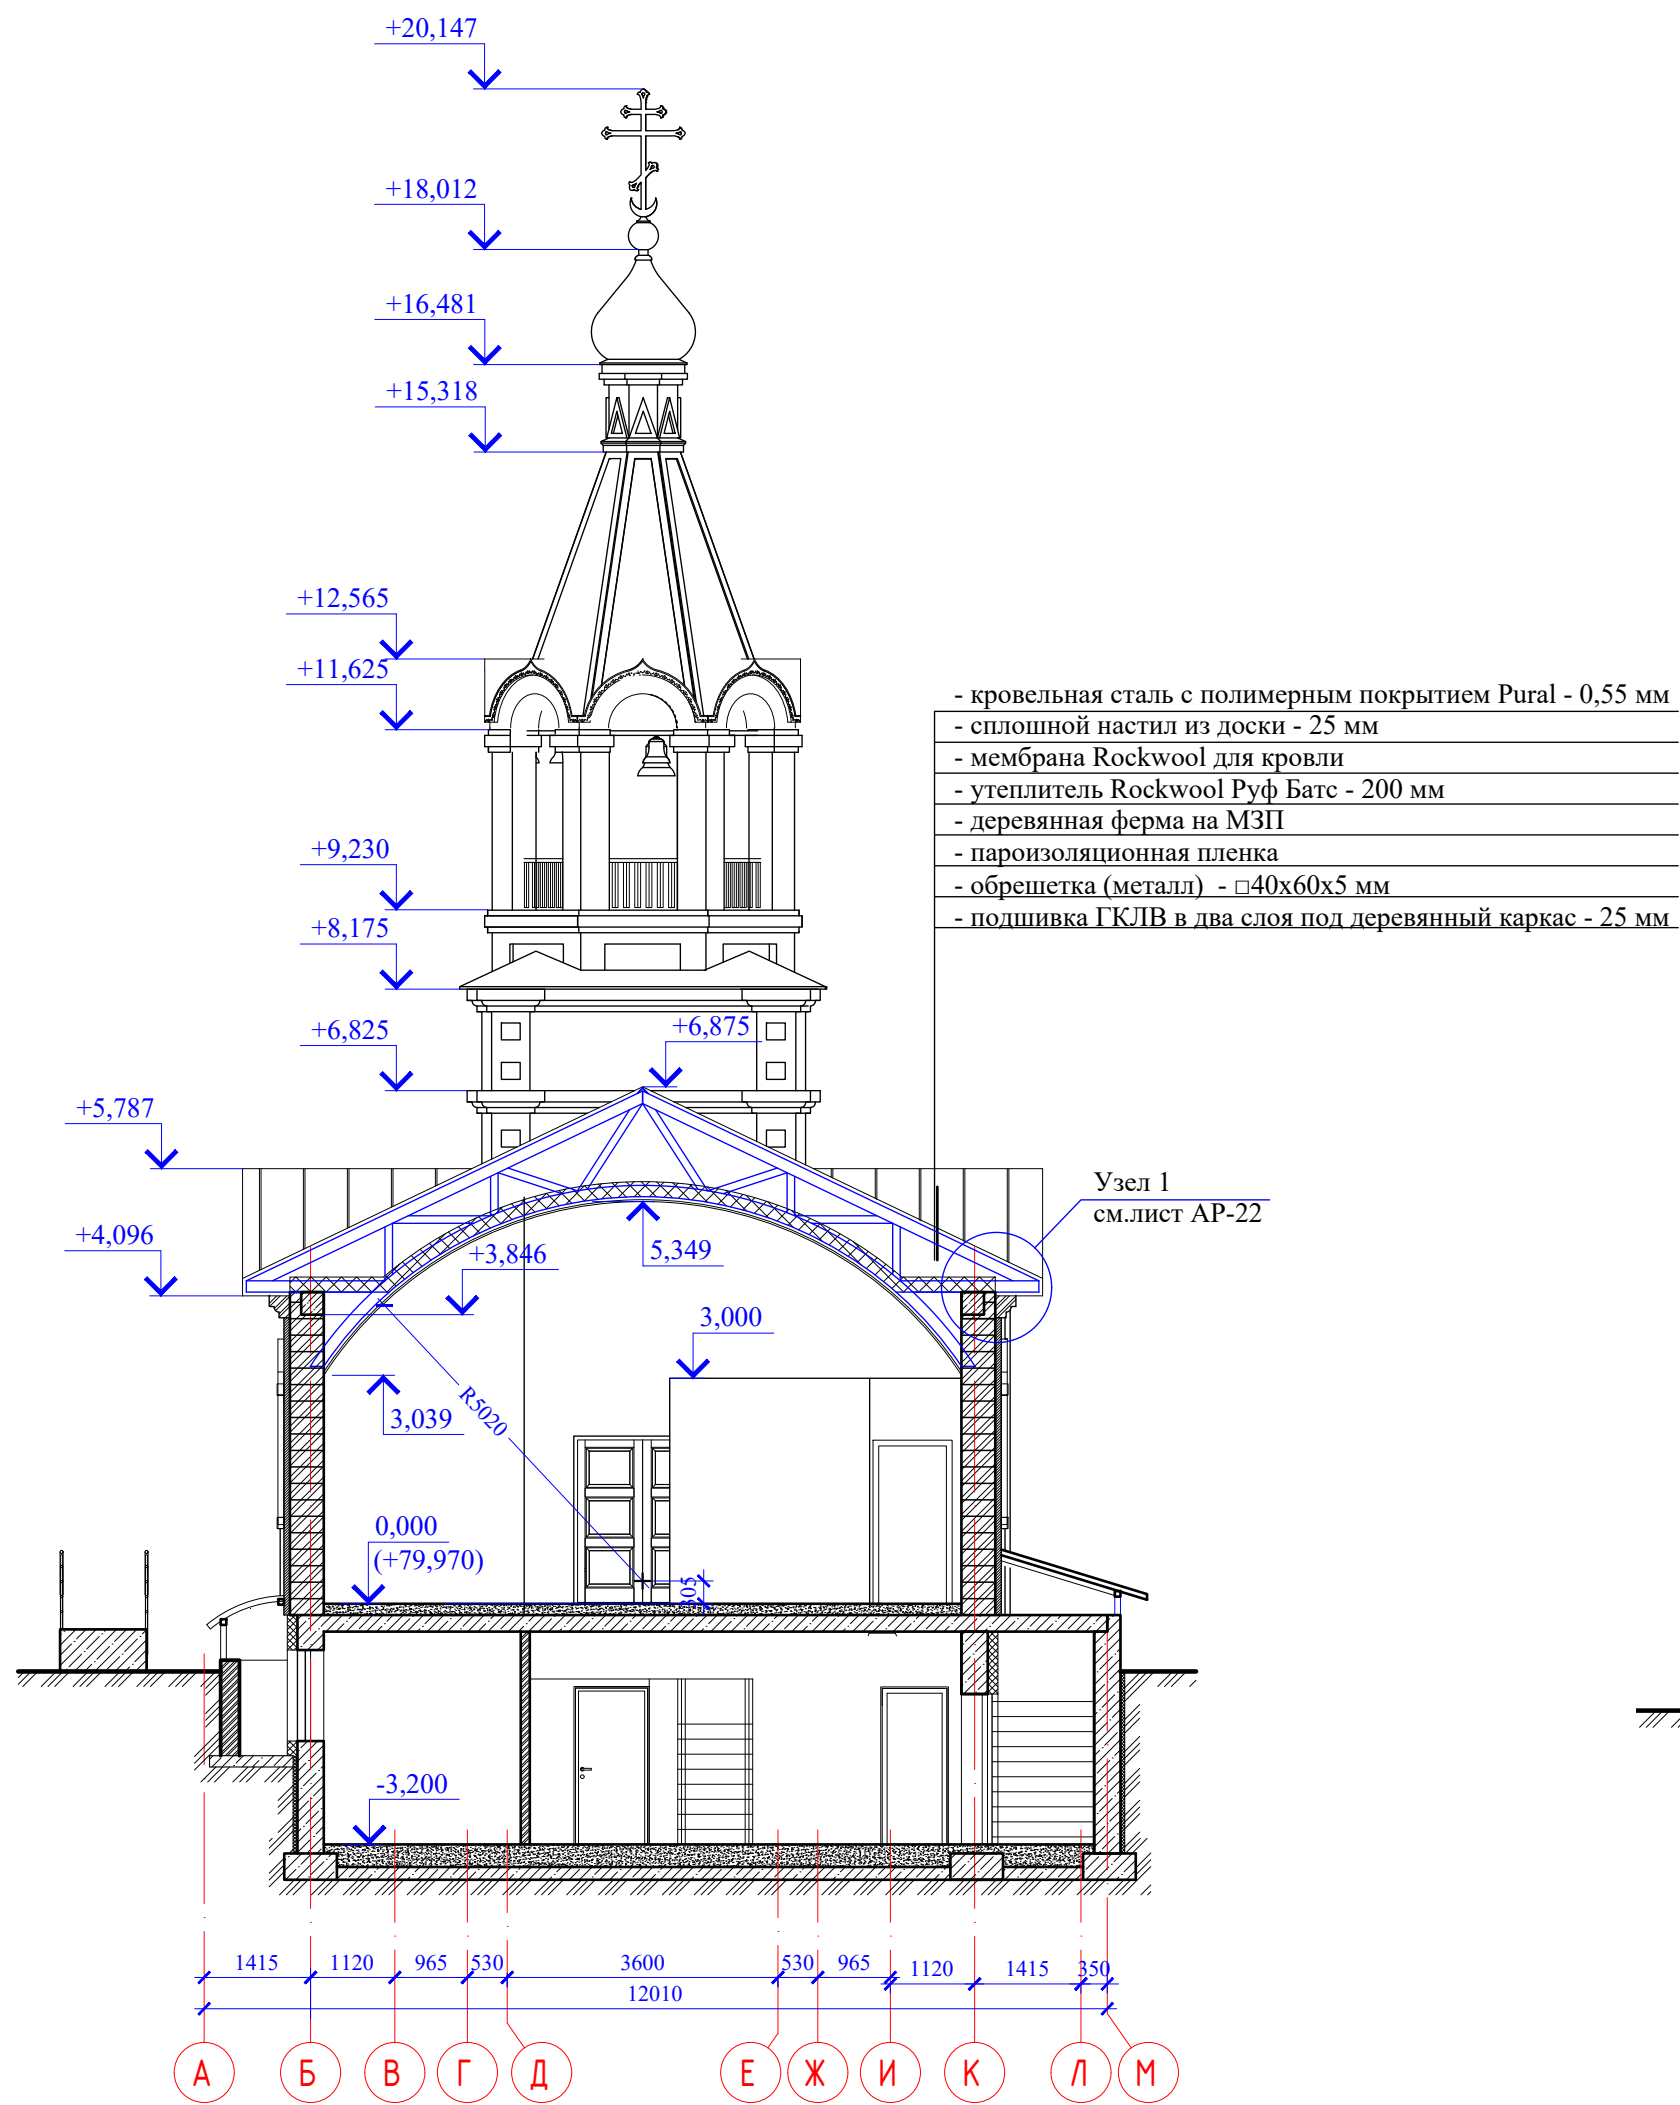

Разрез 5-5.

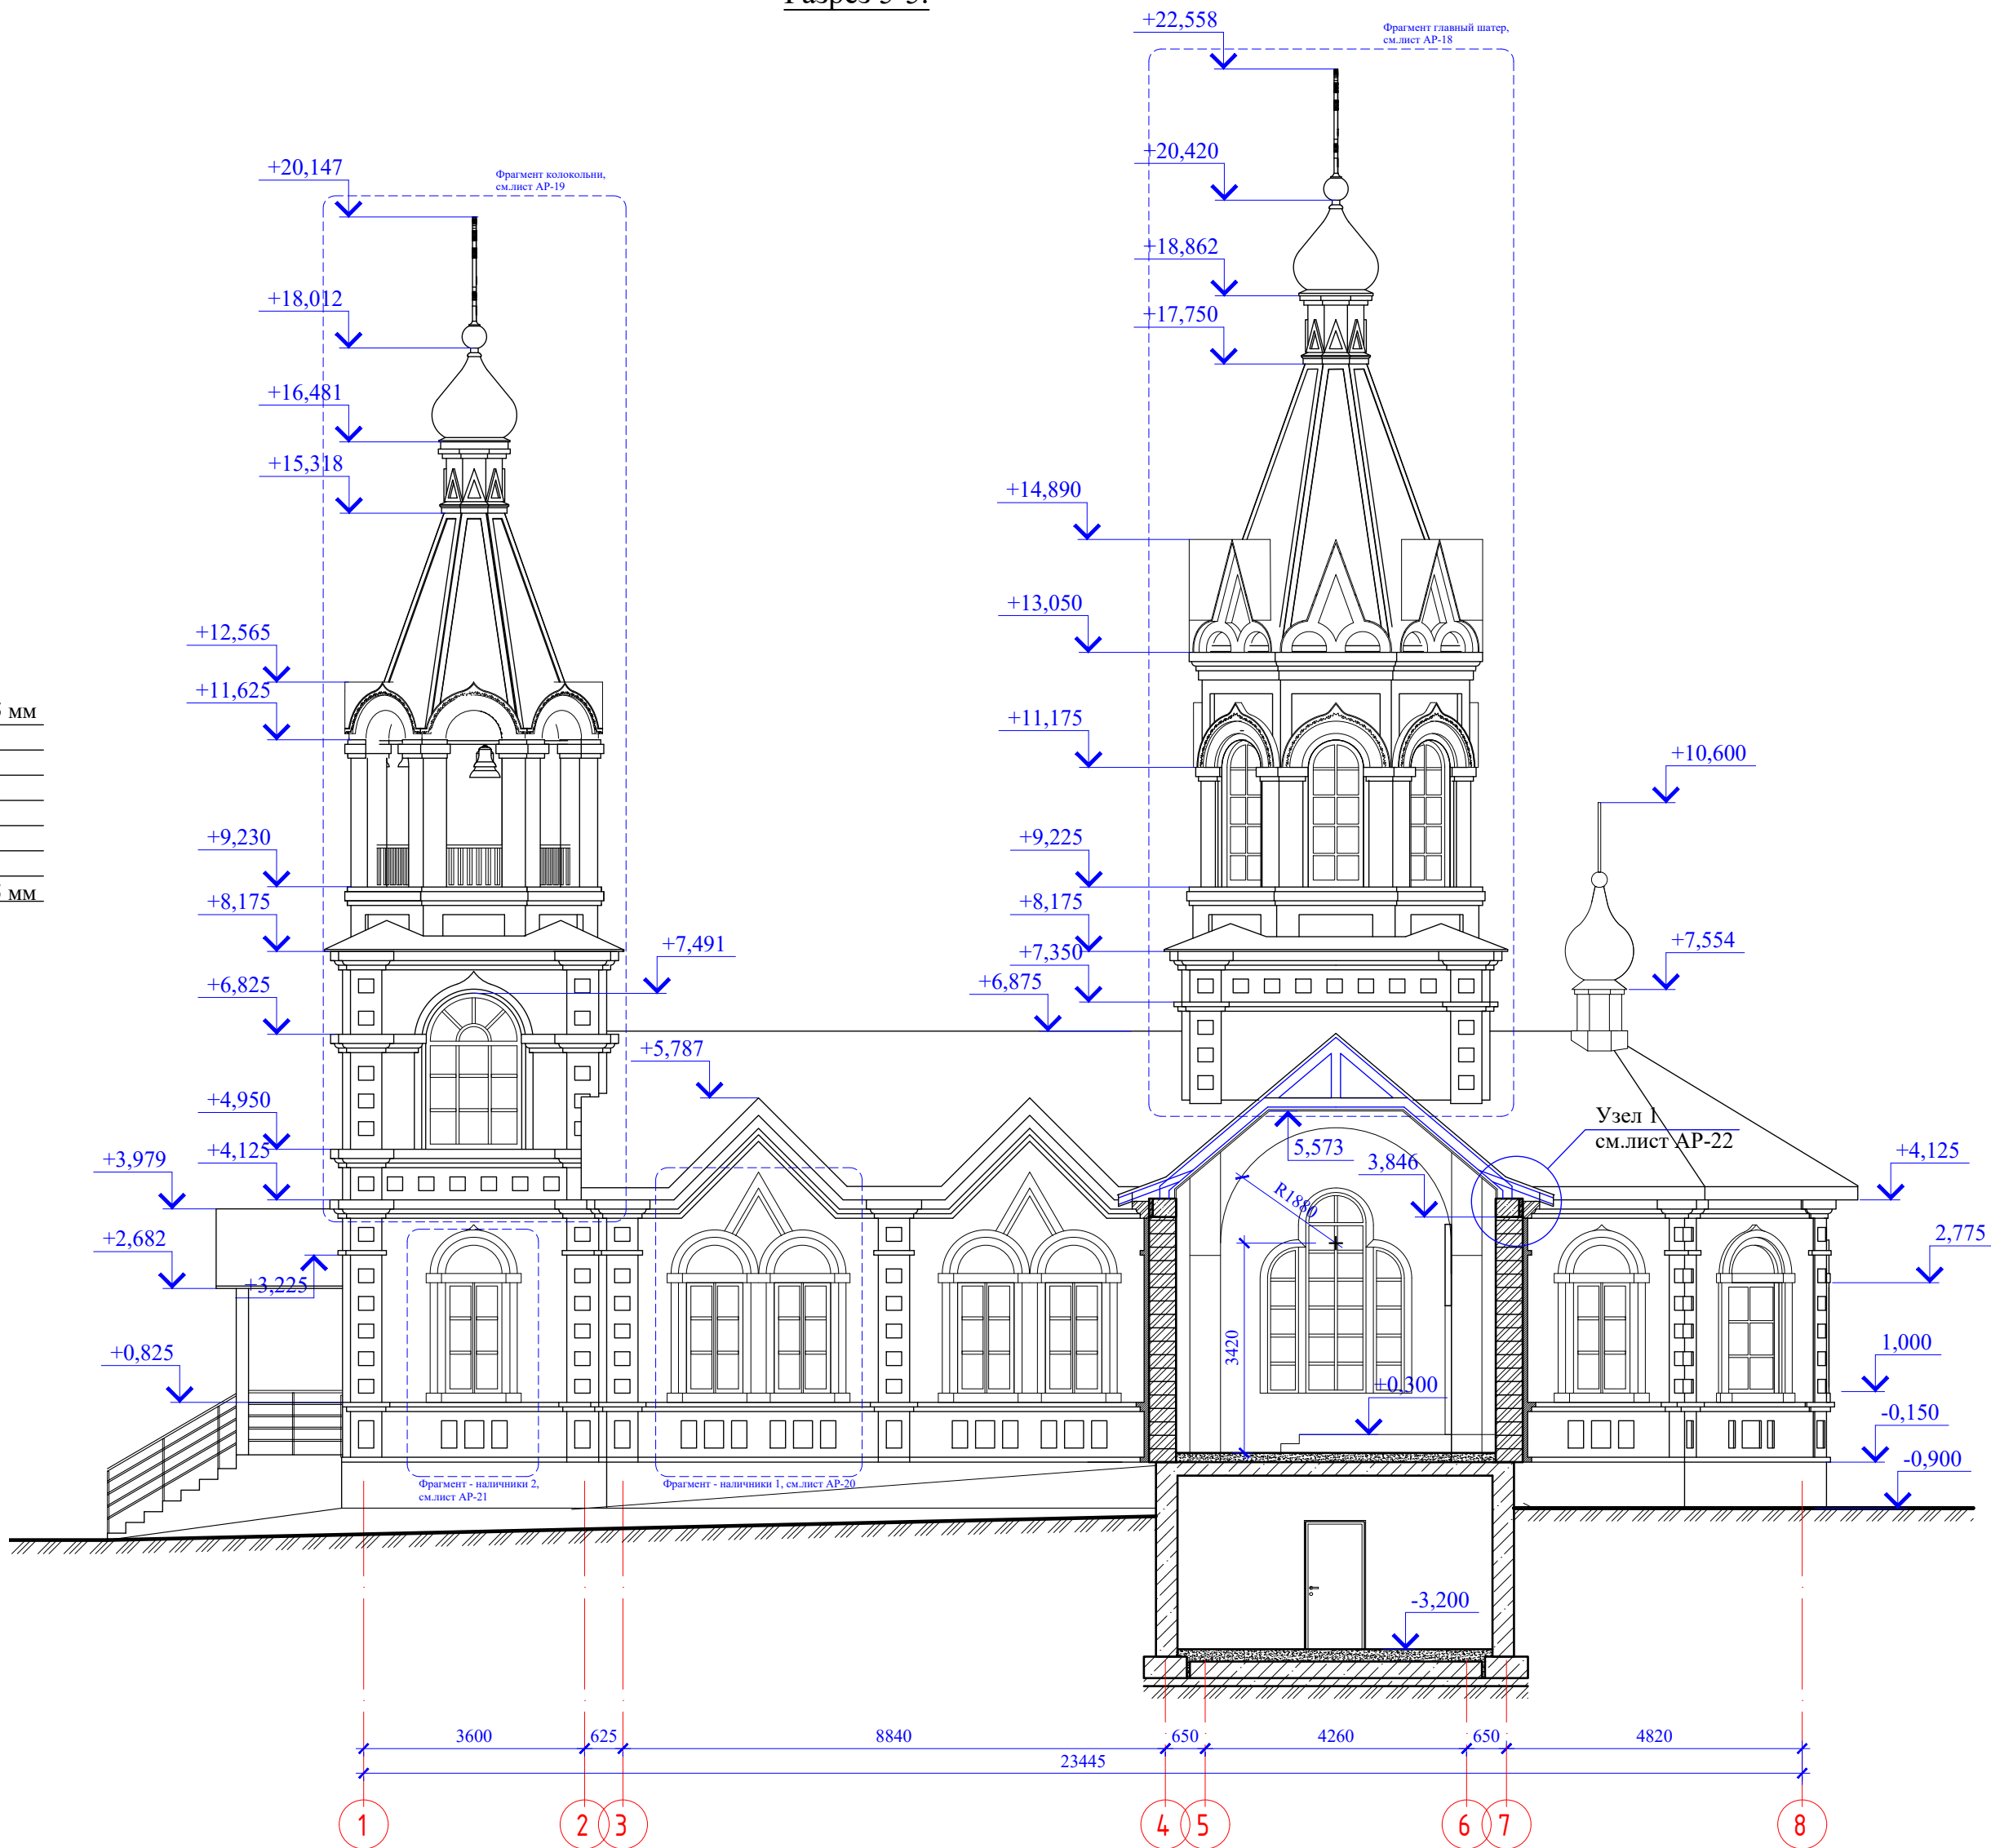

Условные обозначения :


- | | | | |
|--|--|--|--|
| | - Ж/б стены и колонны | | - Ядринский кирпич полнотелый - 250x120x65 мм |
| | - Стены из керамических блоков "Porotherm" - 440мм | | - Облицовка - кирпич керамическийлицевой «ЕВРО» - 250x85x65 мм |
| | | | - Керамический пустотелый кирпич КолПу — 250x120x65 мм |

0143.03.2023-AP					
Храм Рождества Пресвятой Богородицы по адресу ул. Березовская рядом с профилакторием в Московском р-не г. Нижний Новгород					
Изм.	Кол.Уч	Лист	№док	Подпись	Дата
Разработал	Иняев В.А.				
ГАП	Иняев А.А.				
				Стадия	Лист
				П	15
				Листов	
Разрез 4-4, Разрез 5-5. М 1:100.				«ООО Творческая мастерская архитектора Иняева А.А.»	
Н.контр.	Иняев А.А.				


Согласовано

Изм.	Кол.Уч	Лист	№ док	Подпись	Дата
Разработал	Иняев В.А.				
ГАП	Иняев А.А.				
Иняев А.А.					
Н.контр.	Иняев А.А.				

Изм. № подл. Подп. и дата. Взам. инв. №

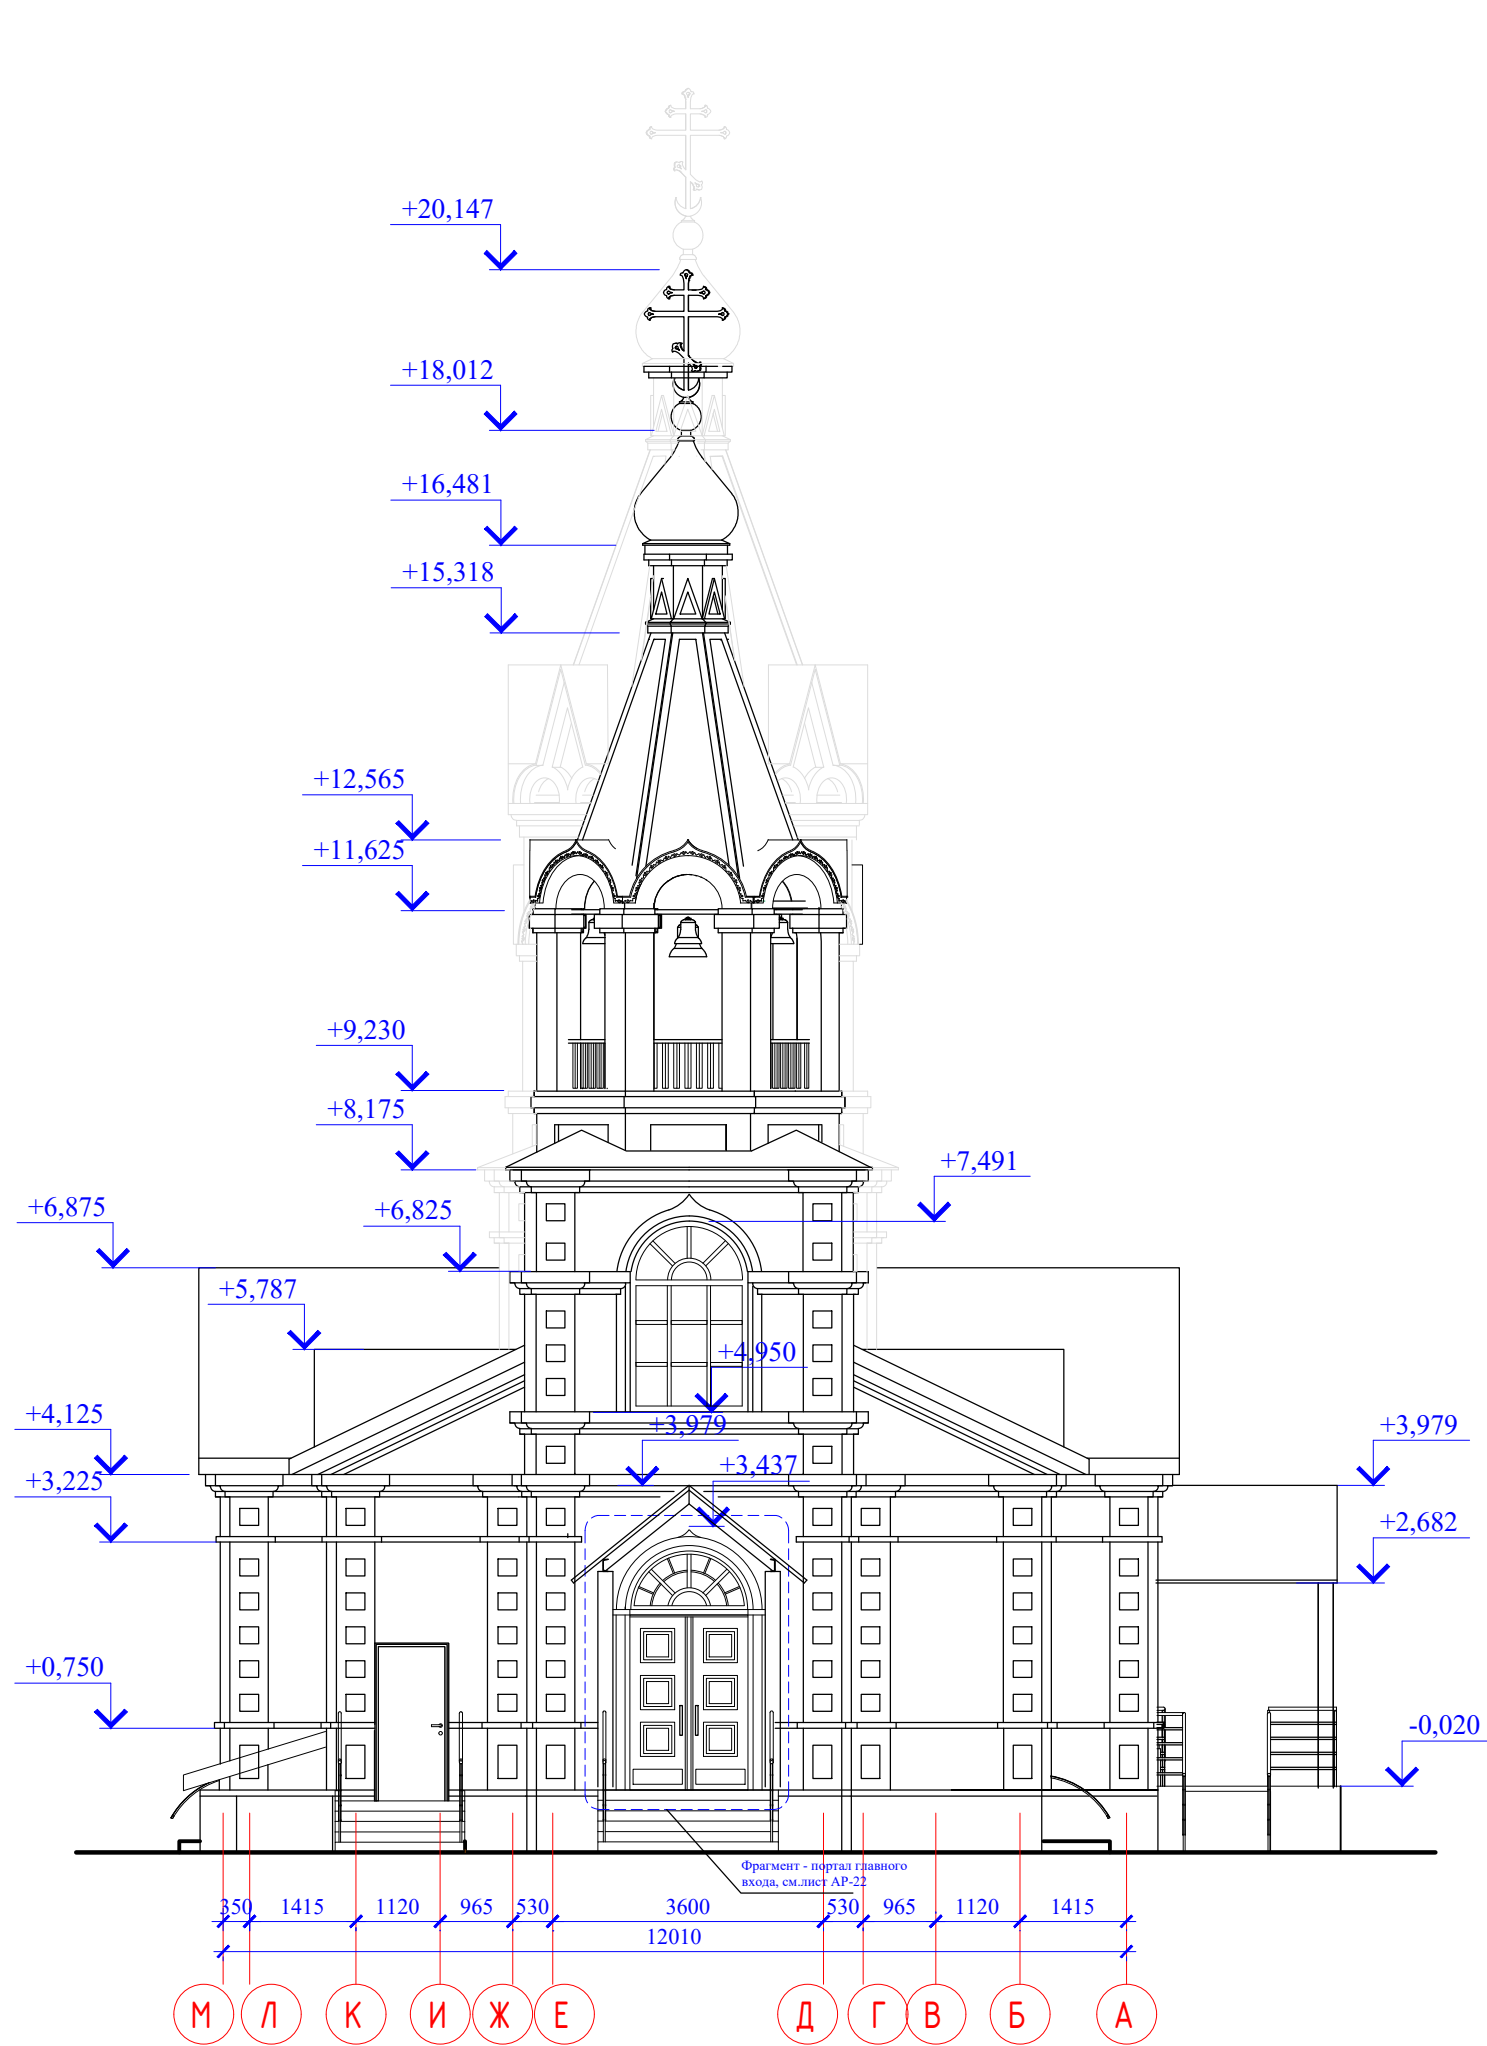


Фасад М-А. М 1:100.

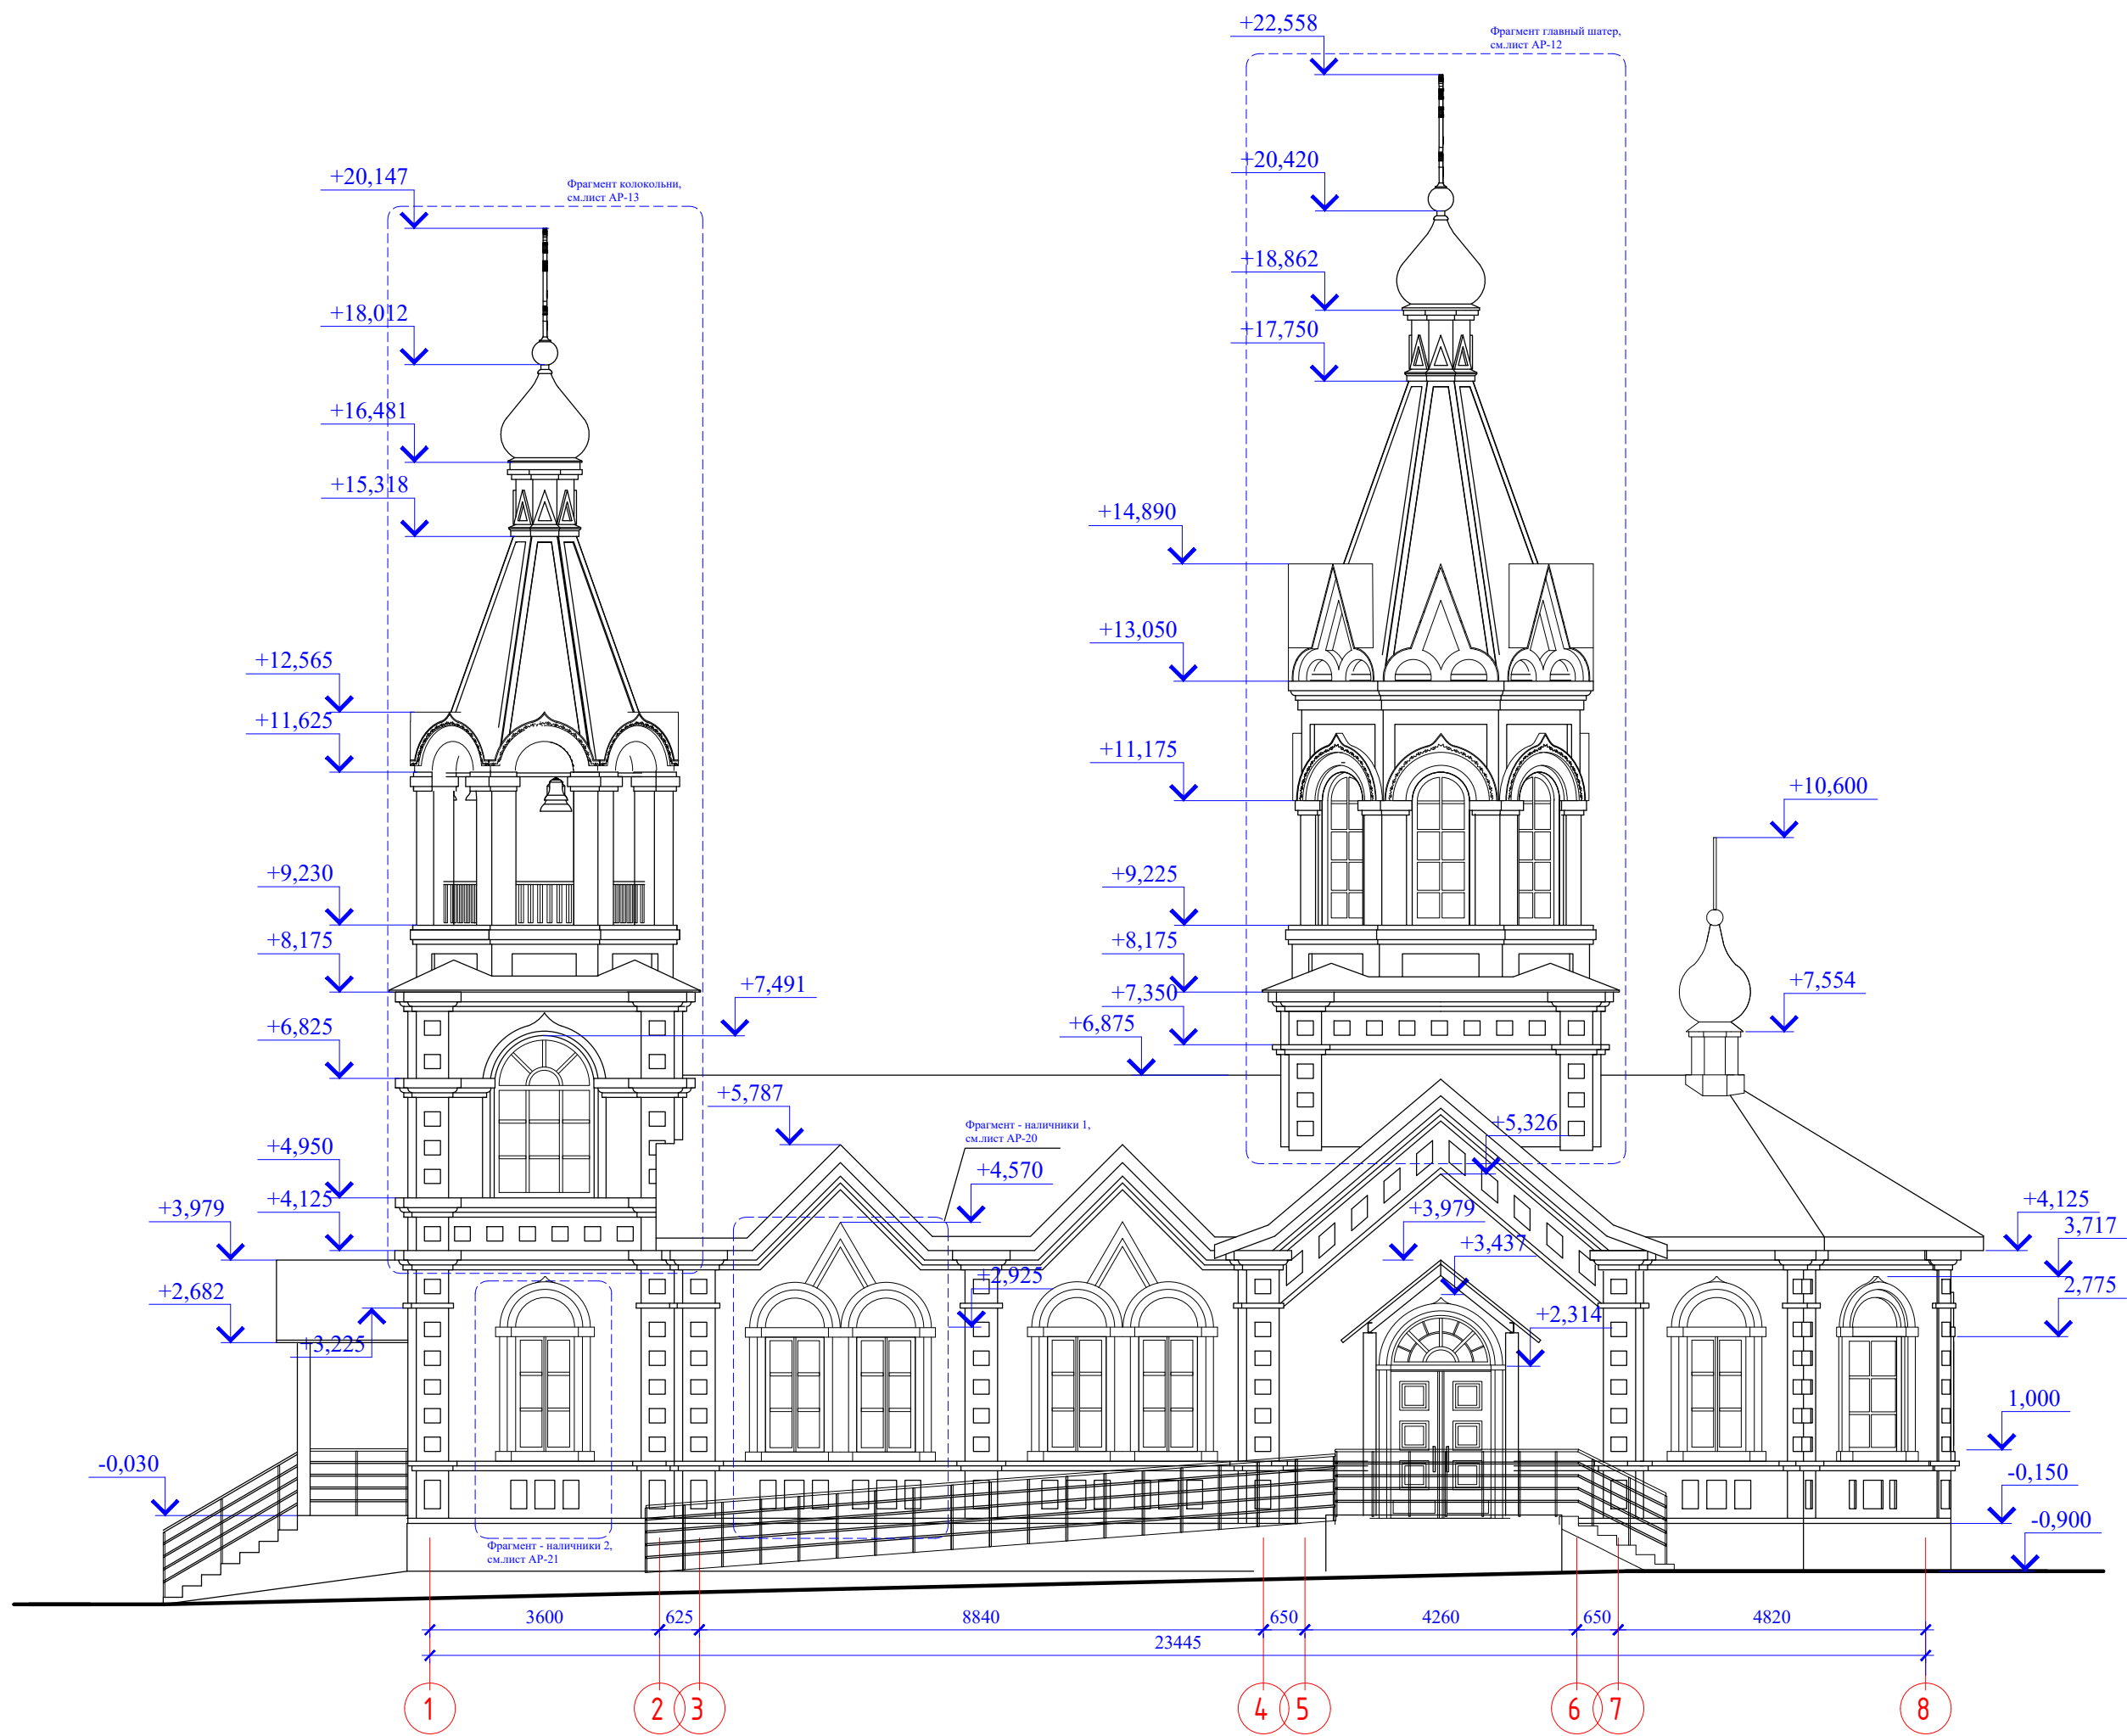


Фасад 1-8. М 1:100.

0143.03.2023-АР					
Храм Рождества Пресвятой Богородицы по адресу ул. Березовская рядом с профилакторием в Московском р-не г. Нижний Новгород					
Изм.	Кол.Уч	Лист	№ док	Подпись	Дата
Разработал	Иняев В.А.				
ГАП	Иняев А.А.				
Иняев А.А.					
Н.контр.	Иняев А.А.				
Фасад М-А. Фасад 1-8. М 1:100.				Стадия	Лист
				П	16
				Листов	
				«ООО Творческая мастерская архитектора Иняева А.А.»	

Согласовано					
Изм. № подл.	Подп. и дата	Взам. инв. №			

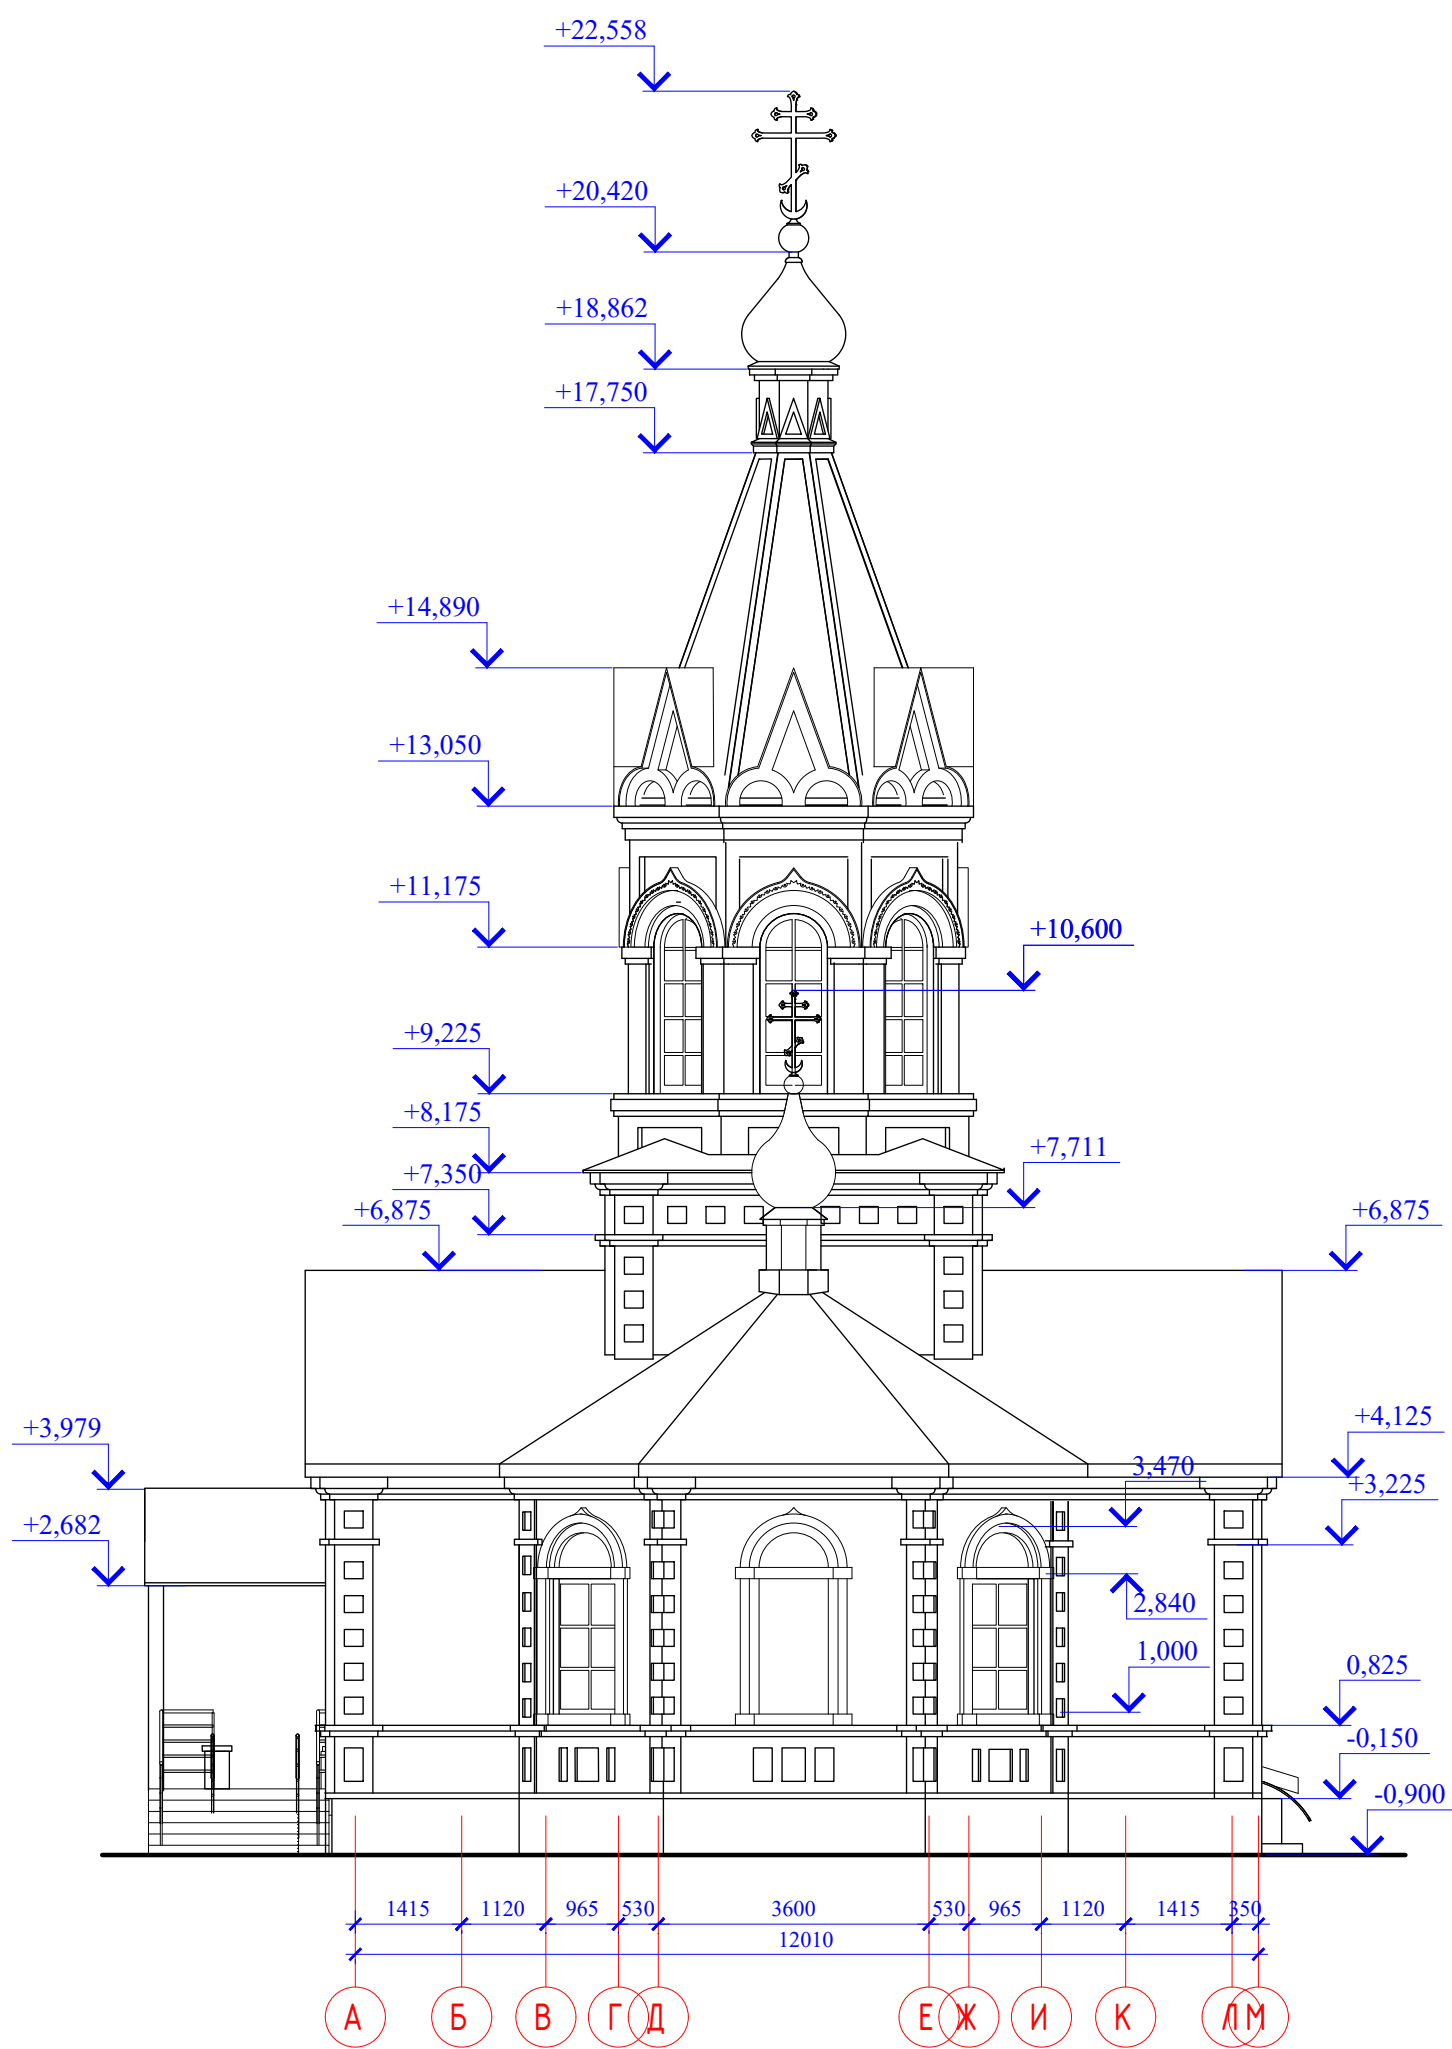


Фасад А-М. М 1:100.





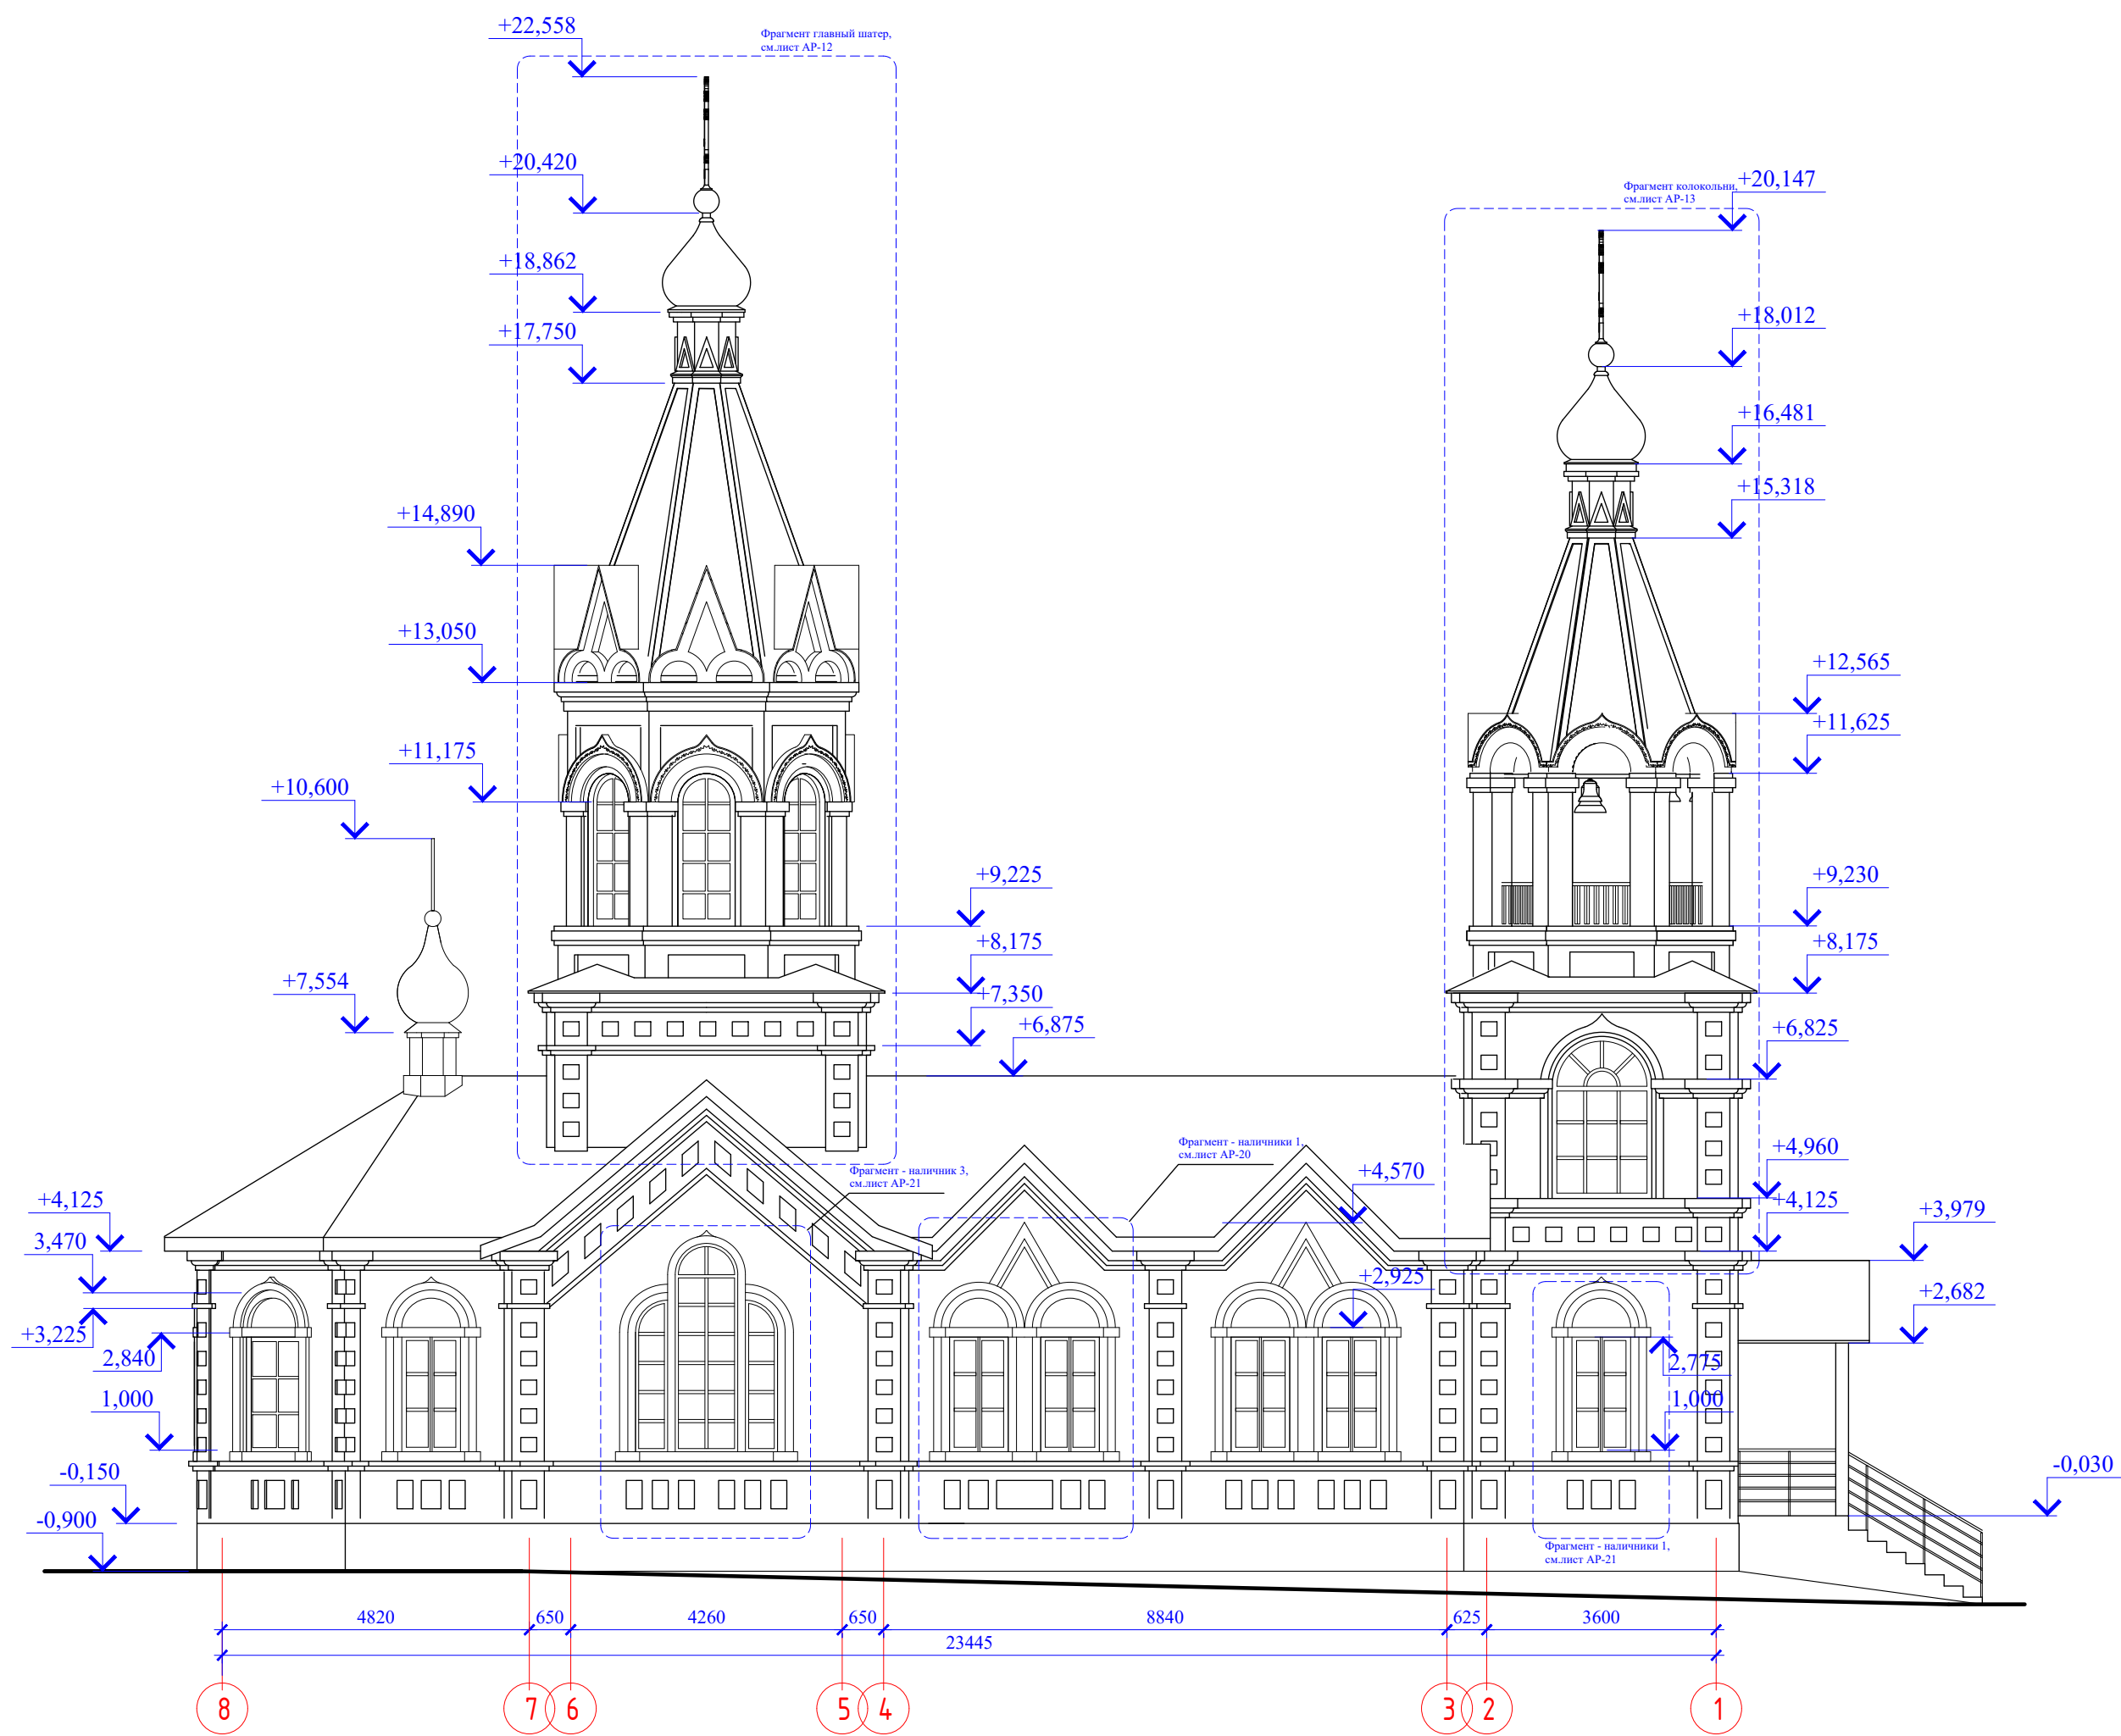


Фасад 8-1. М 1:100.

						0143.03.2023-АР				
						Храм Рождества Пресвятой Богородицы по адресу ул. Березовская рядом с профилакторием в Московском р-не г. Нижний Новгород				
Изм.	Кол.Уч	Лист	№док	Подпись	Дата					
Разработал	Иняев В.А.					Стадия	Лист	Листов		
ГАП	Иняев А.А.					П	17			
						«ООО Творческая мастерская архитектора Иняева А.А.»				
Н.контр.	Иняев А.А.					Фасад А-М. Фасад 8-1. М 1:100.				

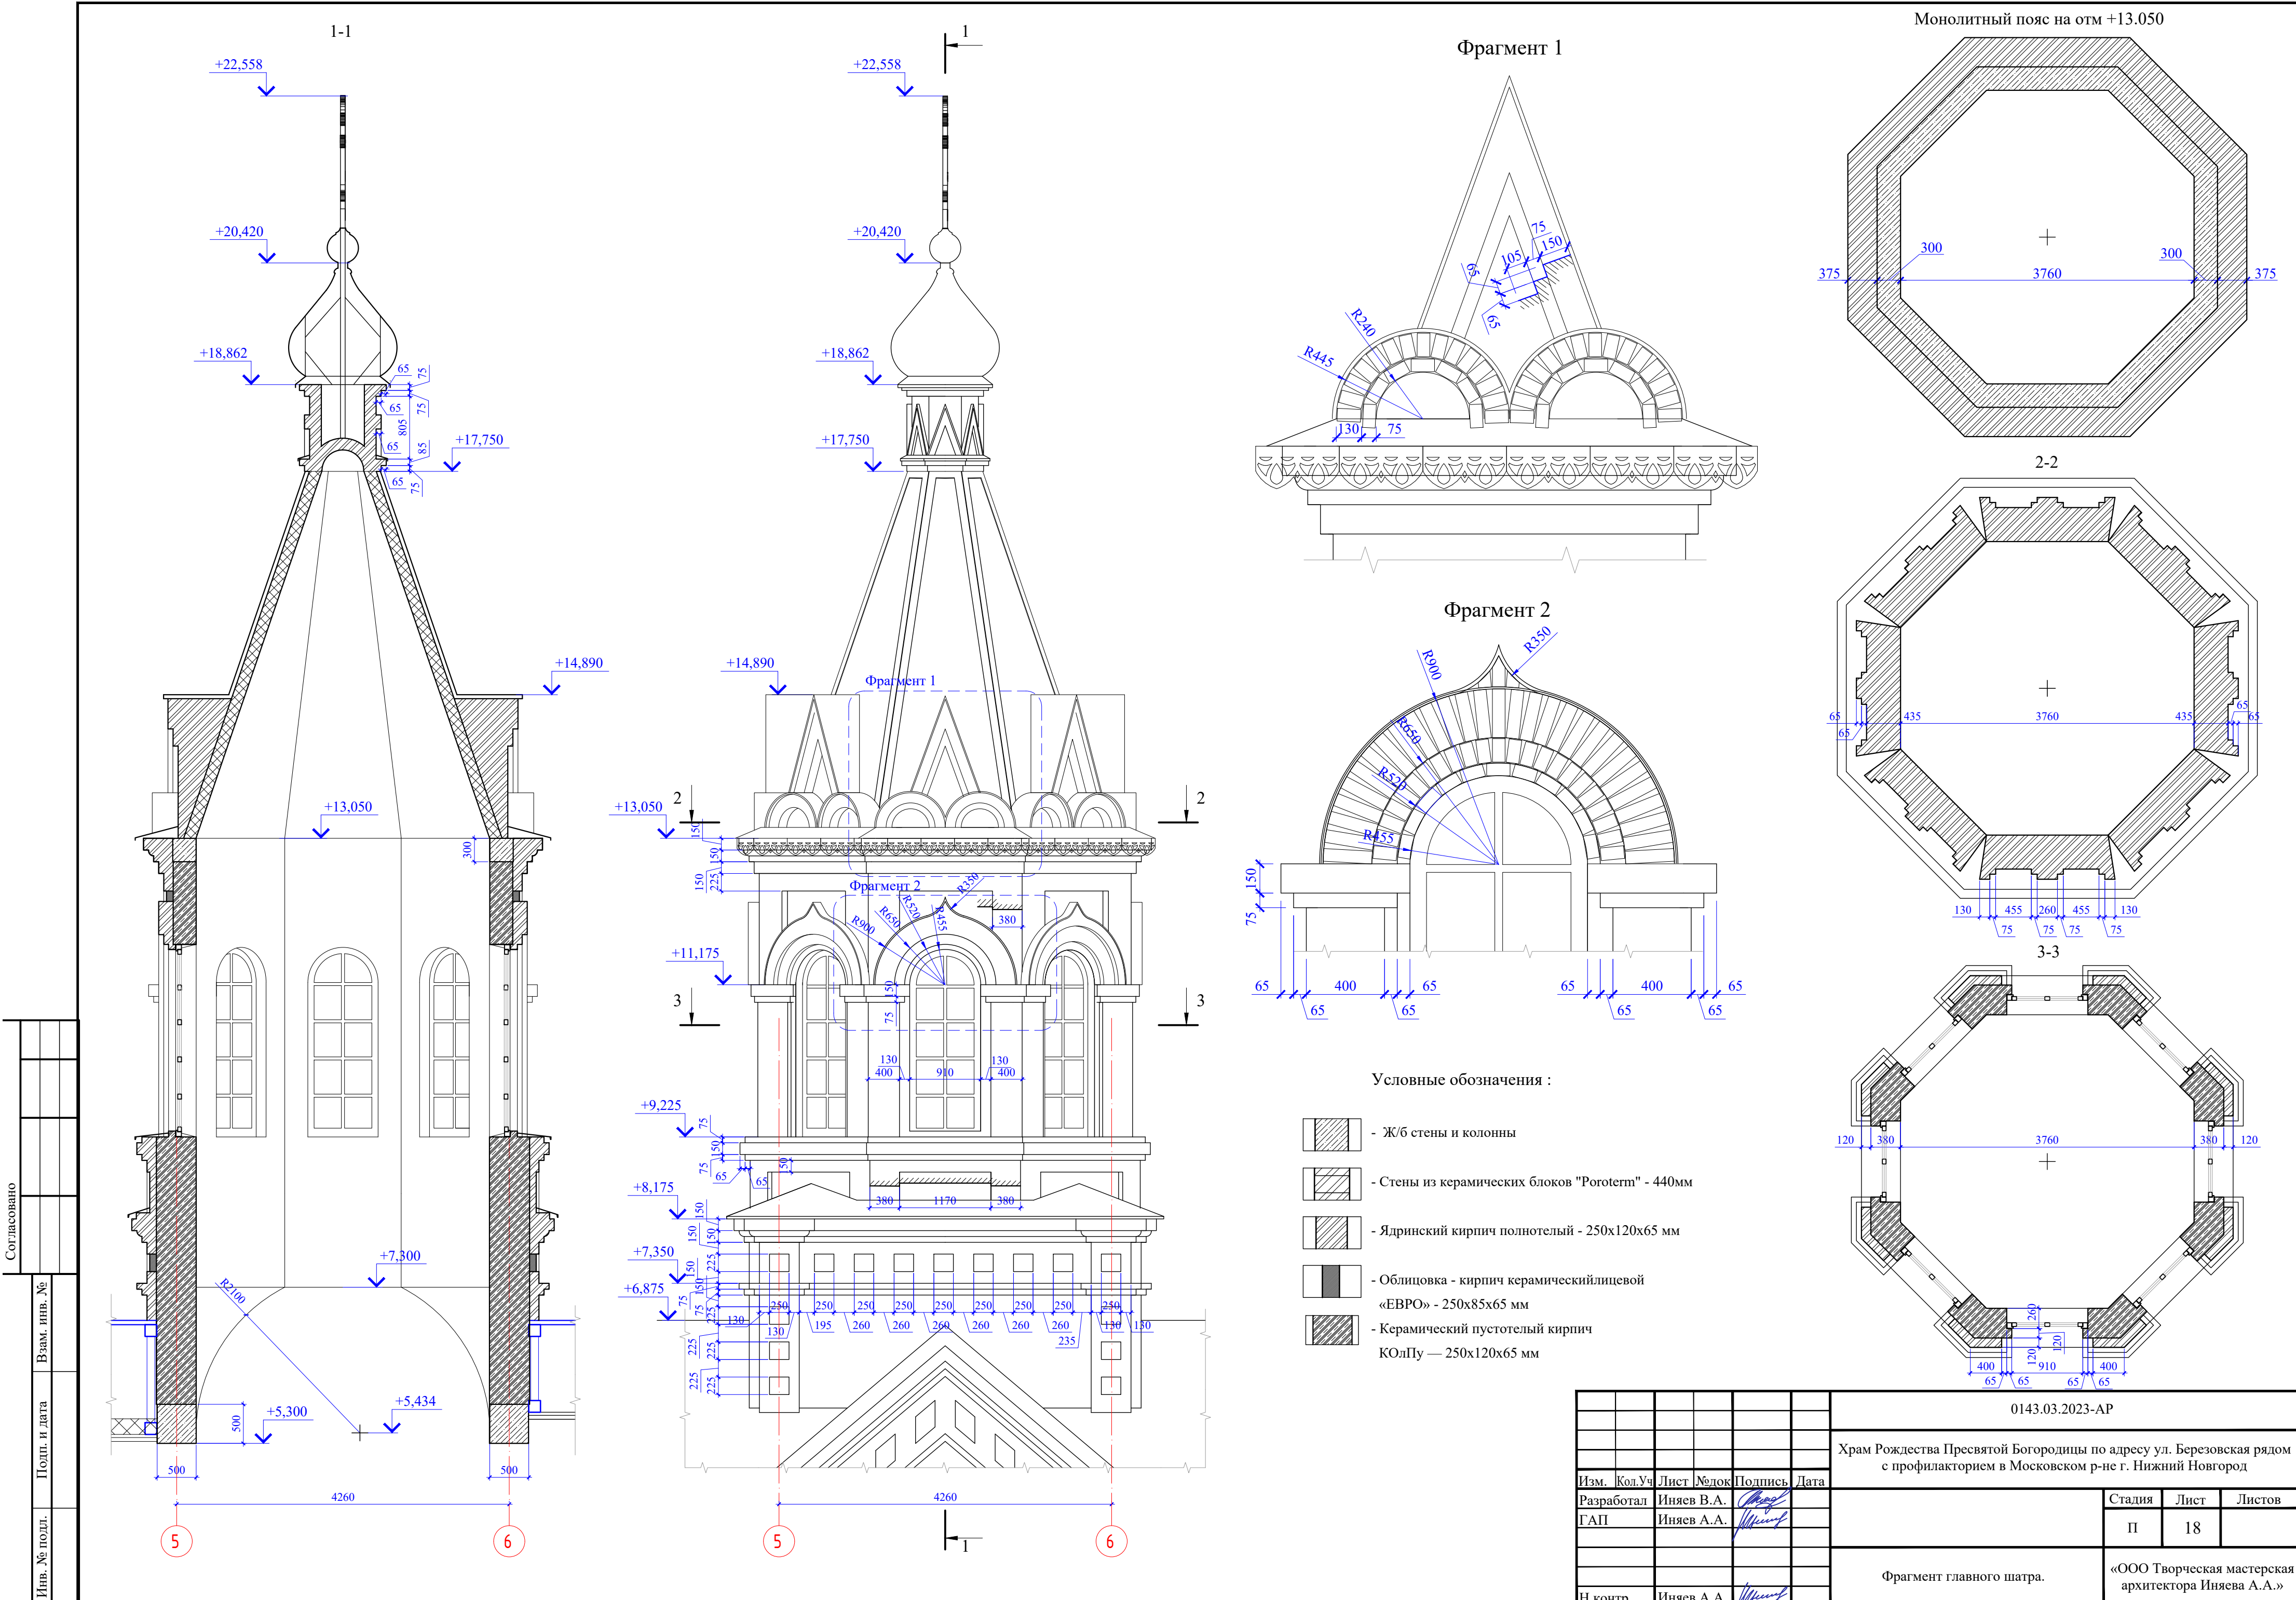


Согласовано					
Изм.	Кол.Уч	Лист	№ док	Подпись	Дата
Разработал	Иняев В.А.				
ГАП	Иняев А.А.				
Иняев А.А.					
Н.контр.	Иняев А.А.				

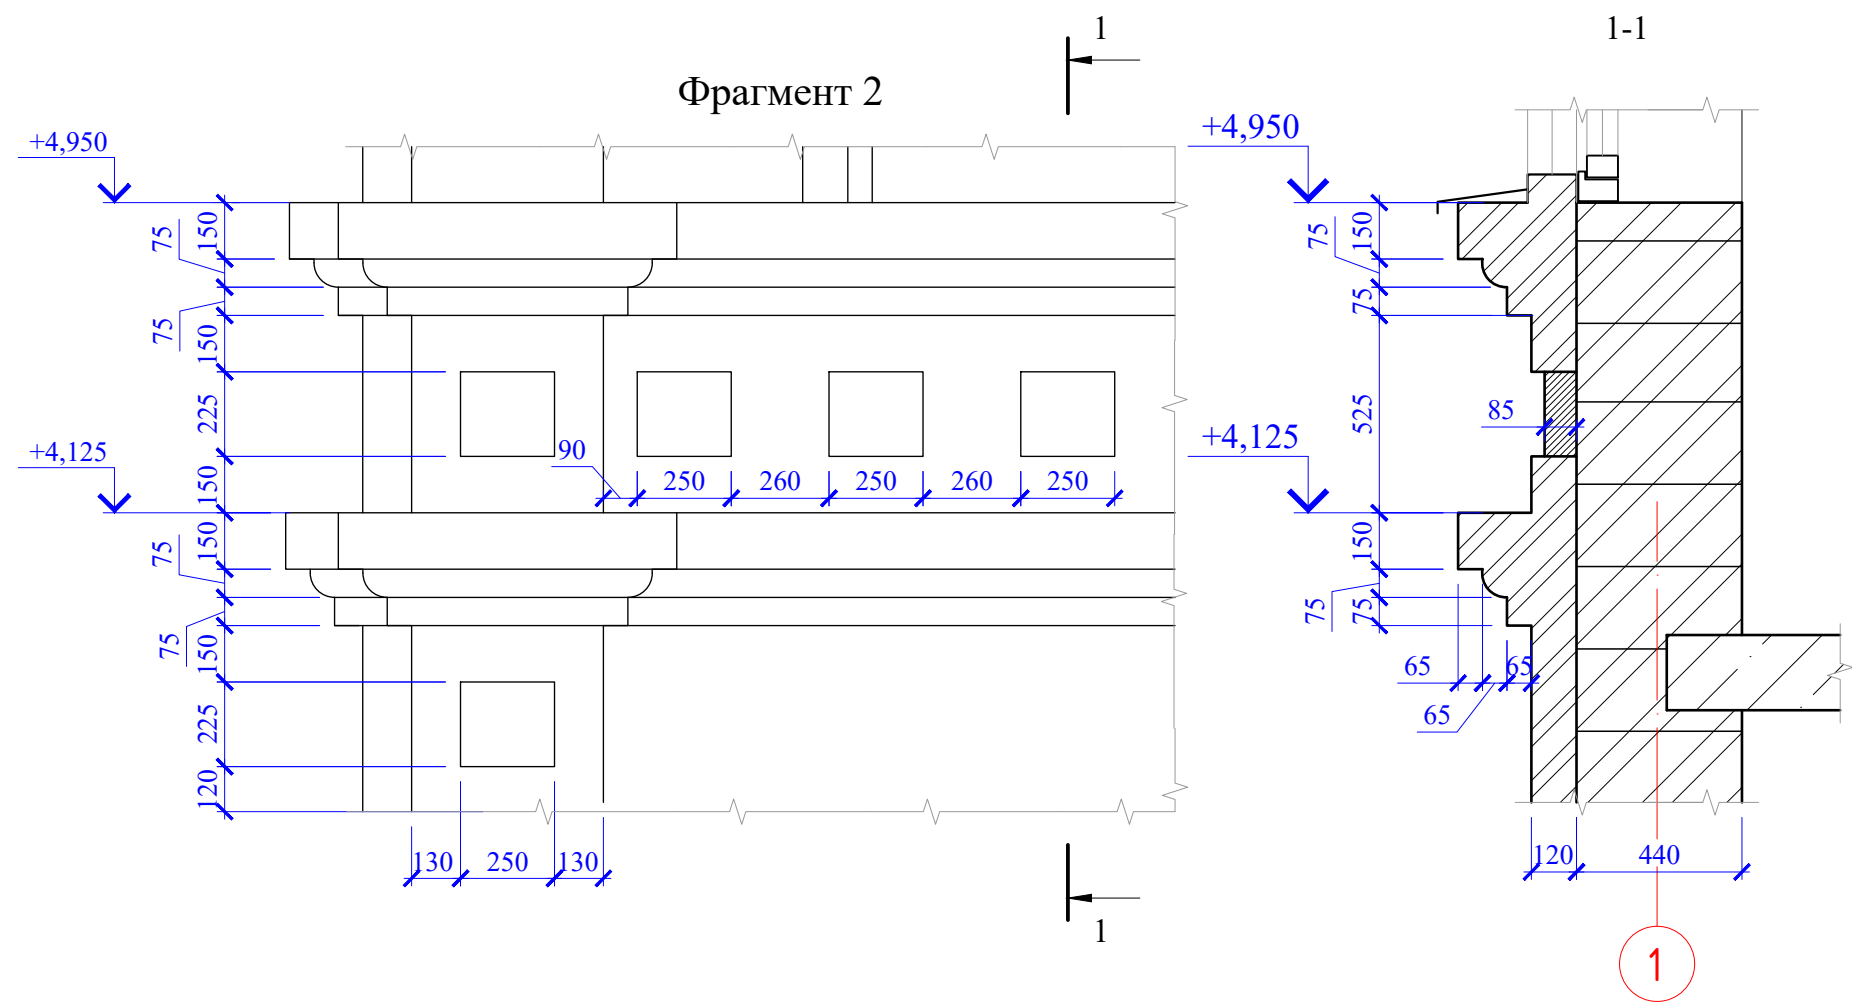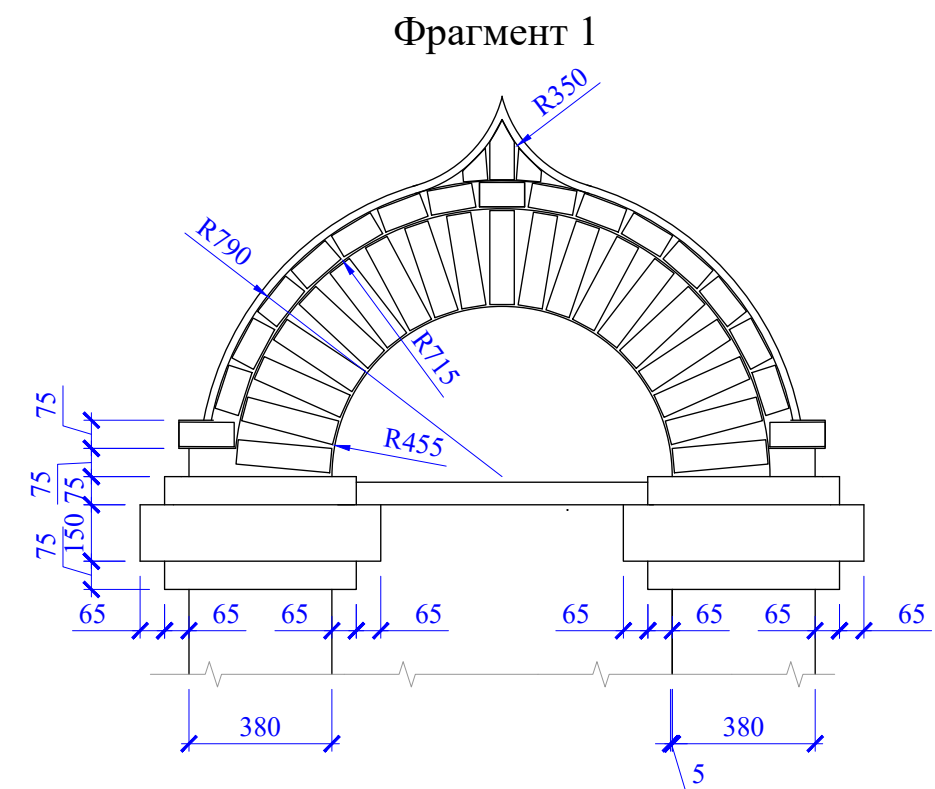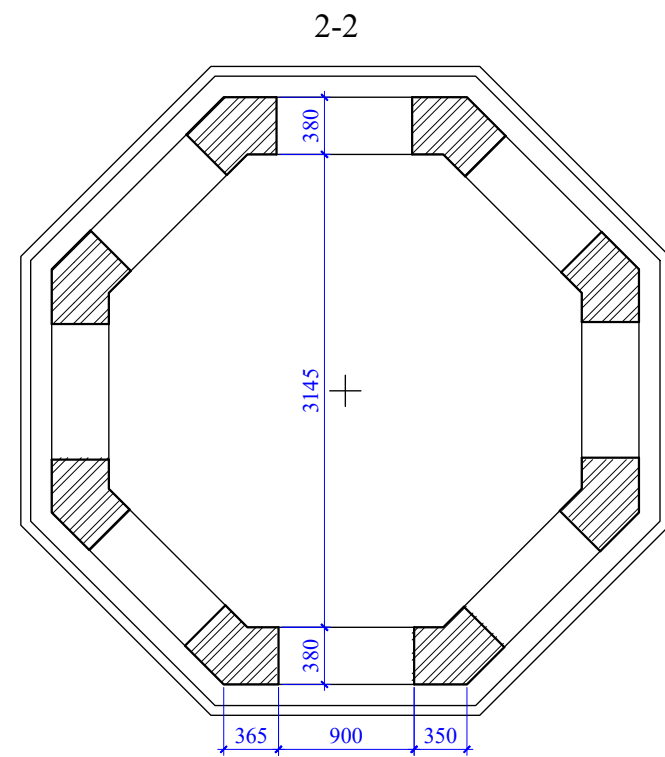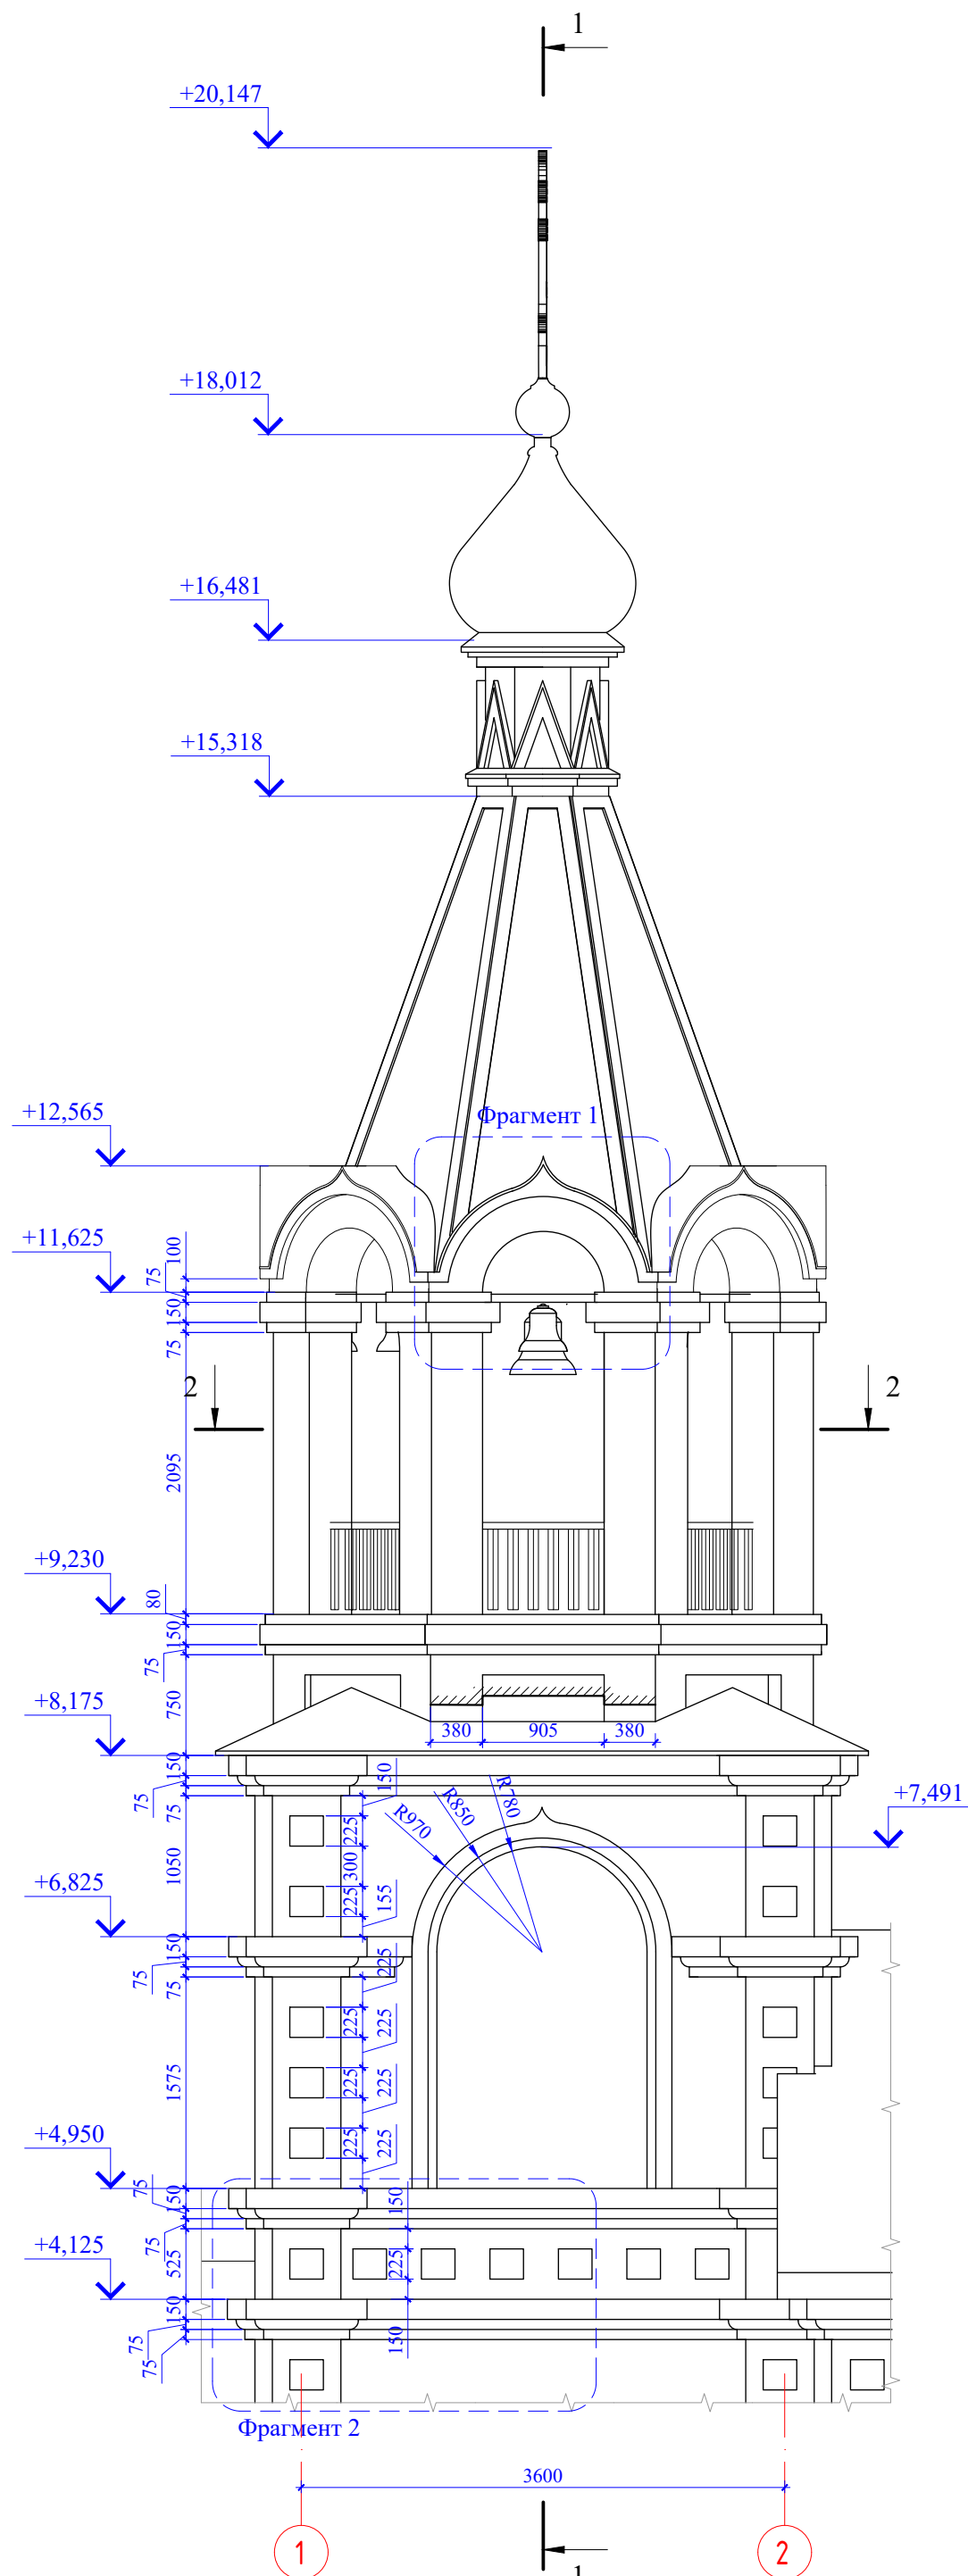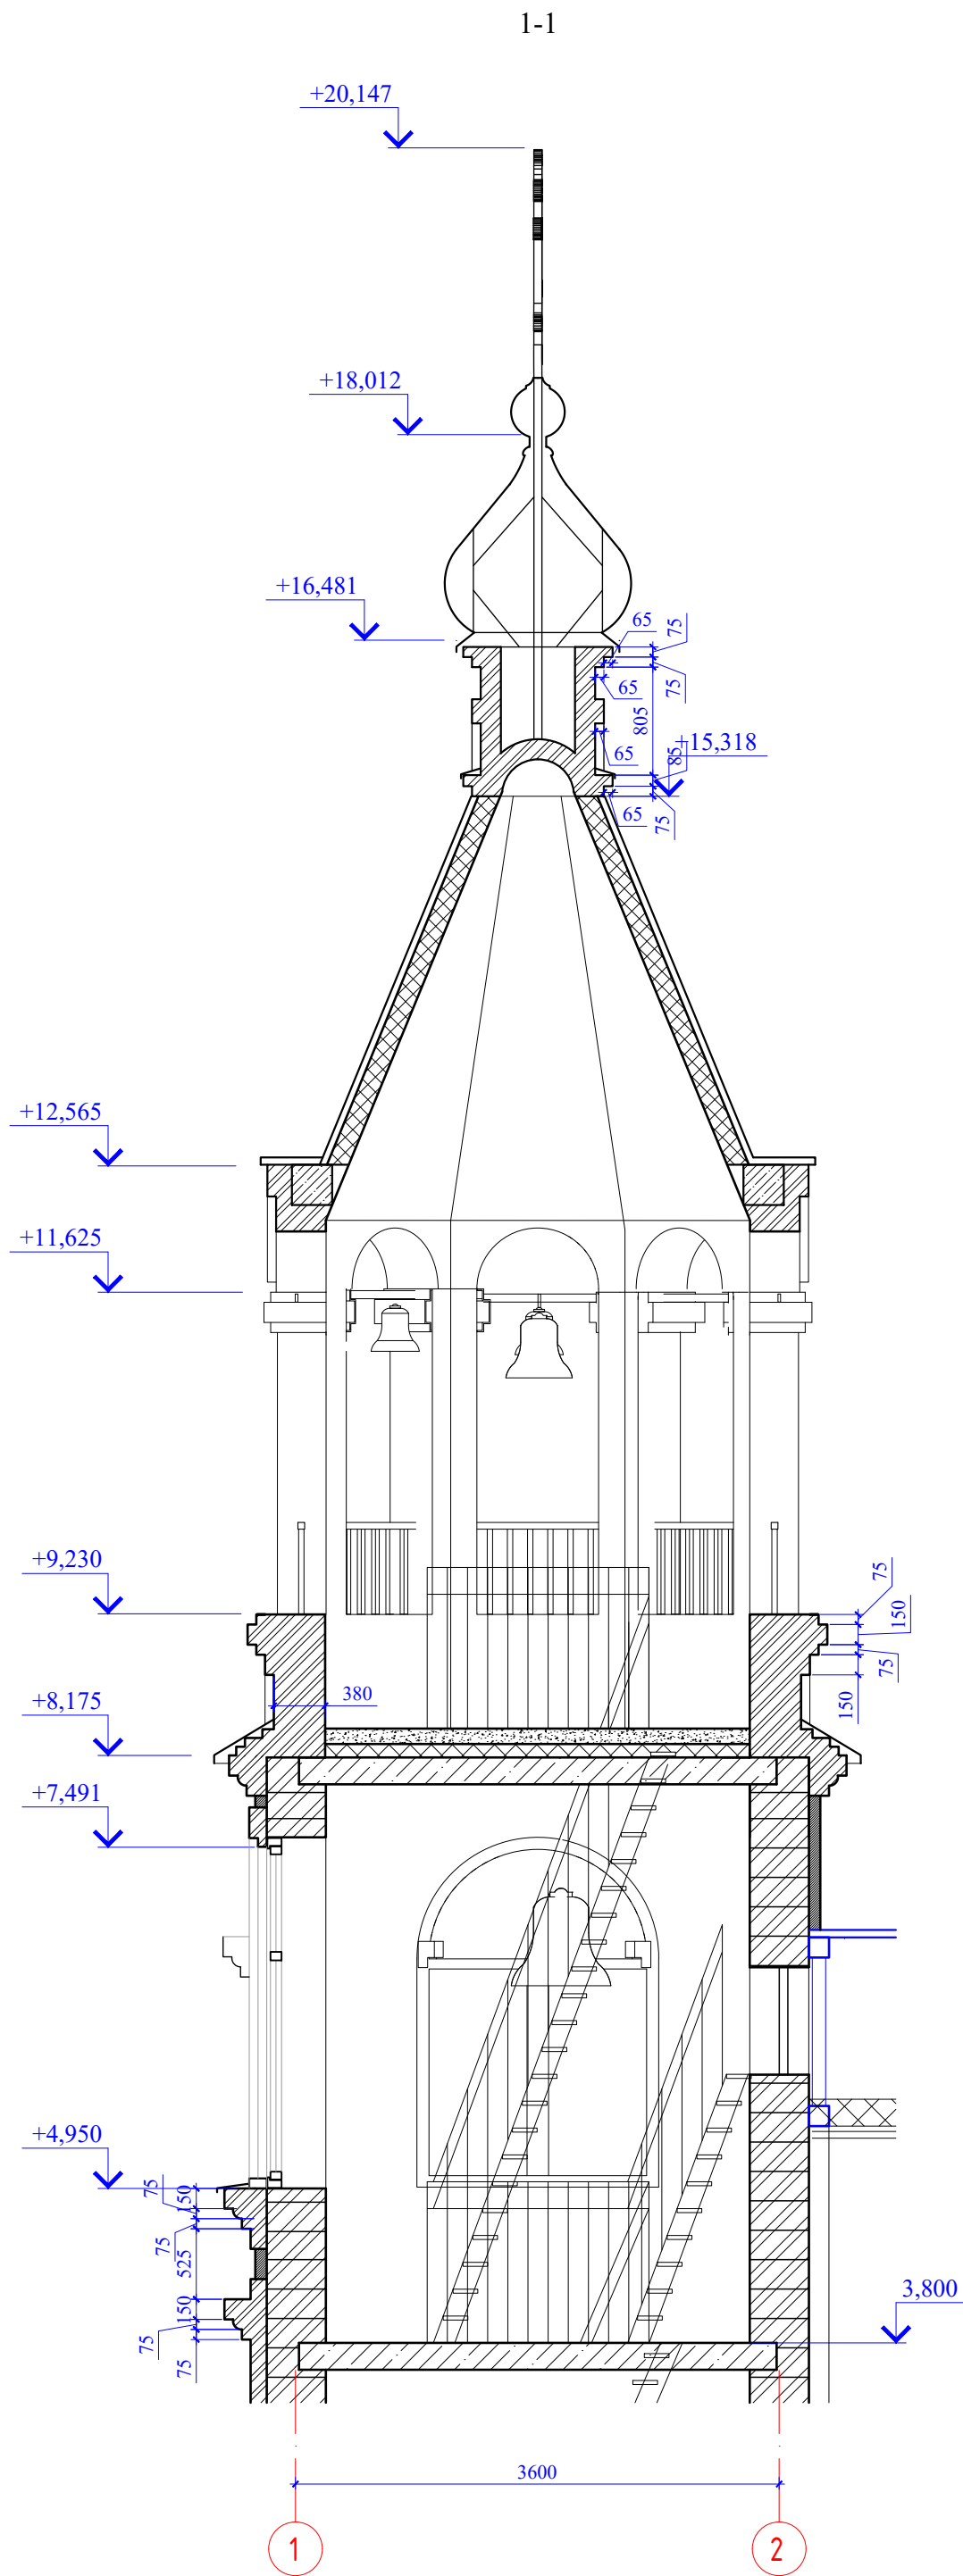


						0143.03.2023-AP			
						Храм Рождества Пресвятой Богородицы по адресу ул. Березовская рядом с профилакторием в Московском р-не г. Нижний Новгород			
Изм.	Кол.Уч	Лист	№ док	Подпись	Дата		Стадия	Лист	Листов
Разработал	Иняев В.А.						П	19	
ГАП	Иняев А.А.								
Н.контр.	Иняев А.А.								

Согласовано					
Изм.	Кол.Уч	Лист	№ док	Подпись	Дата
Разработал	Иняев В.А.				
ГАП	Иняев А.А.				
Иняев	№ подл.	Подп. и дата	Взам. инв. №		

Фрагмент - наличники 1

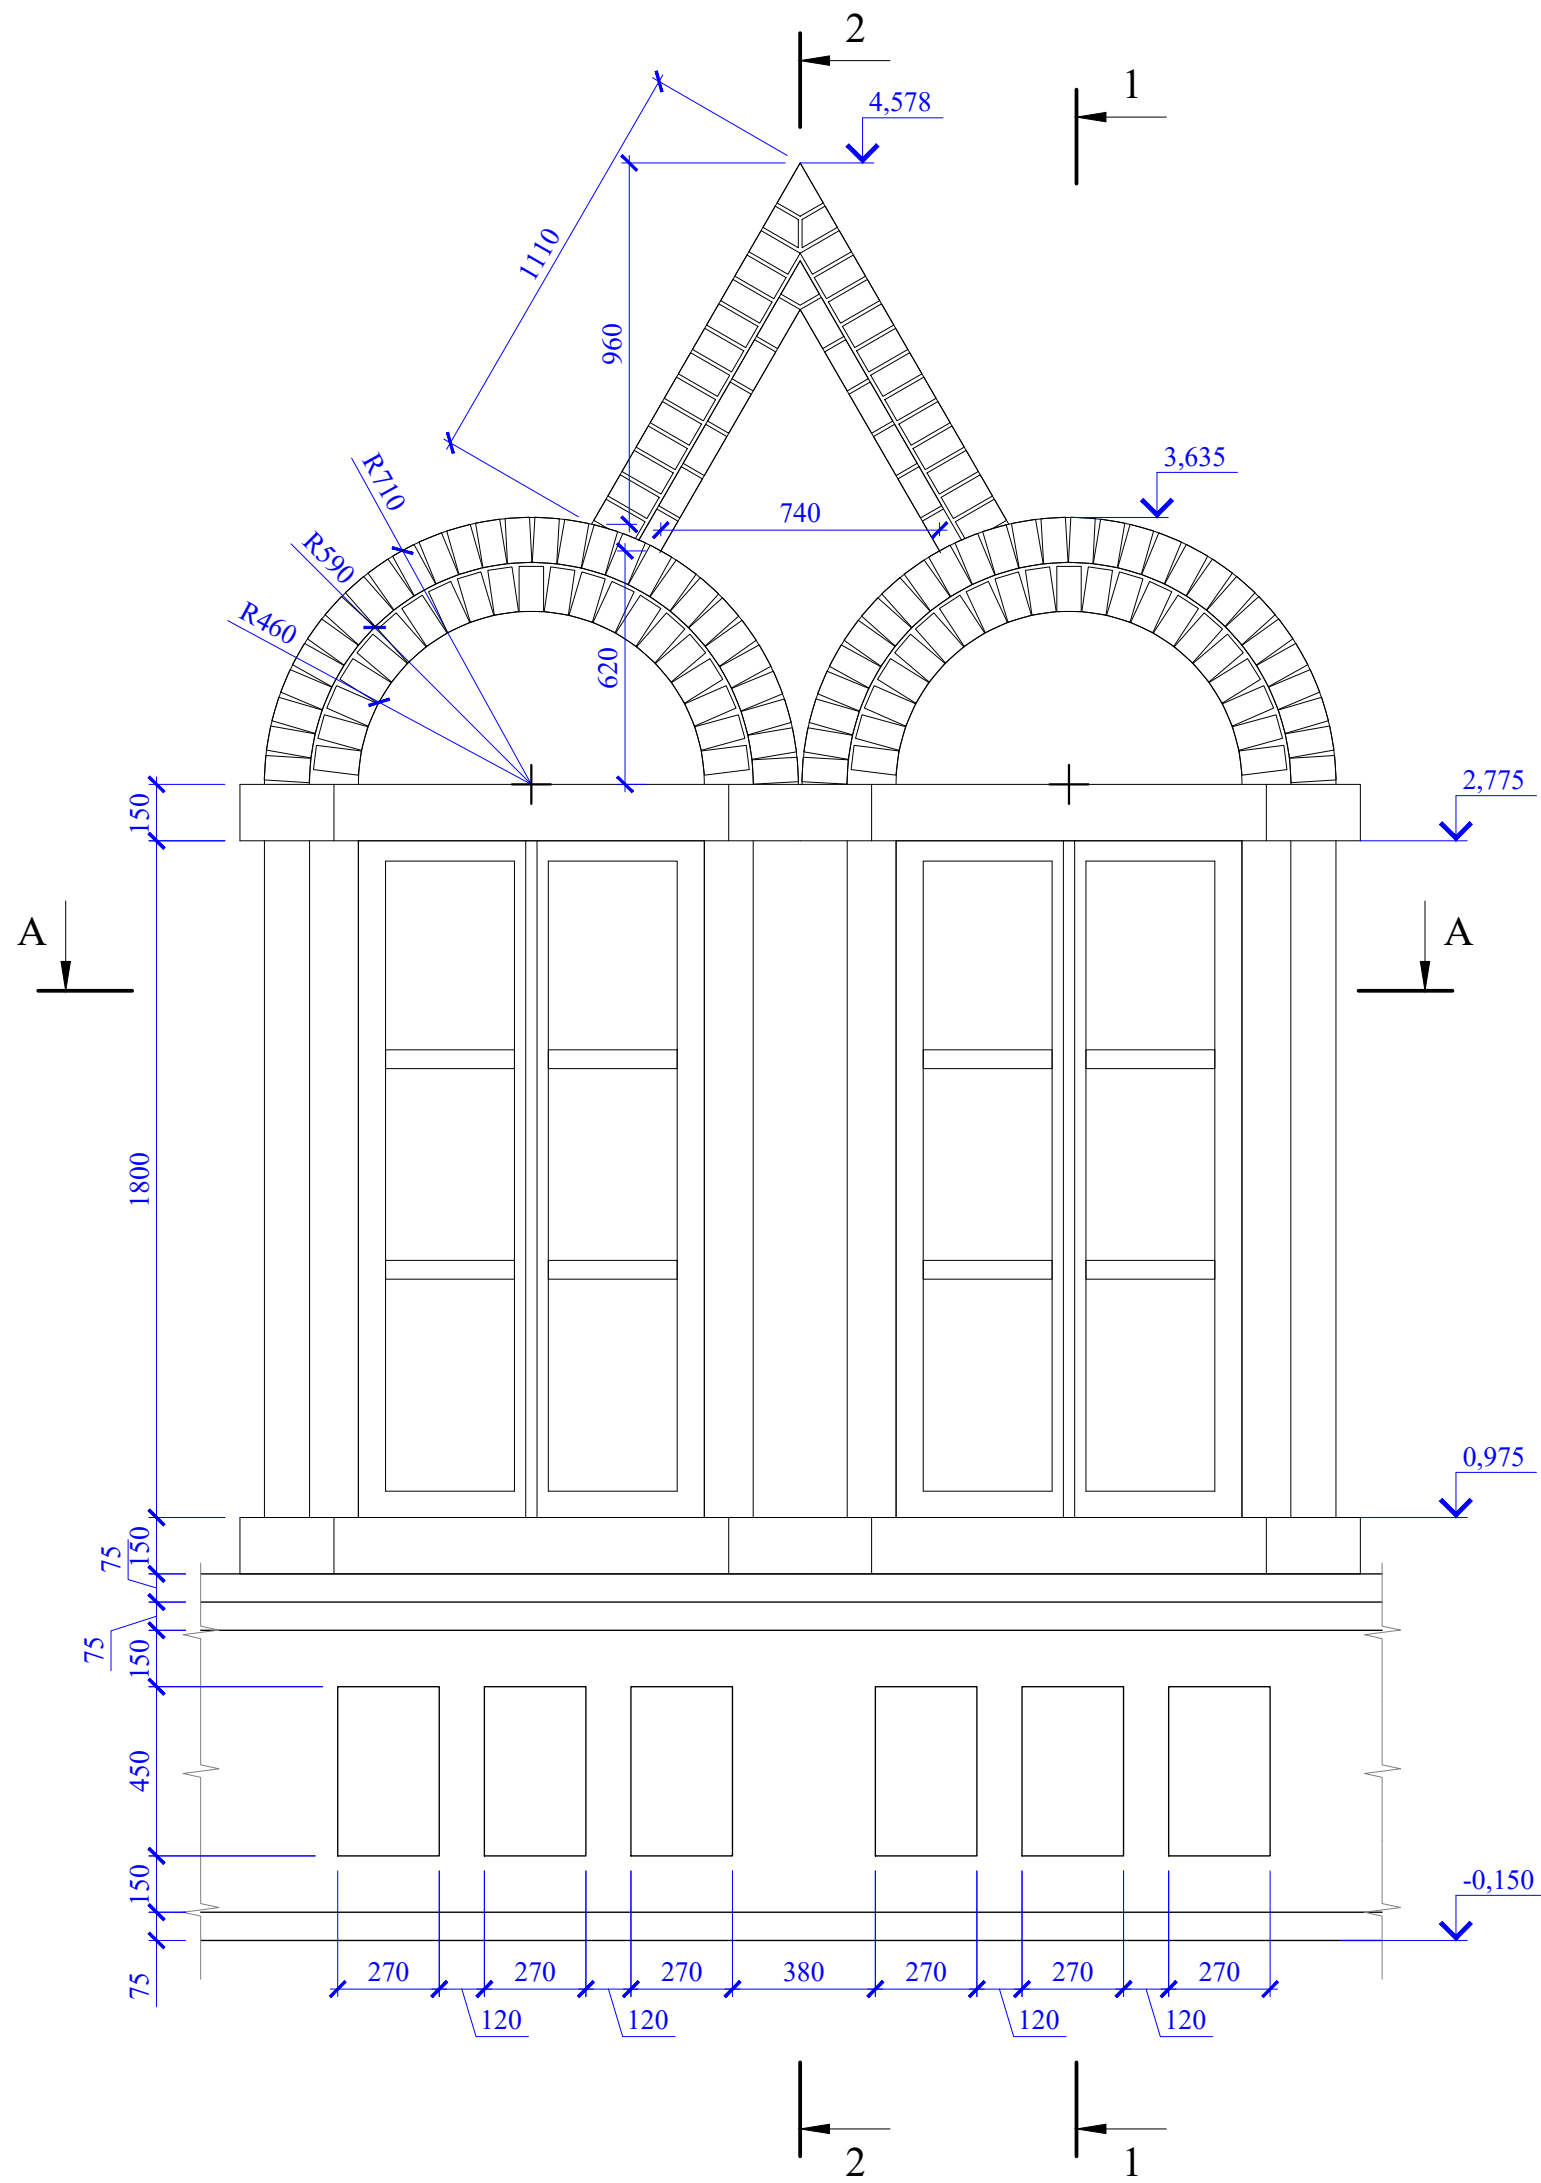


A-A

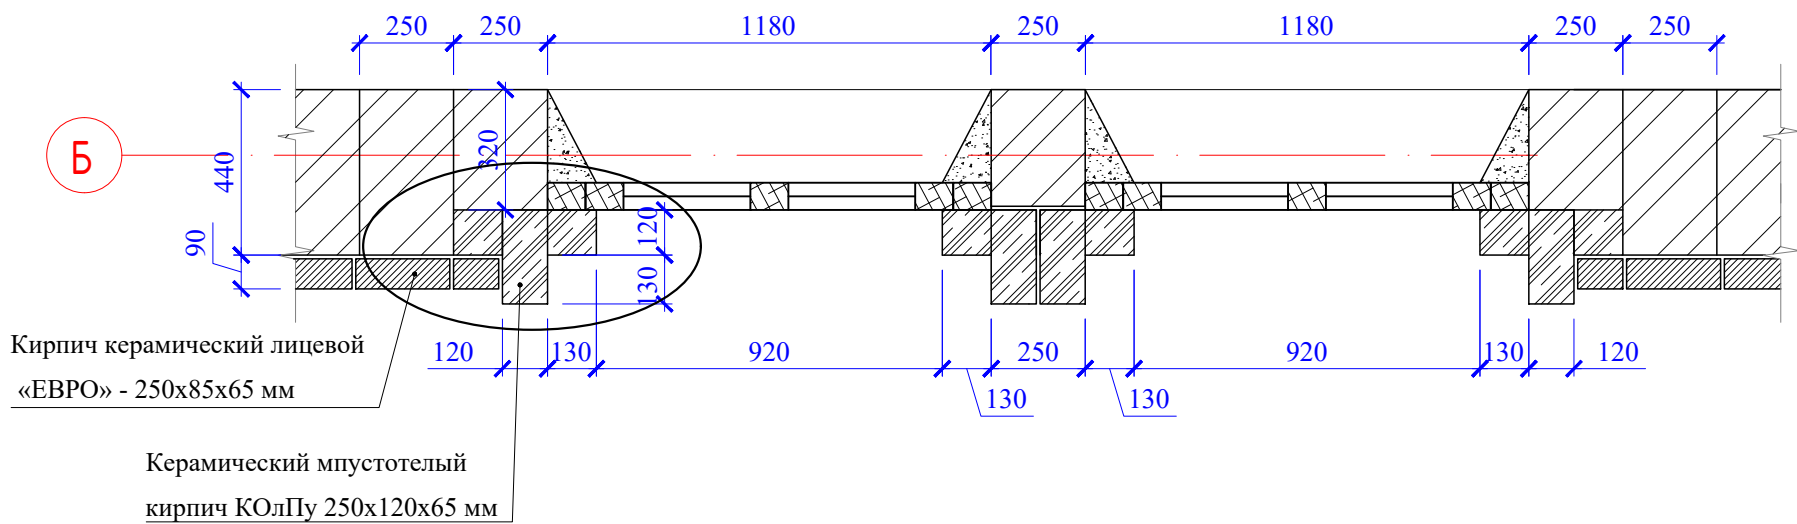


Кирпич керамический лицевой
«ЕВРО» - 250x85x65 мм

Керамический мпустотелый
кирпич КОлПу 250x120x65 мм

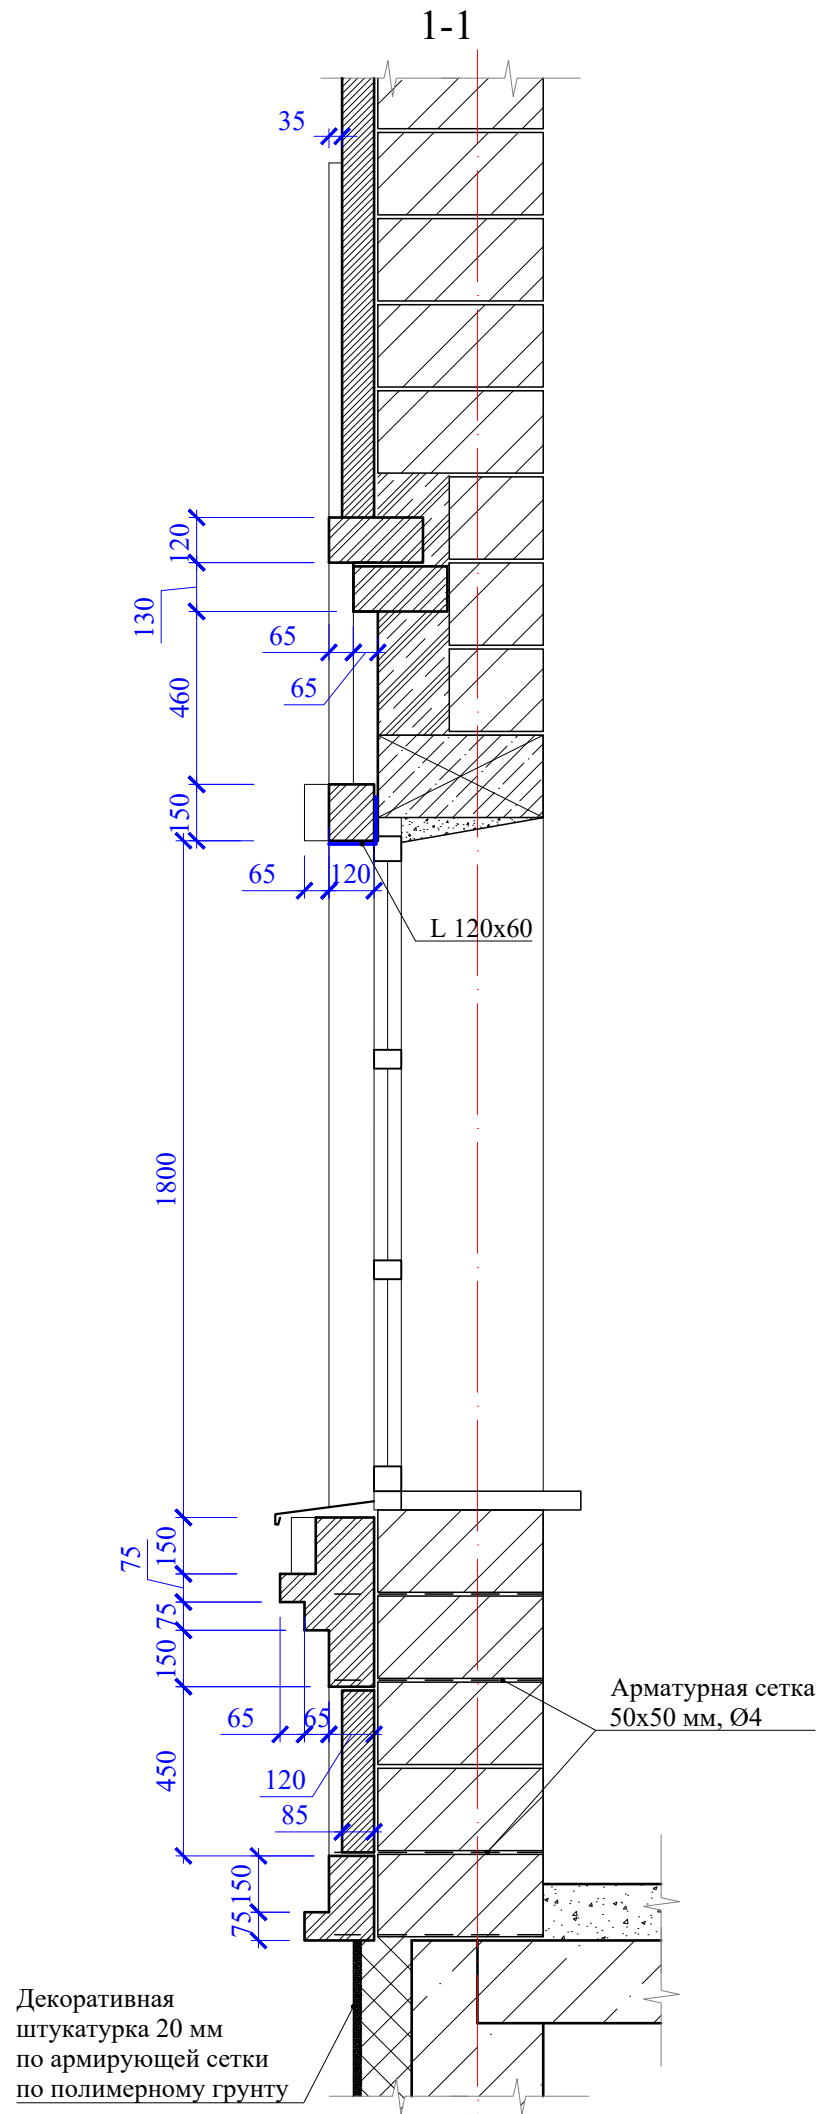






Б

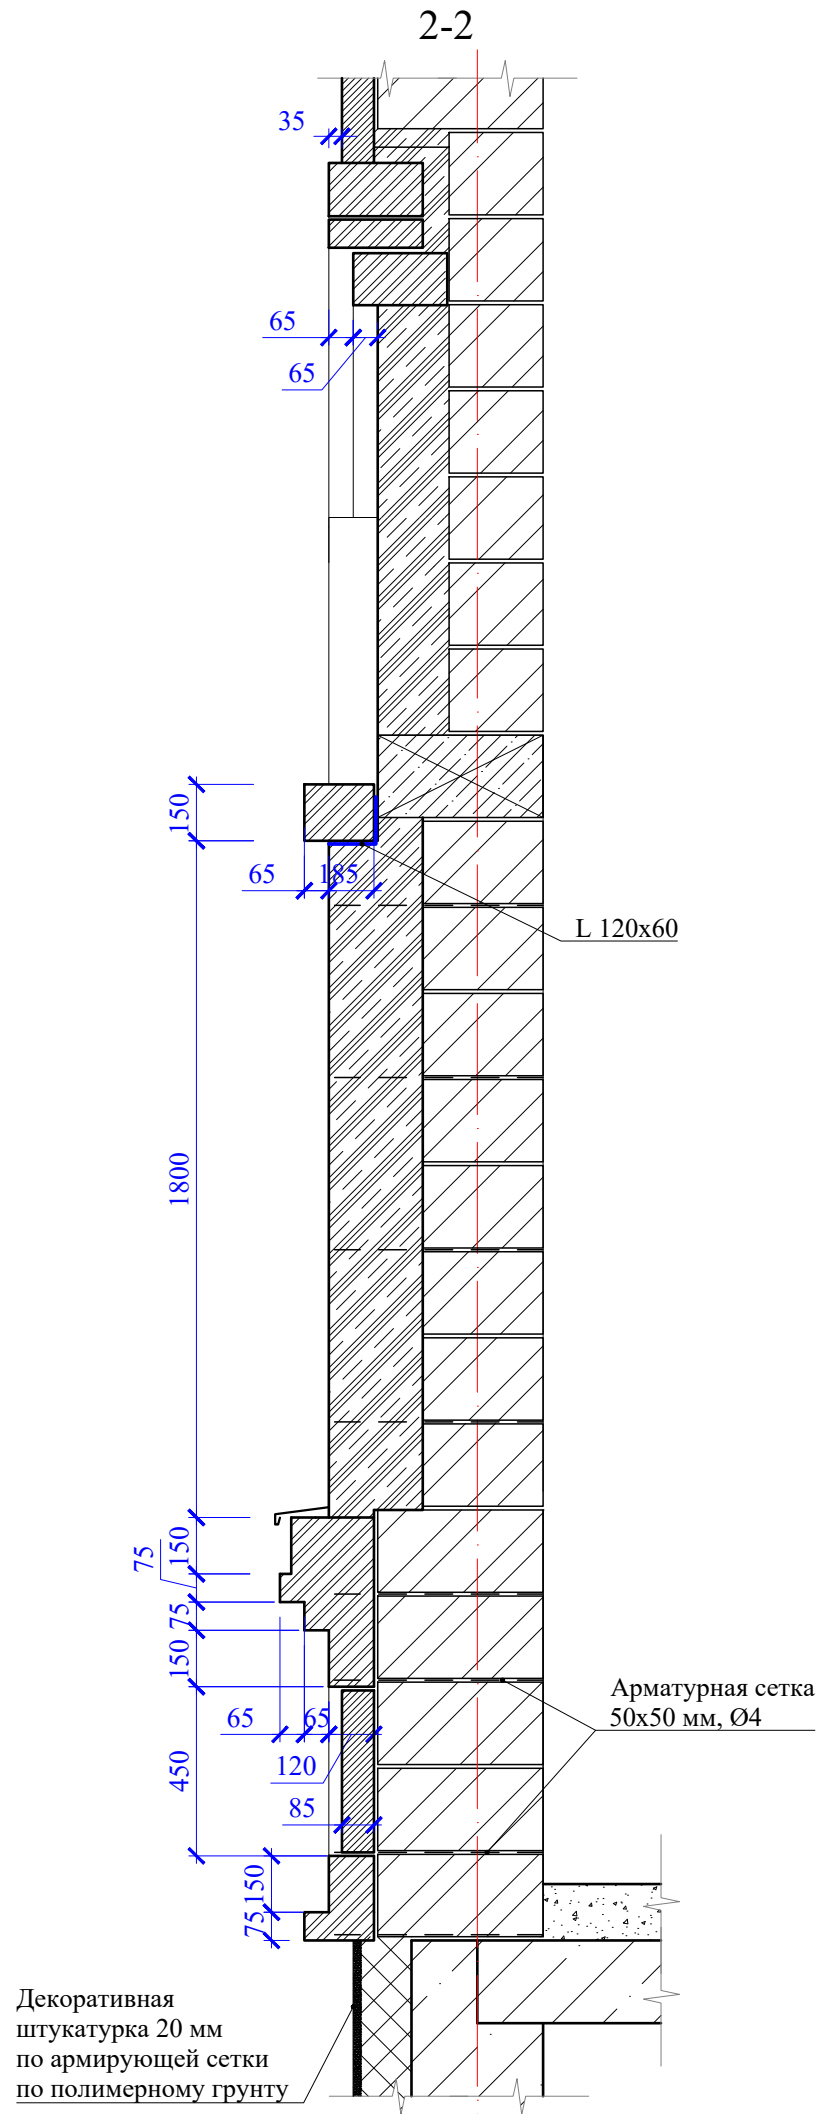

Б

						0143.03.2023-АР			
						Храм Рождества Пресвятой Богородицы по адресу ул. Березовская рядом с профилакторием в Московском р-не г. Нижний Новгород			
Изм.	Кол.Уч	Лист	№ док	Подпись	Дата				
Разработал	Иняев В.А.						Стадия	Лист	Листов
ГАП	Иняев А.А.						П	20	
						Фрагмент - наличники 1, М 1:20.	«ООО Творческая мастерская архитектора Иняева А.А.»		
Н.контр.	Иняев А.А.								

Инв. № подл.	Подп. и дата	Взам. инв. №	Согласовано		

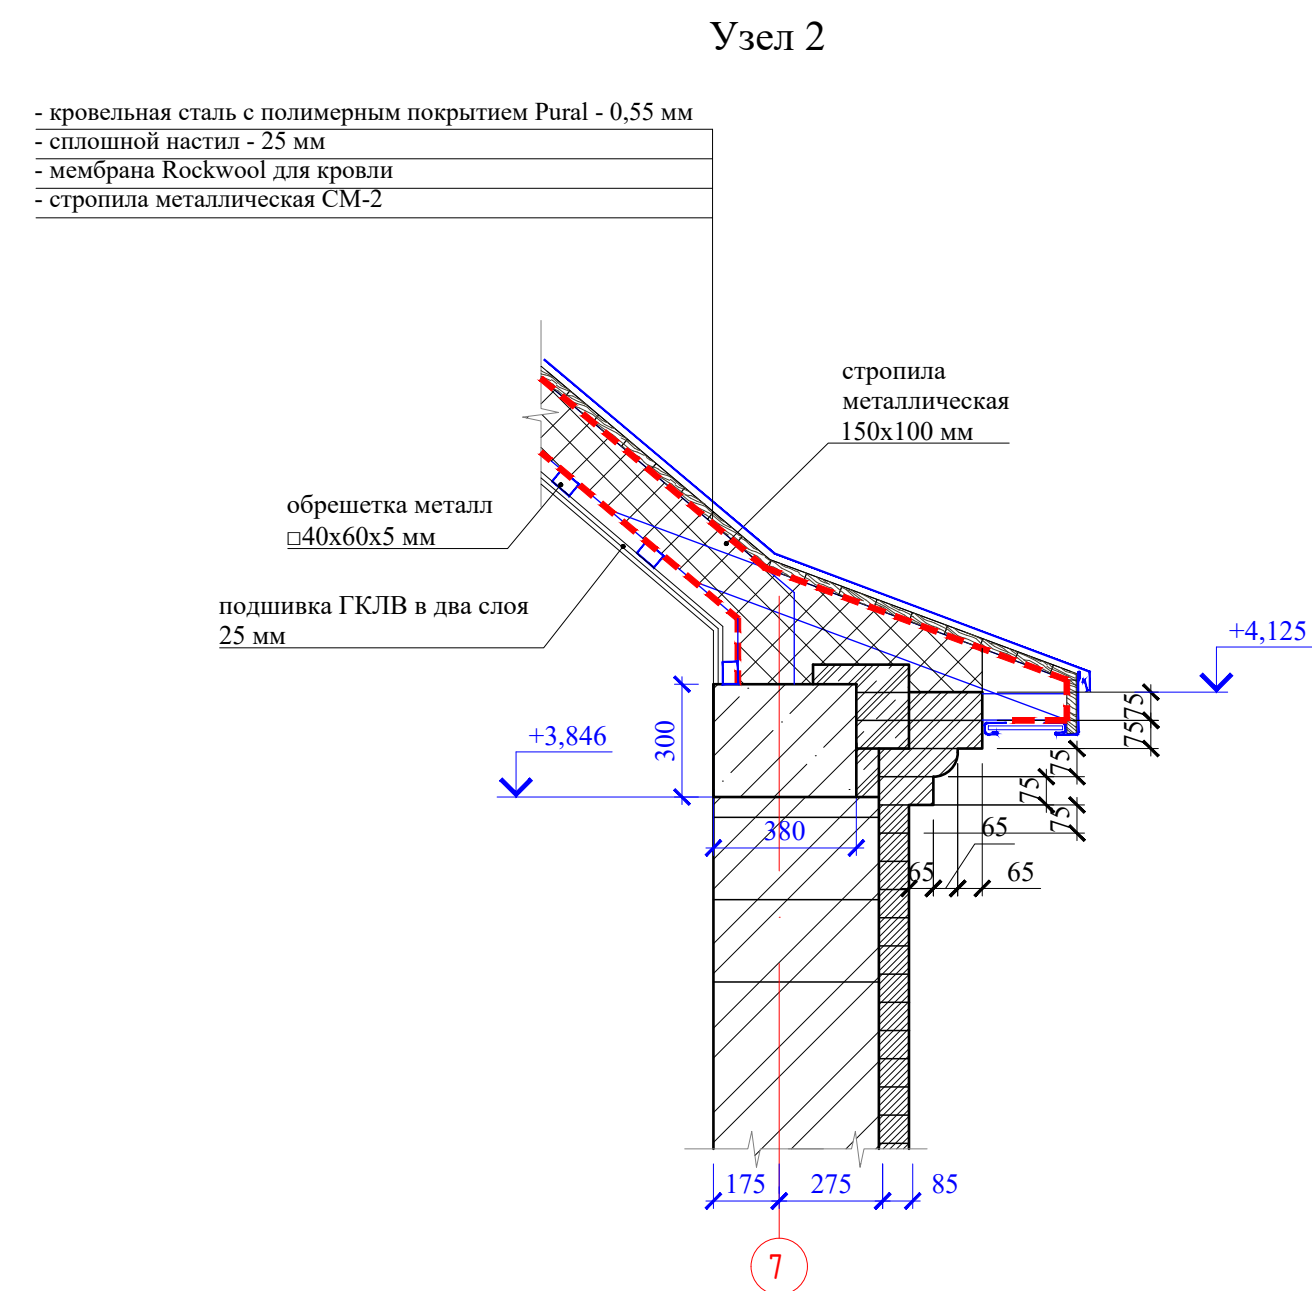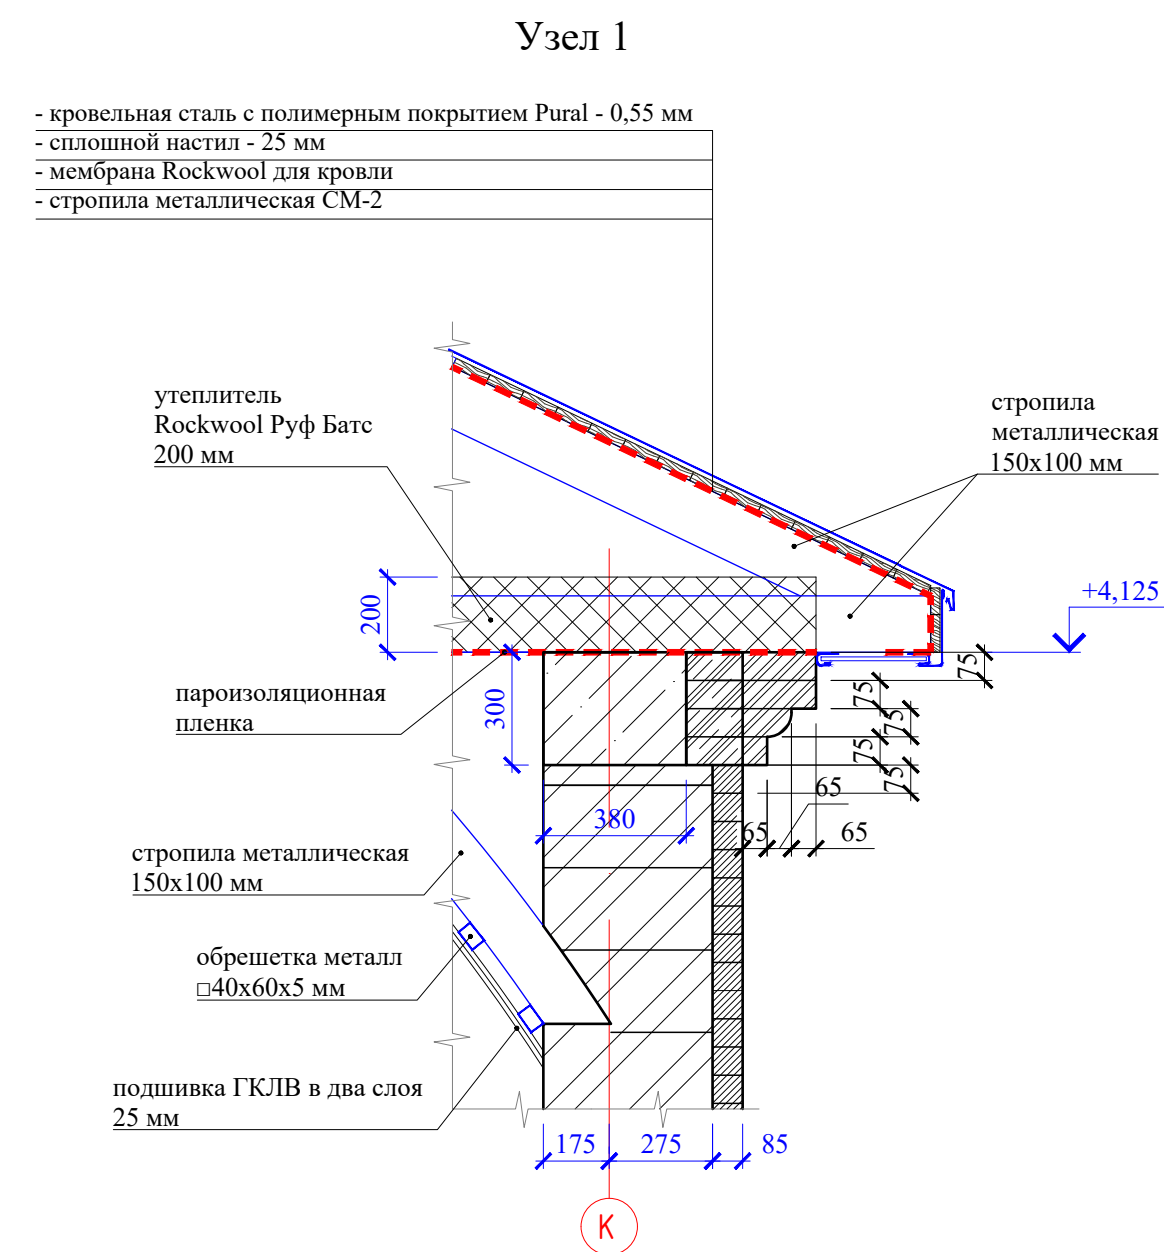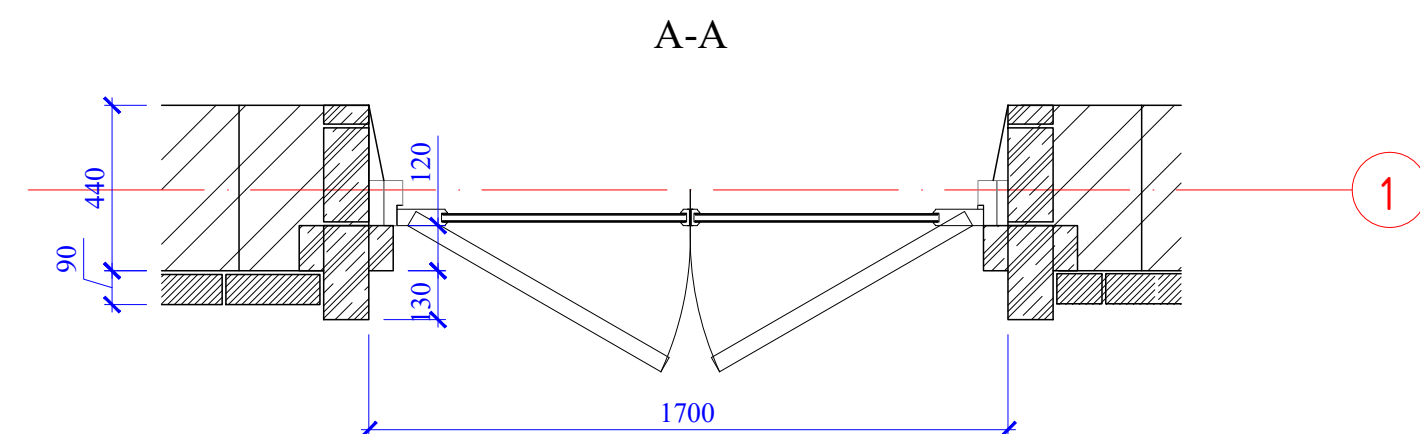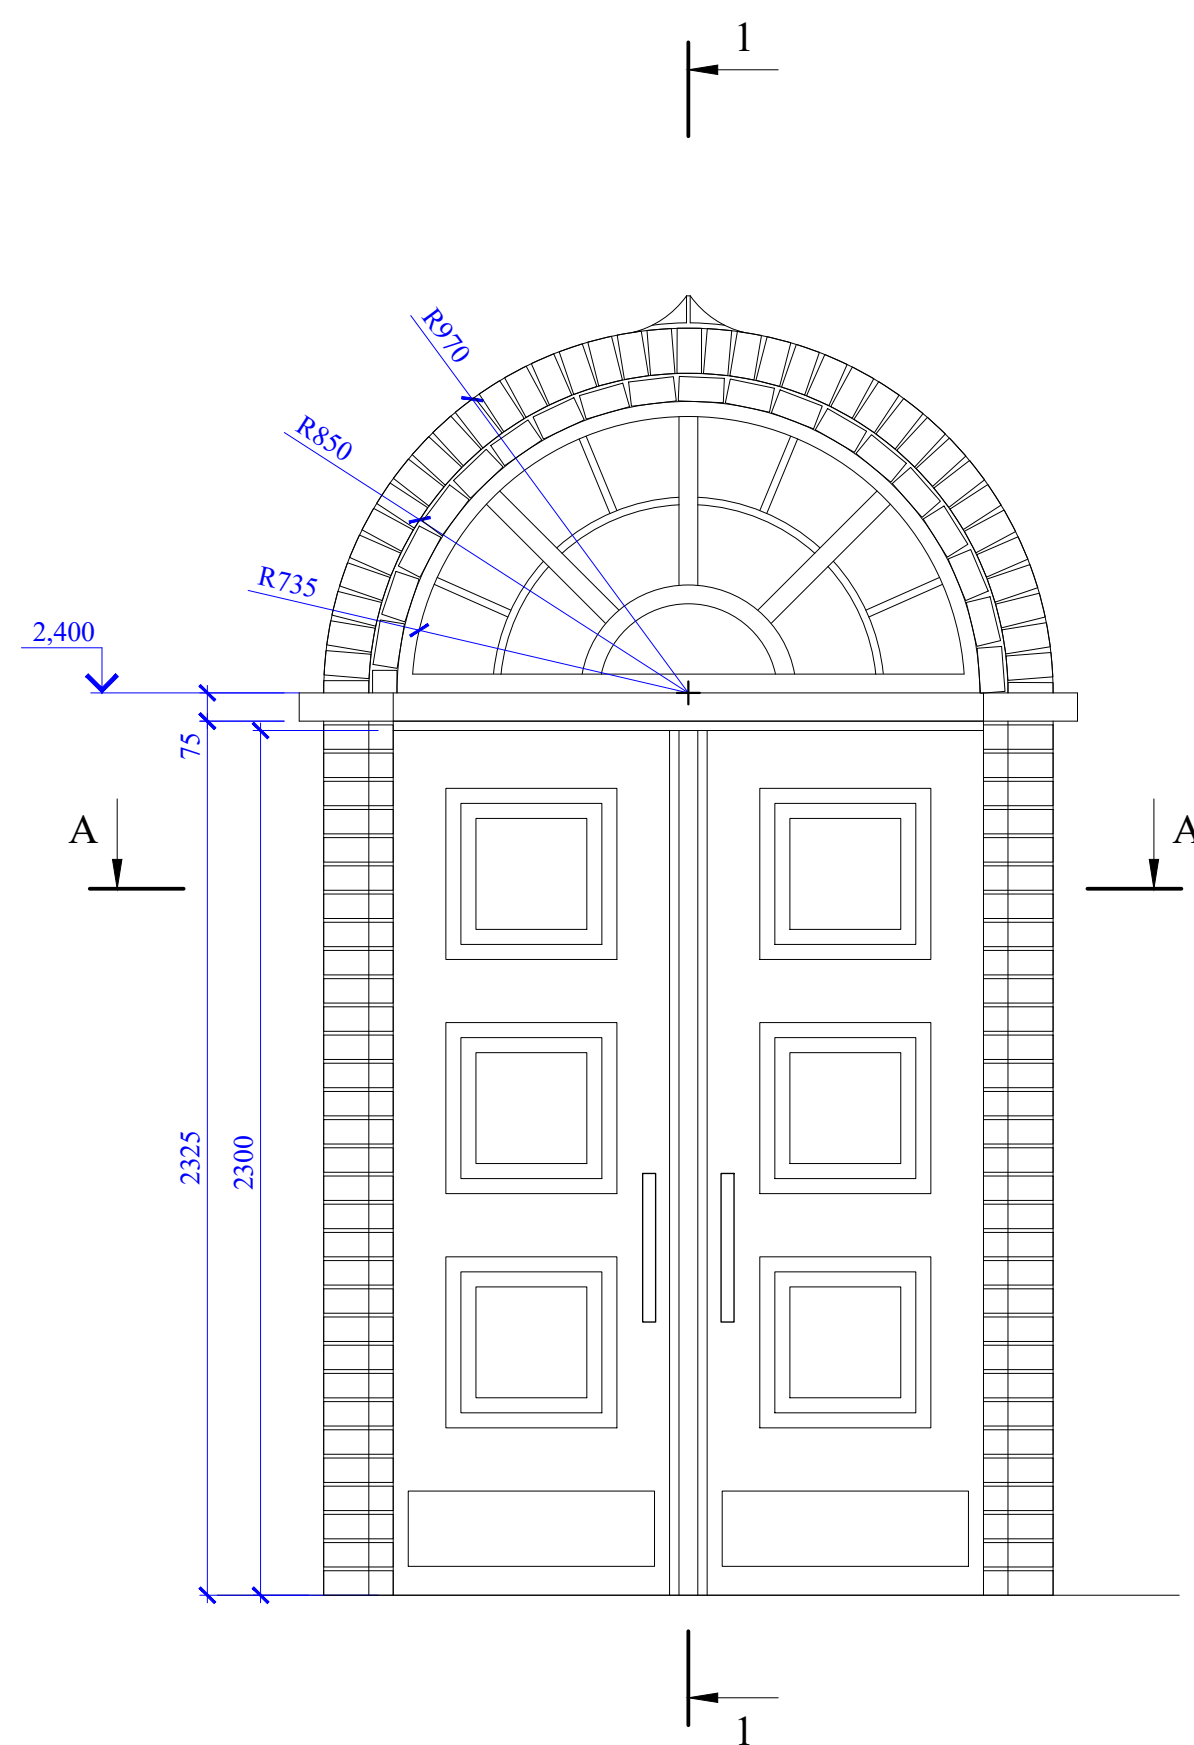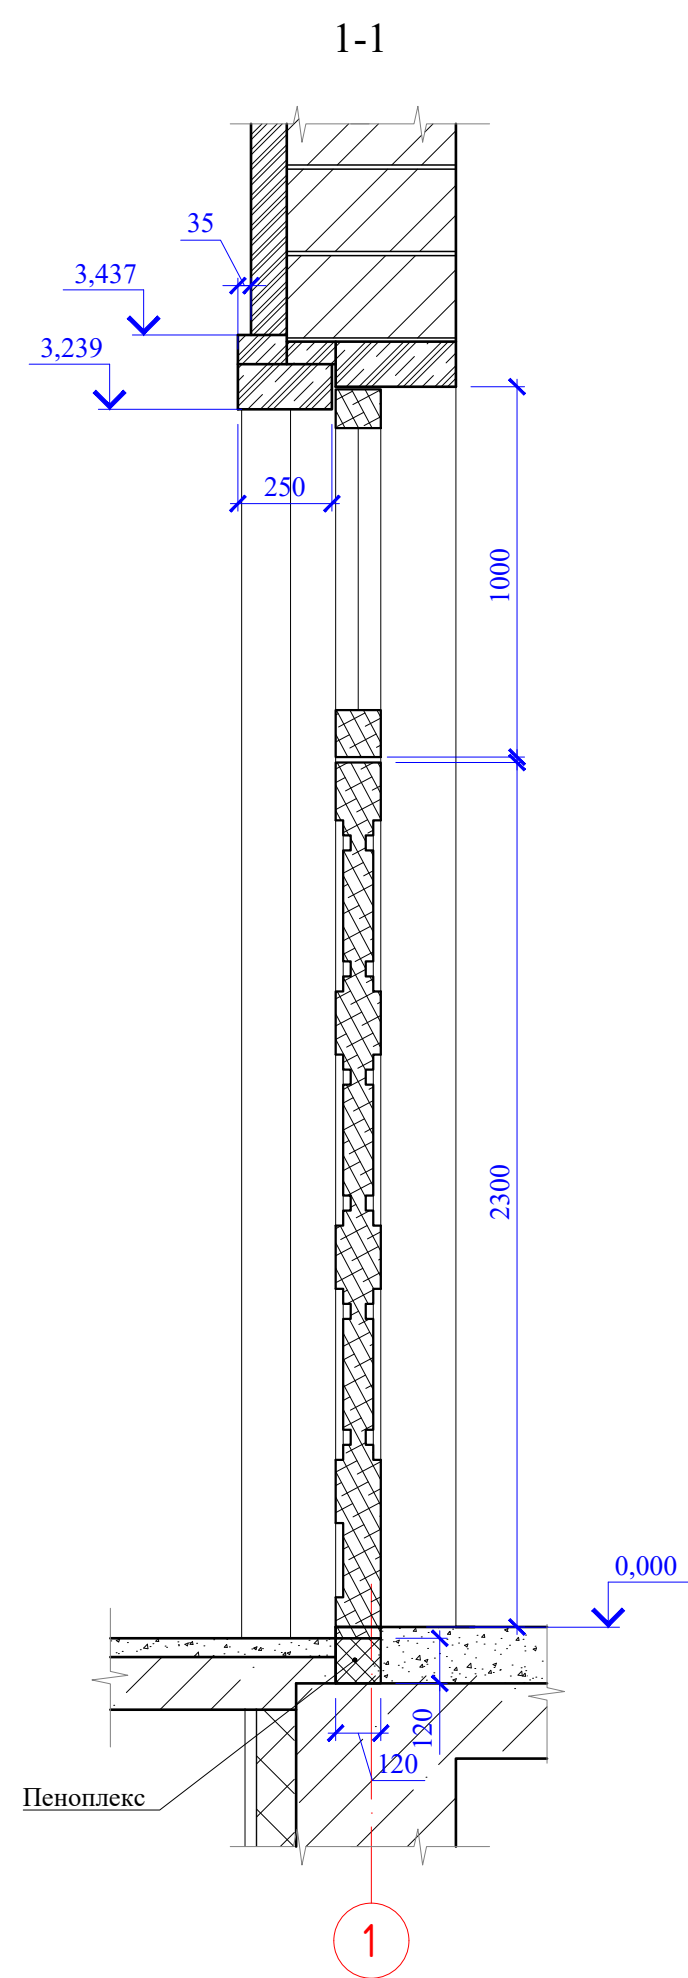

						0143.03.2023-АР			
						Храм Рождества Пресвятой Богородицы по адресу ул. Березовская рядом с профилакторием в Московском р-не г. Нижний Новгород			
Изм.	Код.Уч.	Лист	Листок	Подпись	Дата				
Разработал	Иняев В.А.						Стадия	Лист	Листов
ГАП	Иняев А.А.						П	22	
Н.контр.	Иняев А.А.					Фрагмент - портал главного входа. Узел 1. Узел 2. М 1:20.	«ООО Творческая мастерская архитектора Иняева А.А.»		

Спецификация заполнения дверных проемов

№ поз.	Марка заполнения проема	Размеры	Кол-во шт.	Примечания
Наружная дверь				
1	ДН-1	900 х 2000 проем (1000 х 2100)	2	- металлическая - EI-30 - утепленная - одностворчатая - лев. открывание
2	ДН-2	1500 х 2200 проем (1700 х 2315)	2	- массив - двустворчатая
Внутренняя дверь				
3	Д-1	900 х 2000 проем (1000 х 2100)	2	- массив, МДФ - одностворчатая - прав. открывание
4	Д-2	800 х 2000 проем (900 х 2100)	7	- массив, МДФ - одностворчатая - прав. открывание
5	Д-3	850 х 2000 проем (950 х 2100)	1	- массив, МДФ - одностворчатая - лев. открывание
6	Д-4	1500 х 2200 проем (1700 х 2315)	1	- массив - двустворчатая
7	Д-5	750 х 2000 проем (650 х 2100)	2	- массив, МДФ - одностворчатая - прав. открывание
8	Д-6	люк-лаз 1000х800	2	- металлическая - прав. открывание




ВЕДОМОСТЬ ОТДЕЛКИ ПОМЕЩЕНИЙ

Наименование или номер помещения	Вид отделки элементов интерьеров			
	Потолок	Площадь м2	Стены или перегородки	Площадь м2
1, 2, 3, 4, 5, 6, 7, 8, 9, 10 (Подклет на отм.-3,200)	Подвесные потолки "Armstrong"		Шпаклевка, грунтовка, высококачественная покраска RAL - 9016	
1, 2, 3, 4 (1-ый этаж)	Шпаклевка, грунтовка, высококачественная покраска цвет - белый RAL - 9016		Шпаклевка, грунтовка, высококачественная покраска RAL - 9016	
1 (Колокольня на отм.+5,900)	Шпаклевка, грунтовка, высококачественная покраска цвет - белый RAL - 9016		Шпаклевка, грунтовка, высококачественная покраска RAL - 9016	

Спецификация заполнения оконных проемов:


№ поз.	Наименование проема	Обознач. проема	Размер проема	Кол-во шт.	Примечания
1	Окно	ОК-1	800 х 1200	3	
2	-"	ОК-2	920 х 1730	14	
3	-"	ОК-3	*см. эскиз	1	
4	-"	ОК-4	910 х 2325	8	
5	-"	ОК-5	*см. эскиз	2	
6	-"	ОК-6	1565 х 2535	3	

Экспликация полов

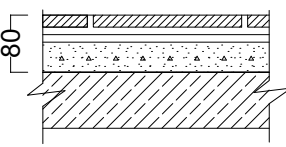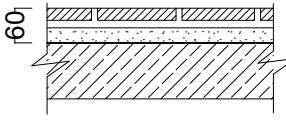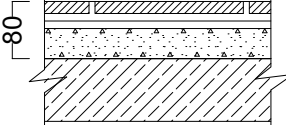Наименование или номер помещения	Тип пола по проекту	Схема пола или номер узла по серии	Элементы пола и их толщина	Площадь пола кв.м
1, 2, 3, 4, 5 7, 8, 9, 10 (Подклет на отм.-3,200)	1		Керамогранит - 8мм Прослойка цементно-песчаного раствора -12мм Выравнивающая стяжка "Ветонит" - 10мм Легкобетонная стяжка (γ=1600кг/м³) - 50мм Железобетонная монолитная плита	141,92
6 (Подклет на отм.-3,200)	2		Керамическая плитка для полов (с шероховатой поверхностью),вариант- керамогранит -15мм Прослойка цементно-песчаного раствора -15мм Выравнивающая цемент.-песч.стяжка М150 - 30мм Железобетонная монолитная плита - 200мм	9,90
1, 2, 3, 4 (1 этаж) 1 (Колокольня на отм.+5,900)	3		Гранитные плиты 300х300 -20мм Прослойка цементно-песчаного раствора -10мм Выравнивающая стяжка "Ветонит" - 10мм Легкобетонная стяжка (γ=1600кг/м³) - 40мм Железобетонное монолитное перекрытие - 200мм	168,80

0143.03.2023-АР

Храм Рождества Пресвятой Богородицы по адресу ул. Березовская рядом с профилакторием в Московском р-не г. Нижний Новгород

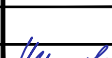Изм.	Кол.Уч	Лист	№док	Подпись	Дата	Стадия	Лист	Листов
Разработал	Иняев В.А.							
ГАП	Иняев А.А.					П	23	
						«ООО Творческая мастерская архитектора Иняева А.А.»		
Н.контр.	Иняев А.А.							

Спецификация заполнения дверных проемов.
Спецификация заполнения оконных проемов.
Ведомость отделки помещений. Экспликация полов.